



PROJETOS COMPLETO NICHOS EMBUTIDOS EM PORCELANATO

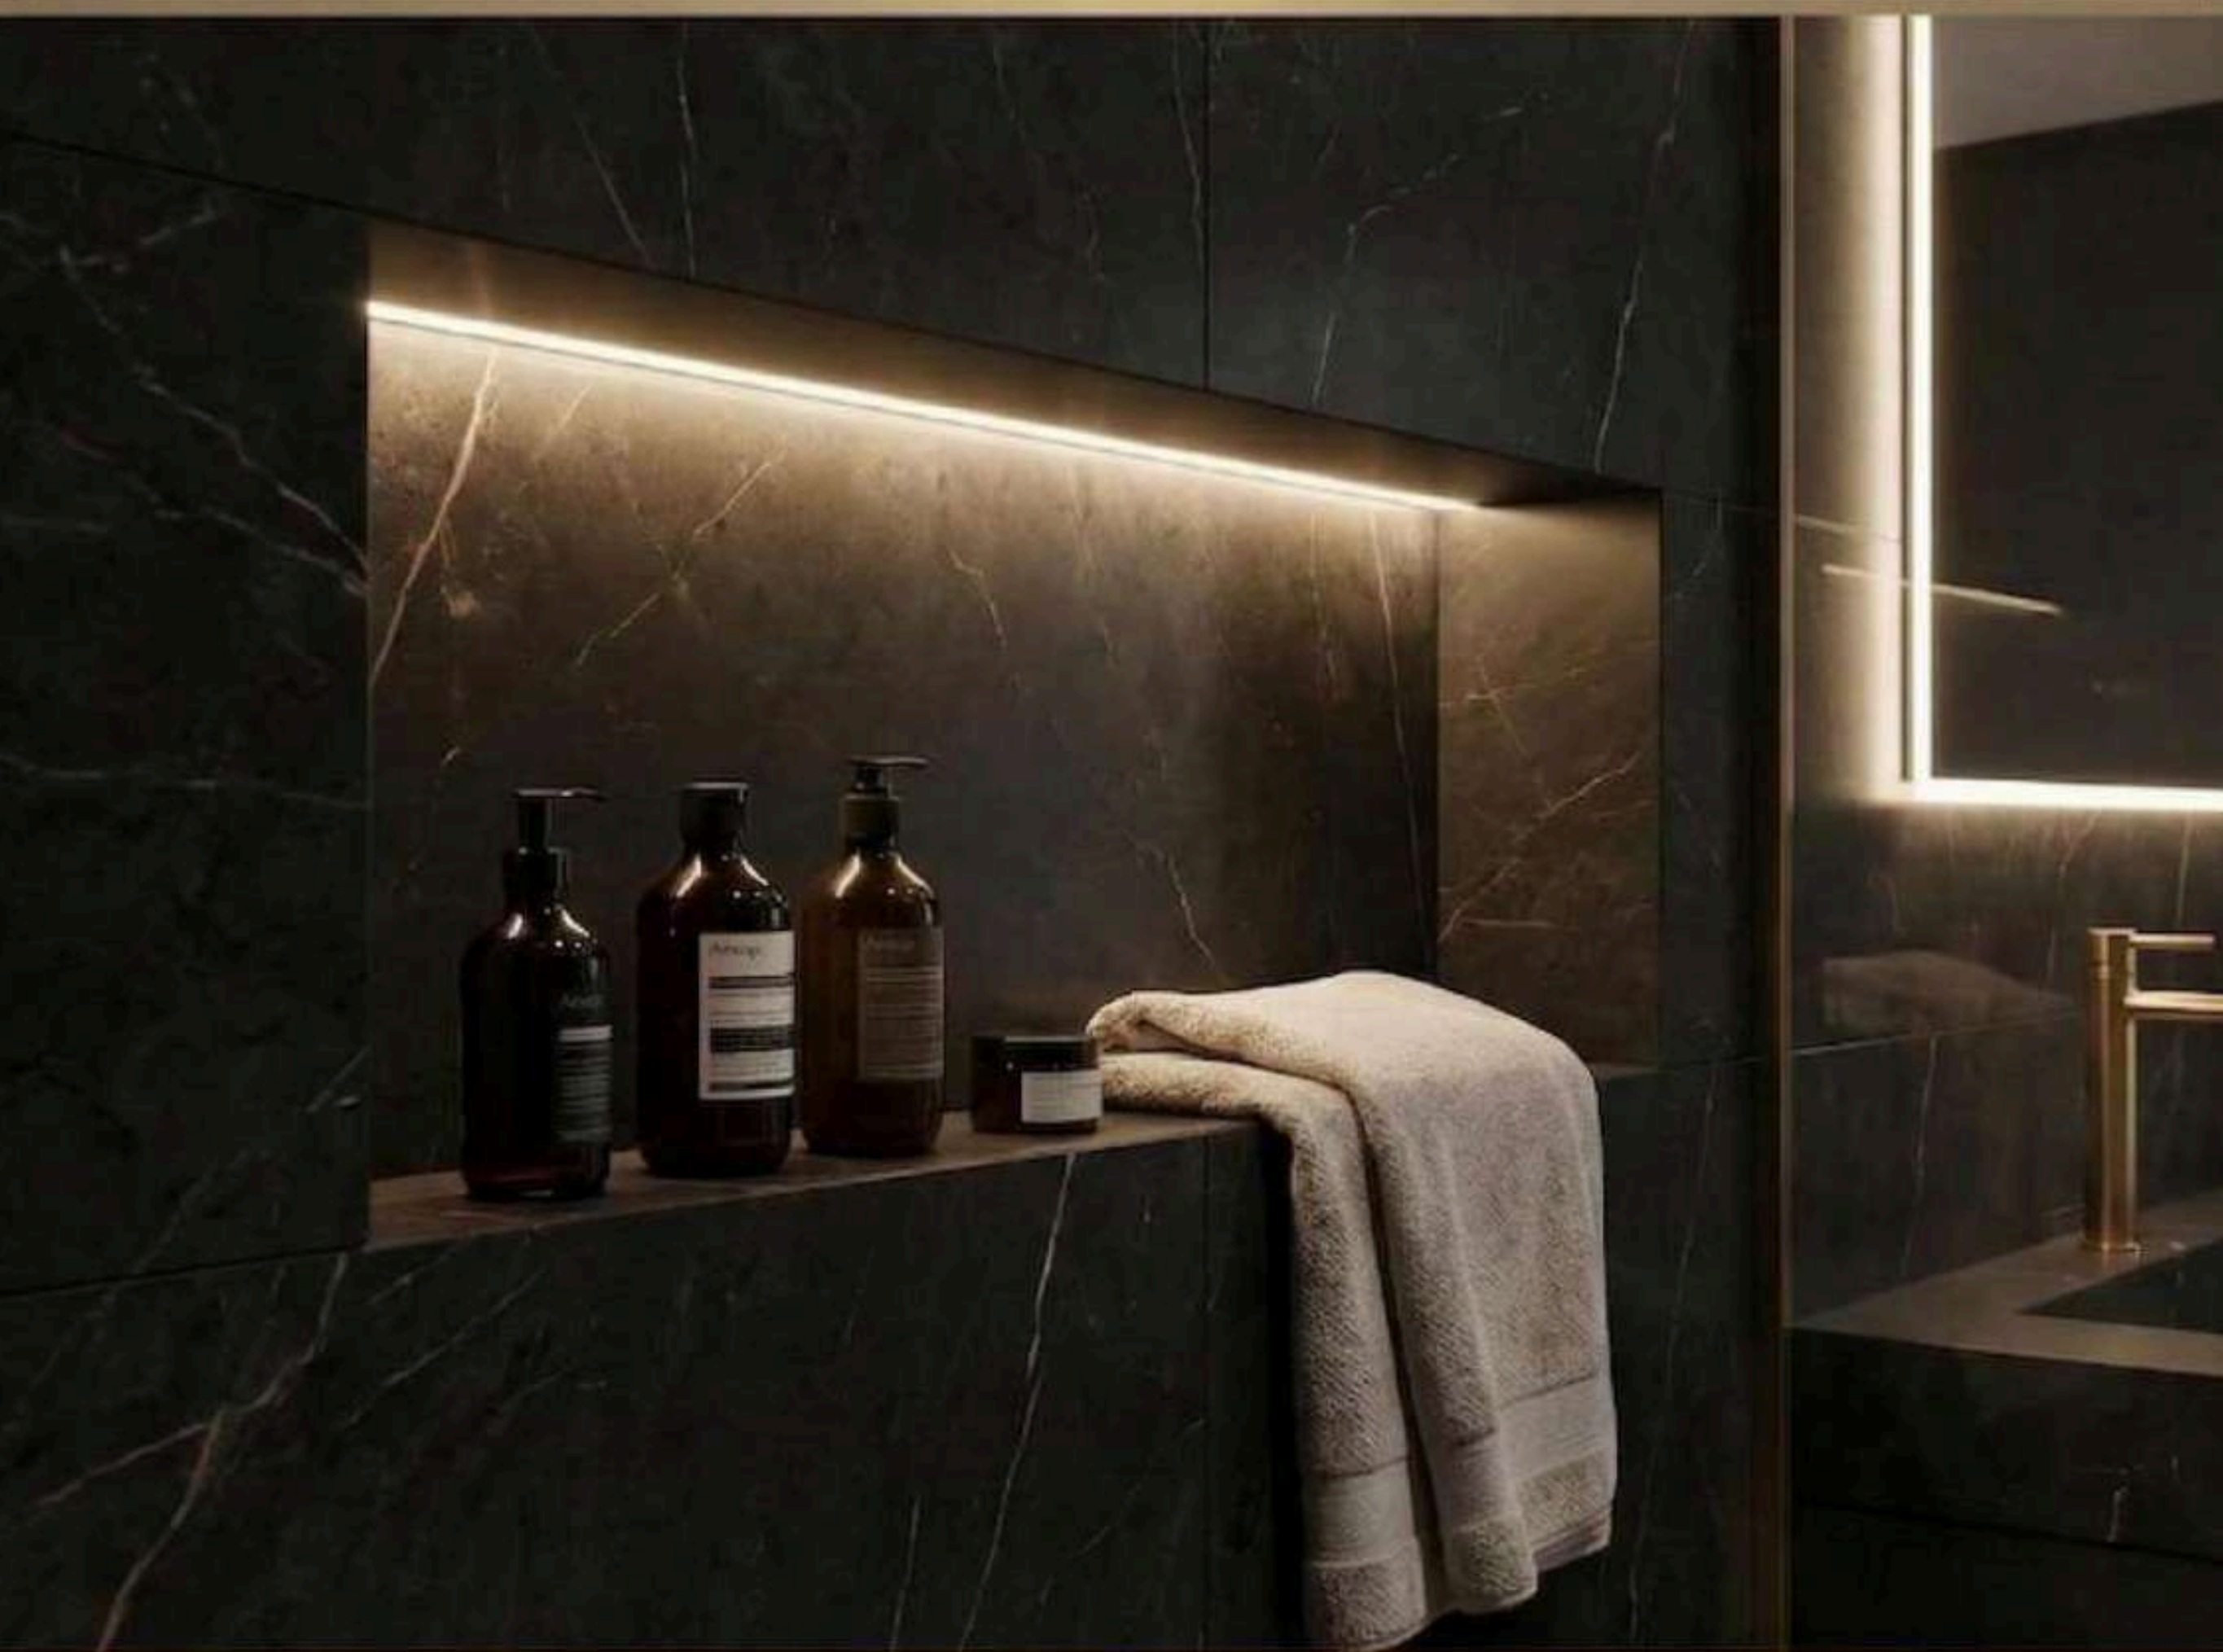

CATÁLOGO DIGITAL | EDIÇÃO PREMIUM

PROJETO 01 — NICHO HORIZONTAL EM PORCELANATO MARMORIZADO COM ACABAMENTO EM MEIA ESQUADRIA

IDEAL PARA BANHEIROS E ÁREAS DE BOX | DESIGN MINIMALISTA E SOFISTICADO

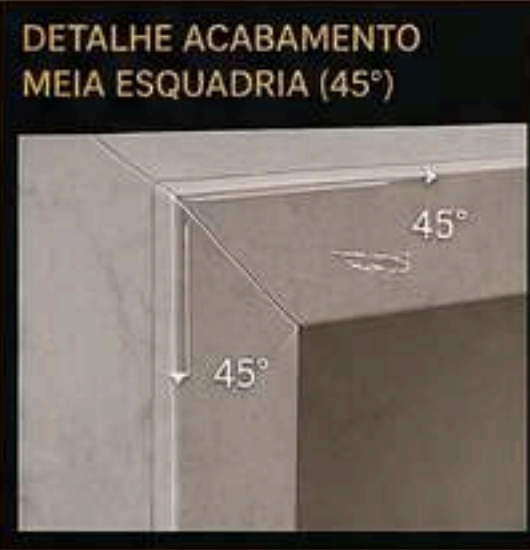

MEDIDAS DAS PEÇAS

TOPO:	80,0 x 12,0 cm
BASE:	80,0 x 12,0 cm
LATERAL (2x):	22,0 x 12,0 cm
FUNDO:	74,0 x 22,0 cm
MOLDURA FRONTAL:	
2x LATERAIS:	30,0 x 3,0 cm
2x TOPO/BASE:	80,0 x 3,0 cm
ESPESSURA DO PORCELANATO:	1,2 cm

PASSO A PASSO DE EXECUÇÃO

1 MARCAÇÃO DO NICHO

Marque o local e as medidas do nicho na parede conforme o projeto.

2 ABERTURA DO VÃO

Abra o vão com serra mármore ou cortadora elétrica nas medidas corretas.

3 REGULARIZAÇÃO

Limpe o interior do vão e aplique chapisco e emboço para nivelar.

4 CORTE DAS PEÇAS

Corte as peças de porcelanato em 45° (meia esquadria) conforme medidas.

5 MONTAGEM SECA

Monte as peças dentro do vão para conferir medidas e alinhamento.

6 FIXAÇÃO

Aplique argamassa ACIII ou específica e fixe as peças começando pelo fundo.

7 ACABAMENTO

Faça o acabamento das juntas com rejunte porcelanato.

8 LIMPEZA FINAL

Remova os excessos e faça a limpeza com produtos adequados.

ESPECIFICAÇÕES TÉCNICAS

- Área ideal de aplicação: Banheiros e áreas de box
- Material: Porcelanato Marmorizado
- Acabamento: Polido
- Tipo de corte: Meia Esquadria (45°)
- Profundidade interna útil: 10,0 cm
- Espessura do porcelanato: 1,2 cm
- Fixação: Argamassa ACIII ou específica para porcelanato
- Rejunte: Epóxi ou rejunte flexível
- Estilo: Minimalista e Contemporâneo
- Funcionalidade: Decoração e apoio para objetos

DESTAQUES DO PROJETO

- ★ Design sofisticado e atemporal
- ★ Acabamento em meia esquadria de alta precisão
- ★ Valoriza o ambiente e otimiza espaço
- ★ Ideal para projetos de alto padrão

SUGESTÃO DE PORCELANATOS

Mármore Calacatta Polido
120x120 cm

Mármore Statuário Polido
120x120 cm

SUGESTÃO DE METAIS E ACESSÓRIOS

Torneira Cromada

Acabamento Cromado

Saboneteira Cromada

Ducha Cromada

Porta Shampoo Cromado

SUGESTÃO DE ILUMINAÇÃO

LED Fita 3000K

Spot LED Direcionável

Luz Indireta em Nicho

PROJETO 02 — NICHO HORIZONTAL E VERTICAL INTEGRADO EM PORCELANATO MARMORIZADO COM ACABAMENTO EM MEIA ESQUADRIA ELEGÂNCIA E FUNCIONALIDADE PARA BANHEIROS COMPLETOS



PASSO A PASSO DE EXECUÇÃO

1 MARCAÇÃO DO NICHO
Marque os nichos na parede conforme medidas do projeto.

2 ABERTURA DO VÃO
Abra os vãos com serra mármore ou cortadora elétrica nas medidas corretas.

3 REGULARIZAÇÃO
Limpe o interior do vão e aplique chapisco e emboço para nivelar.

4 CORTE DAS PEÇAS
Corte as peças de porcelanato em 45° (meia esquadria) conforme medidas.

5 MONTAGEM SECA
Monte as peças dentro do vão para conferir medidas e alinhamento.

6 FIXAÇÃO
Aplique argamassa ACIII ou específica e fixe as peças começando pelo fundo.

7 ACABAMENTO
Faça o acabamento das juntas com rejunte porcelanato.

8 LIMPEZA FINAL
Remova os excessos e faça a limpeza com produtos adequados.

ESPECIFICAÇÕES TÉCNICAS

- Área ideal de aplicação: Banheiros completos (banheira e parede)
- Material: Porcelanato Marmorizado
- Acabamento: Polido
- Tipo de corte: Meia Esquadria (45°)
- Profundidade interna útil: 12,0 cm
- Espessura do porcelanato: 1,2 cm
- Fixação: Argamassa ACIII ou específica para porcelanato
- Rejunte: Epóxi ou rejunte flexível
- Estilo: Minimalista e Contemporâneo
- Funcionalidade: Organização e sofisticação com integração total

DESTAQUES DO PROJETO

- ★ Integração de nichos horizontal e vertical
- ★ Design monolítico e sofisticado
- ★ Máximo aproveitamento de espaço
- ★ Acabamento em meia esquadria de alta precisão
- ★ Ideal para projetos de alto padrão

SUGESTÃO DE PORCELANATOS

Mármore Calacatta Polido 120x120 cm

Mármore Statuário Polido 120x120 cm

SUGESTÃO DE METAIS E ACESSÓRIOS

Torneira Cromada

Acabamento Cromado

Saboneteira Cromada

Ducha Cromada

Porta Shampoo Cromado

SUGESTÃO DE ILUMINAÇÃO

LED Fita 3000K

Spot LED Direcional

Luz Indireta nos Nichos

PROJETO 03 – NICHO HORIZONTAL EM PORCELANATO MARMORIZADO COM ACABAMENTO EM MEIA ESQUADRIA

SOFISTICAÇÃO E PRATICIDADE PARA BOX DE BANHEIRO



PASSO A PASSO DE EXECUÇÃO

1. MARCAÇÃO DO NICHO

Marque o nicho na parede conforme as medidas do projeto.

2. ABERTURA DO VÃO

Abra o vão com serra mármore ou cortadora elétrica nas medidas corretas.

3. REGULARIZAÇÃO

Limpe o interior do vão e aplique chapisco e emboço para nivelar.

4. CORTE DAS PEÇAS

Corte as peças de porcelanato em 45° (meia esquadria) conforme medidas.

5. MONTAGEM SECA

Monte as peças dentro do vão para conferir medidas e alinhamento.

6. FIXAÇÃO

Aplique argamassa ACIII ou específica e fixe as peças começando pelo fundo.

7. ACABAMENTO

Faça o acabamento das juntas com rejunte porcelanato.

8. LIMPEZA FINAL

Remova os excessos e faça a limpeza com produtos adequados.

ESPECIFICAÇÕES TÉCNICAS

- Área ideal de aplicação: Box de banheiro / Chuveiro
- Material: Porcelanato Marmorizado
- Acabamento: Polido
- Tipo de corte: Meia Esquadria (45°)
- Profundidade interna útil: 10,8 cm
- Espessura do porcelanato: 1,2 cm
- Fixação: Argamassa ACIII ou específica para porcelanato
- Rejunte: Epóxi ou rejunte flexível
- Estilo: Minimalista e Contemporâneo
- Funcionalidade: Organização e sofisticação no box

DESTAQUES DO PROJETO

- ★ Visual clean e integrado ao revestimento
- ★ Acabamento em meia esquadria de alta precisão
- ★ Praticidade para armazenamento no box
- ★ Solução elegante, sem ocupar espaço físico

SUGESTÃO DE PORCELANATOS

Mármore Calacatta Polido 120x120 cm

Mármore Statuário Polido 120x120 cm

SUGESTÃO DE METAIS E ACESSÓRIOS

Ducha Preta Fosca

Misturador Preto Fosco

Registro Preto Fosco

Porta Shampoo Preto Fosco

Papeleira Preta Fosca

SUGESTÃO DE ILUMINAÇÃO



LED Fita 3000K

Spot LED Direcionável

Luz Indireta no Nicho

PROJETO 04 – NICHOS HORIZONTAIS EM PORCELANATO PRETO MARMORIZADO COM MOLDURA PRETA FOSCA E ACABAMENTO DE ALTA PRECISÃO

SOFISTICAÇÃO, CONTRASTE E FUNCIONALIDADE PARA BANHEIROS DE ALTO PADRÃO

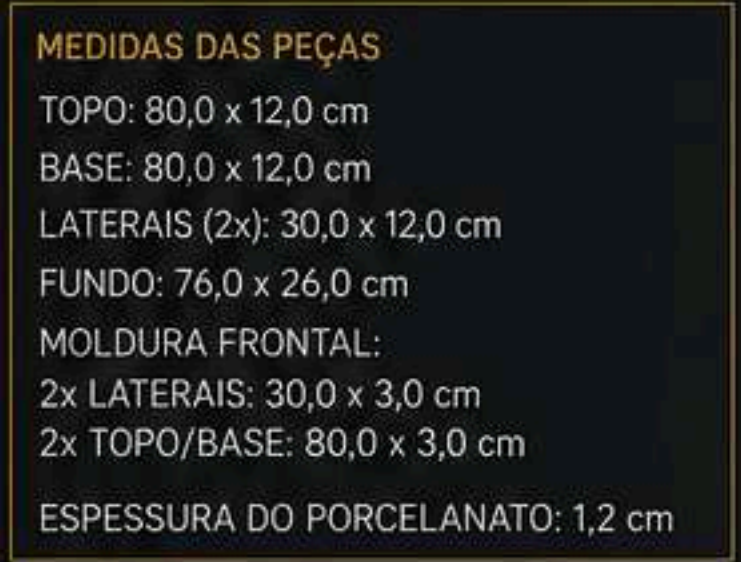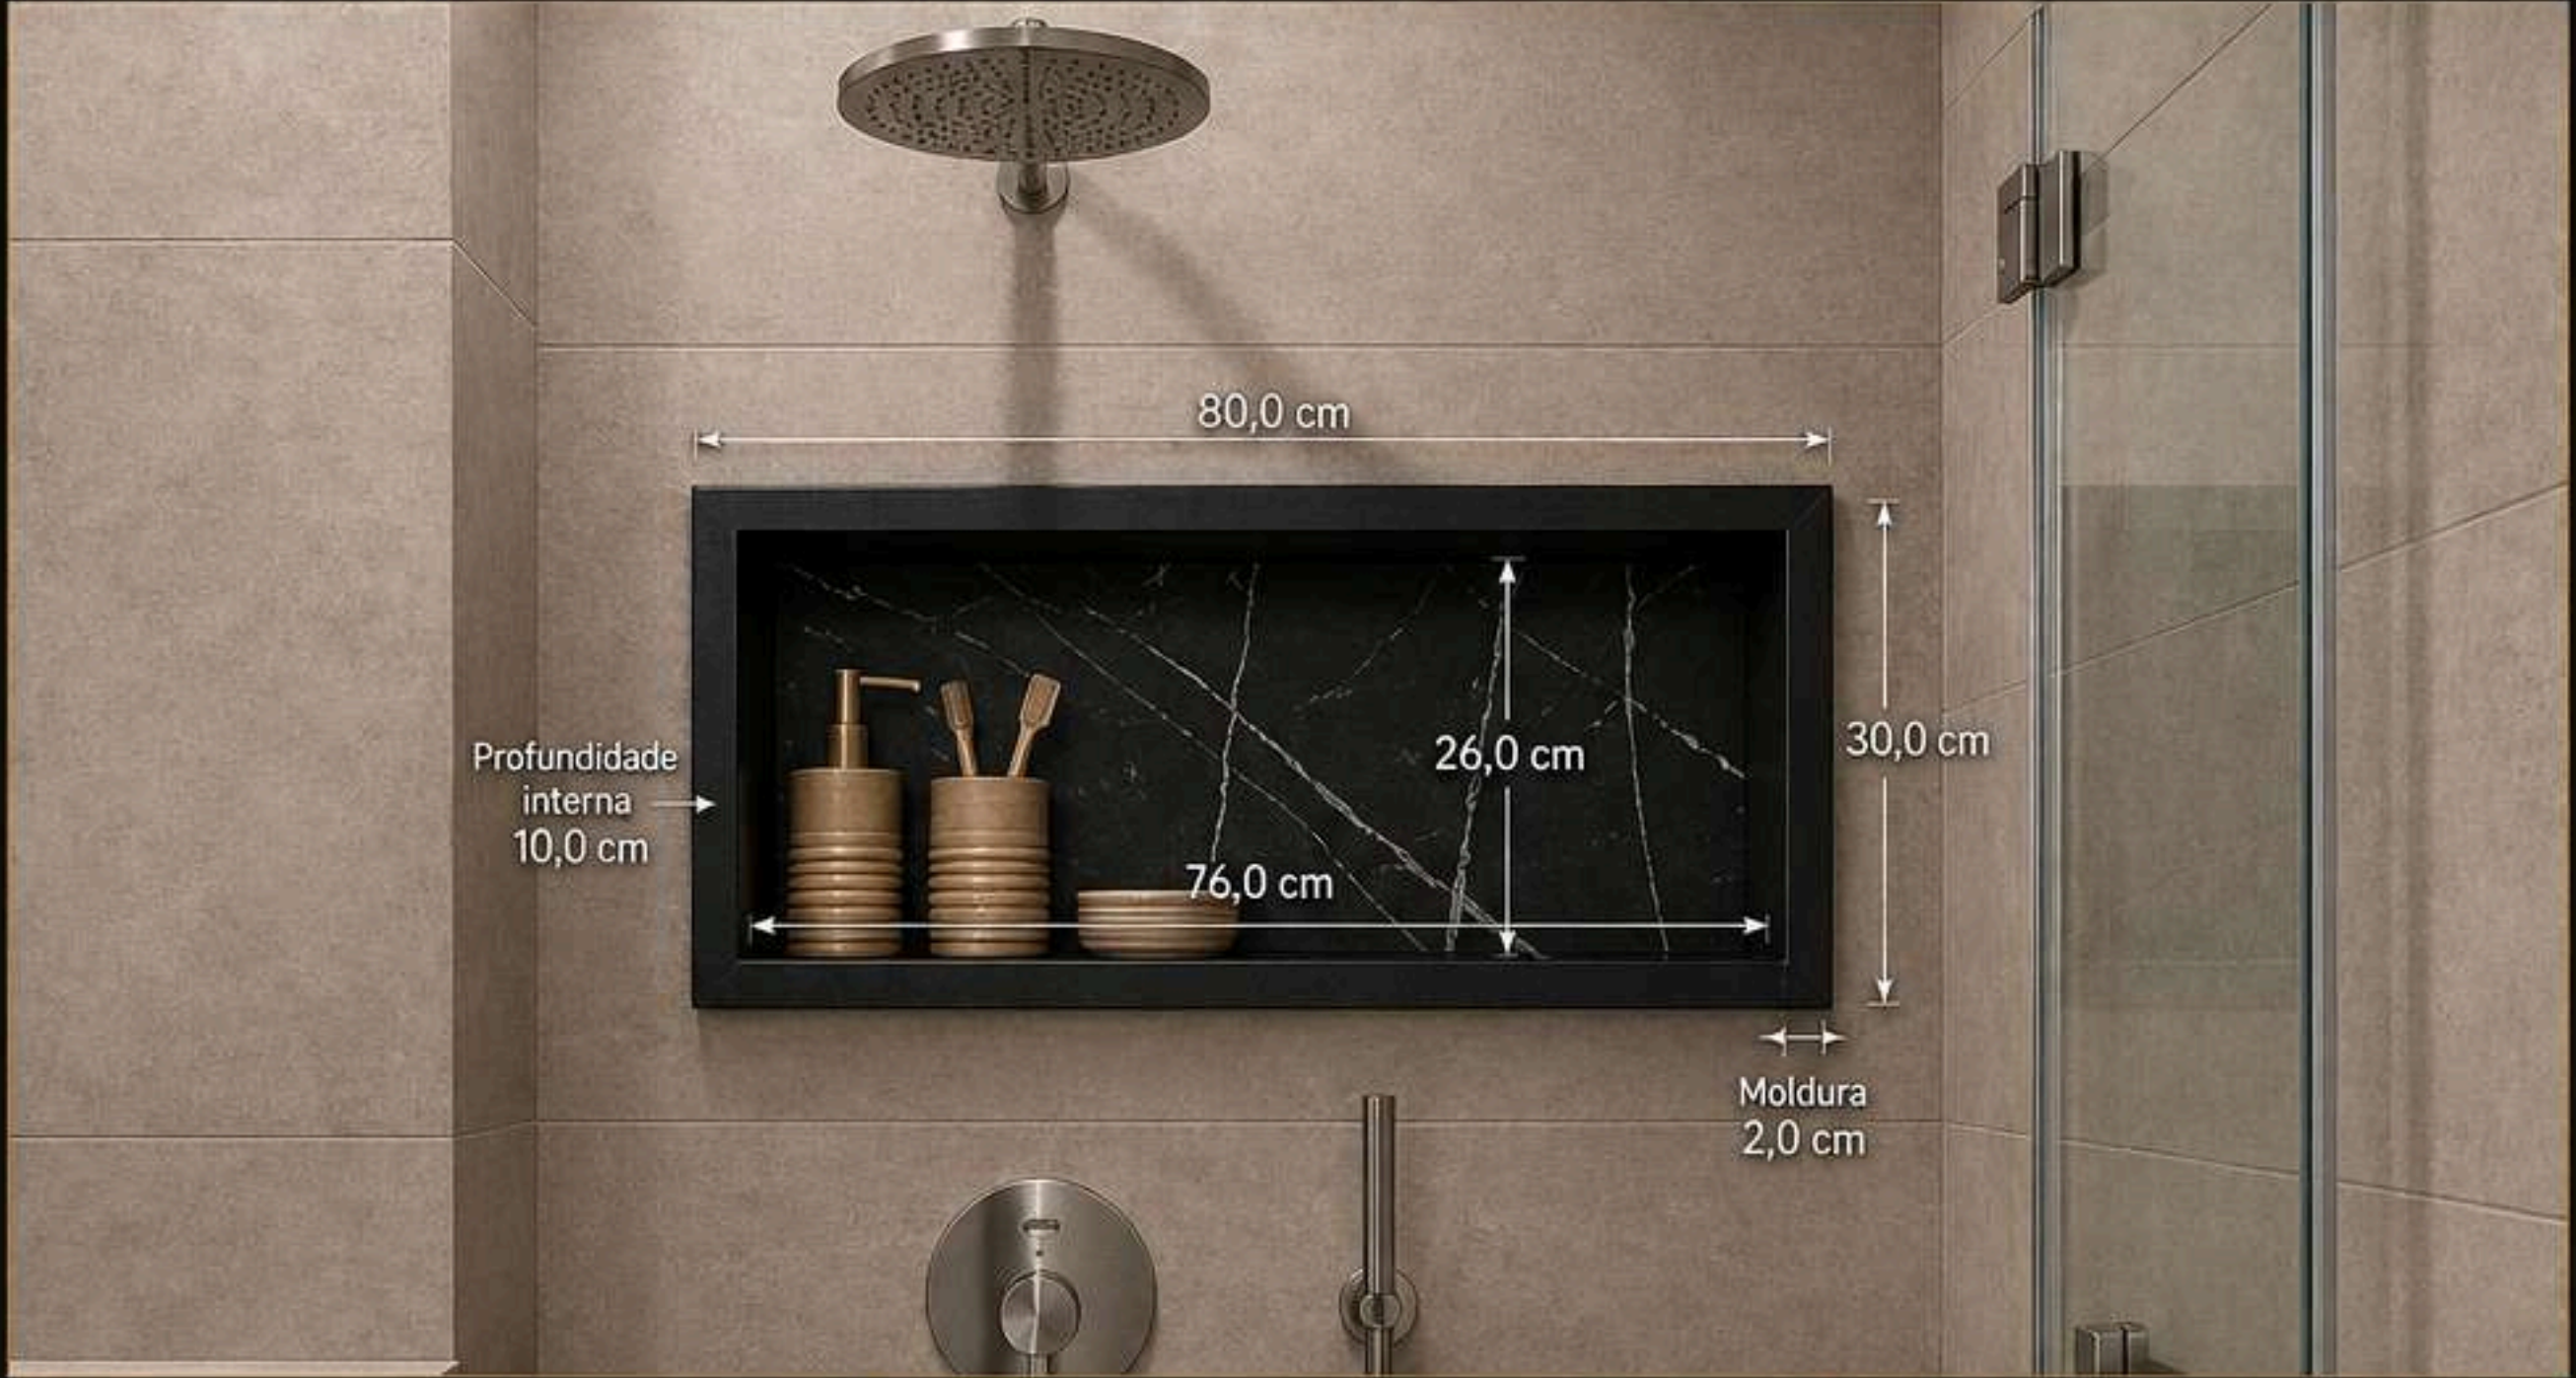

PASSO A PASSO DE EXECUÇÃO

1 MARCAÇÃO DO VÃO

Marque o nicho na parede conforme as medidas do projeto.

2 ABERTURA DO VÃO

Abra o vão com serra mármore ou cortadora elétrica nas medidas corretas.

3 REGULARIZAÇÃO

Limpe o interior do vão e aplique chapisco e emboço para nivelar.

4 CORTE DAS PEÇAS

Corte as peças de porcelanato conforme medidas (45° nas bordas da moldura).

5 MONTAGEM SECA

Monte as peças dentro do vão para conferir medidas e alinhamento.

6 FIXAÇÃO

Aplique argamassa ACIII ou específica e fixe as peças começando pelo fundo.

7 ACABAMENTO

Faça o acabamento das juntas com rejunte porcelanato preto ou cinza escuro.

8 LIMPEZA FINAL

Remova os excessos e faça a limpeza com produtos adequados.

ESPECIFICAÇÕES TÉCNICAS

- Área ideal de aplicação: Boxes de chuveiro / Banheiro principal
- Material: Porcelanato
- Acabamento moldura: Preto Fosco
- Tipo de corte: Meia Esquadria (45°)
- Profundidade interna útil: 10,0 cm
- Espessura do porcelanato: 1,2 cm
- Fixação: Argamassa ACIII ou específica para porcelanato
- Rejunte: Epóxi ou rejunte flexível
- Estilo: Contemporâneo, sofisticado e minimalista
- Funcionalidade: Organização e destaque no box

DESTAQUES DO PROJETO

- ★ Contraste elegante entre o preto e o porcelanato claro
- ★ Acabamento de altíssimo padrão e precisão
- ★ Niche funcional com grande profundidade interna
- ★ Ideal para projetos de luxo e banheiros modernos

SUGESTÃO DE PORCELANATOS

Nero Portoro Polido
120x120 cm

Manhattan Grigio
120x120 cm

SUGESTÃO DE METAIS E ACESSÓRIOS

Ducha Preta Fosca

Misturador Preto Fosco

Registro Preto Fosco

Porta Shampoo Preto Fosco

Linha Acessórios Preto Fosca

SUGESTÃO DE ILUMINAÇÃO

LED Fita 3000K

Spot LED Direcionável

Luz Indireta no Niche

PROJETO 05 – NICHO DE EMBUTIR HORIZONTAL EM PORCELANATO MARMORIZADO PRETO COM ESQUADRIA PRETO FOSCO E ACABAMENTO REFINADO

SOFISTICAÇÃO, CONTRASTE E FUNCIONALIDADE PARA BANHEIROS PREMIUM



MEDIDAS DAS PEÇAS

TOPO:	80,0 x 12,0 cm
BASE:	80,0 x 12,0 cm
LATERAIS (2x):	30,0 x 12,0 cm
FUNDO:	76,0 x 26,0 cm
MOLDURA FRONTAL:	
2x LATERAIS:	30,0 x 3,0 cm
2x TOPO/BASE:	80,0 x 3,0 cm
ESPESSURA DO PORCELANATO:	1,2 cm

PASSO A PASSO DE EXECUÇÃO

1 MARCAÇÃO DO VÃO
Marque o nicho na parede conforme as medidas do projeto.

2 ABERTURA DO VÃO
Abra o vão com serra mármore ou cortadora elétrica nas medidas corretas.

3 REGULARIZAÇÃO
Limpe o interior do vão e aplique chapisco e emboço para nivelar.

4 CORTE DAS PEÇAS
Corte as peças de porcelanato em 45° (meia esquadria) conforme medidas.

5 MONTAGEM SECA
Monte as peças dentro do vão para conferir medidas e alinhamento.

6 FIXAÇÃO
Aplique argamassa ACIII ou específica e fixe as peças começando pelo fundo.

7 ACABAMENTO
Faça o acabamento das juntas com rejunte porcelanato.

8 LIMPEZA FINAL
Remova os excessos e faça a limpeza com produtos adequados.

ESPECIFICAÇÕES TÉCNICAS

- Área ideal de aplicação: Boxes de banheiro / Banheiro principal
- Material: Porcelanato Marmorizado
- Acabamento moldura: Preto Fosco
- Tipo de corte: Meia Esquadria (45°)
- Profundidade interna útil: 10,0 cm
- Espessura do porcelanato: 1,2 cm
- Fixação: Argamassa ACIII ou específica para porcelanato
- Rejunte: Epóxi ou rejunte flexível
- Estilo: Contemporâneo, sofisticado e minimalista
- Funcionalidade: Organização e destaque no box

DESTAQUES DO PROJETO

- ★ Contraste elegante entre o preto e o porcelanato claro/bege
- ★ Acabamento de alto padrão e visual sofisticado
- ★ Nicho funcional com grande profundidade interna
- ★ Ideal para projetos de luxo e banheiros modernos

SUGESTÃO DE PORCELANATOS

SUGESTÃO DE METAIS E ACESSÓRIOS

SUGESTÃO DE ILUMINAÇÃO

PROJETO 08

BANCADA SUSPensa EM PORCELANATO MARMORIZADO COM NICH0 EMBUTIDO E CUBA DE SOBREP0R TEXTURIZADA



ESPECIFICAÇÕES TÉCNICAS DO PROJETO

Estilo do Projeto
Minimalista Contemporâneo com Toques Orgânicos

Tipo de Porcelanato
Porcelanato Marmorizado Travertino (Creme/Bege)


Técnica de Corte
Execução em Meia Esquadria (45°) para bancadas e nicho

Aplicação
Bancada, Prateleira e Nicho de Banheiro


MATERIAIS E ACABAMENTOS

- Porcelanato Travertino Creme/Bege – Acetinado
- Cuba de sobrepor texturizada retangular com cantos arredondados
- Torneira preta fosca de mesa
- LED 3000K embutido no nicho e atrás do espelho
- Espelho redondo lapidado com LED perimetral
- Acabamento minimalista com juntas invisíveis

PLANTA BAIXA ESCALA 1:20

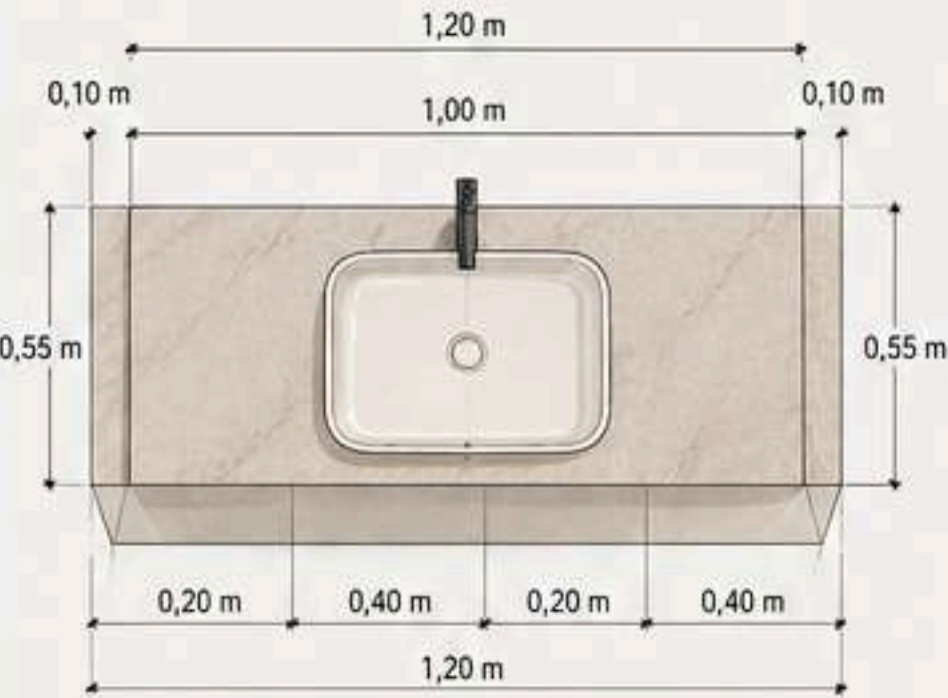


VISTA FRONTAL ESCALA 1:20

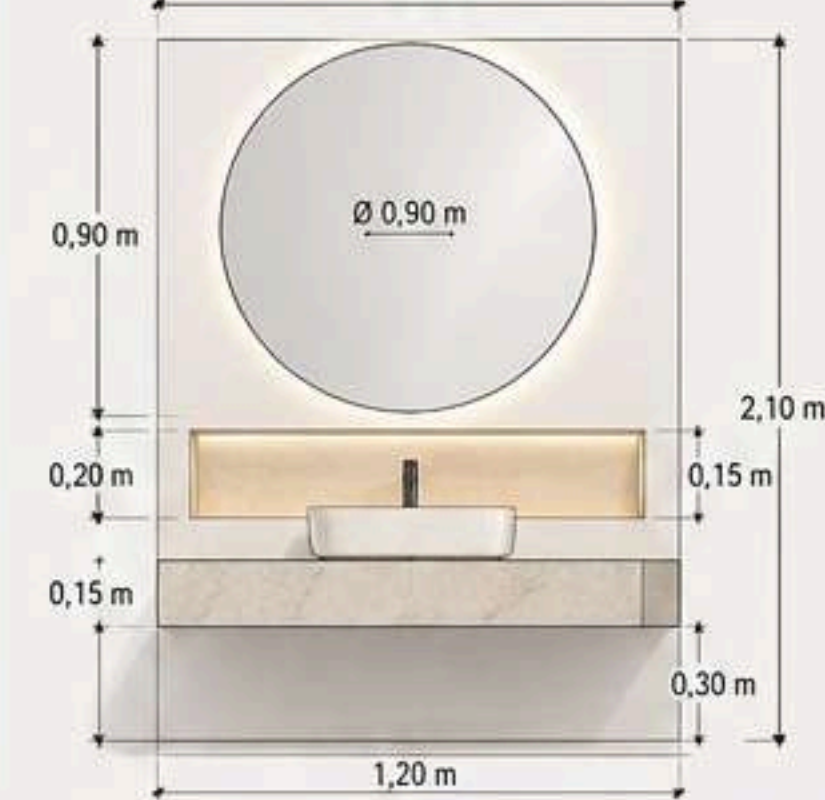

VISTA LATERAL ESCALA 1:20



DETALHE BANCADA ESCALA 1:10

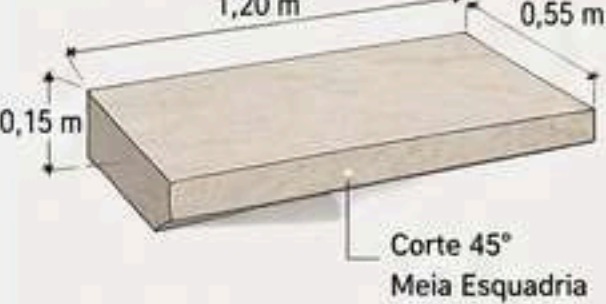


DETALHE NICH0 ESCALA 1:10



DETALHE CUBA ESCALA 1:10



CORTE LATEL (BANCADA) ESCALA 1:10

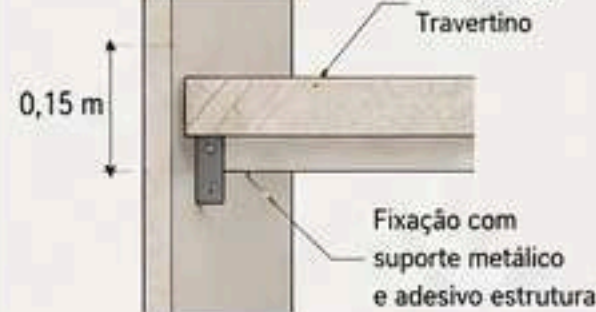


MEDIDAS E DISTÂNCIAS TÉCNICAS

- Altura do piso até o topo da bancada: 0,90 m
- Altura livre abaixo da bancada: 0,30 m
- Altura do nicho: 0,15 m
- Profundidade do nicho: 0,12 m
- Altura do espelho a partir do topo da bancada: 0,15 m (início do espelho)
- Diâmetro do espelho: 0,90 m
- Largura da bancada: 1,20 m
- Profundidade da bancada: 0,55 m
- Espessura da bancada: 0,15 m

SUGESTÃO DE METAIS E ACESSÓRIOS



ILUMINAÇÃO

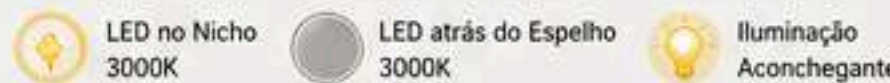

PASSO A PASSO DE EXECUÇÃO

- Marcação do local da bancada, nicho e pontos hidráulicos.
- Execução do nicho embutido na parede, com esquadros perfeitos e impermeabilização.
- Instalação da iluminação LED dentro do nicho e teste.
- Corte das peças de porcelanato em meia esquadria (45°) para a bancada e nicho.
- Colagem da bancada com adesivo estrutural e suporte metálico até a cura.
- Acabamento das juntas invisíveis e polimento.
- Instalação da cuba, torneira, sifão e acessórios.
- Limpeza final e vedação das juntas com silicone neutro.

POR QUE ESTE PROJETO VALORIZA O AMBIENTE?

A bancada suspensa em porcelanato marmorizado traz leveza e sofisticação ao ambiente, valorizando o design minimalista. O nicho com iluminação LED oferece funcionalidade e aconchego, enquanto a cuba de sobrepor texturizada agrega elegância e personalidade ao projeto.

PROJETO 09

BANCADA E NICHOS FLUTUANTES EM PORCELANATO CALACATTA COM ESPELHO LED



ESPECIFICAÇÕES TÉCNICAS DO PROJETO

Estilo do Projeto
Minimalista Industrial
Contemporâneo, Escultural

Tipo de Porcelanato
Porcelanato Marmorizado
Alto Brilho (Calacatta) e
Cimento Texturizado
(Paredes/Piso)


Técnica de Corte
Execução em Meia Esquadria
(45°) e Corte Retificado

Aplicação
Área do Lavabo e Banheiro
(Bancada, Nichos,
Revestimento Total)


MATERIAIS E ACABAMENTOS

- Porcelanato Calacatta Polido (Alta Brilho) – Bancada e Prateleira
- Revestimento Cimento Texturizado Cinza – Paredes e Piso
- Torneira de Mesa Preta Fosca
- Cuba Esculpida Integrada
- Espelho Retangular com LED Perimetral (Luz Fria 4000K)
- Nichos com Iluminação LED Embutida 3000K
- Acabamento minimalista com juntas invisíveis


PLANTA BAIXA
ESCALA 1:20

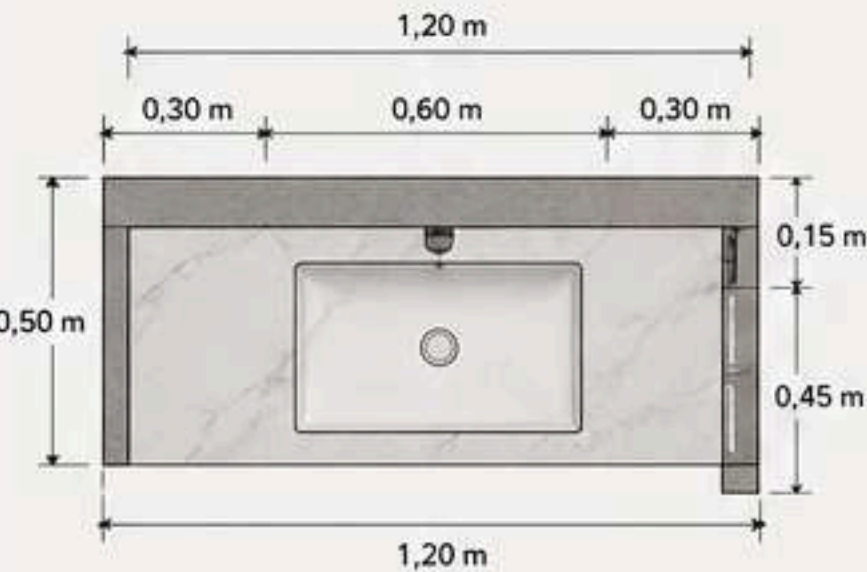


VISTA FRONTAL
ESCALA 1:20

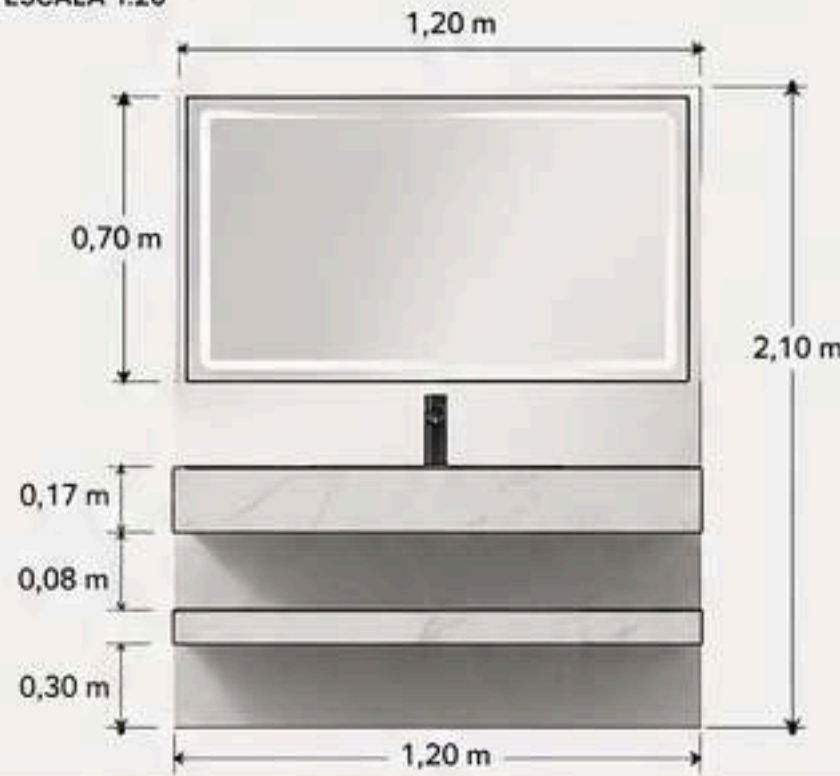


VISTA LATERAL
ESCALA 1:20

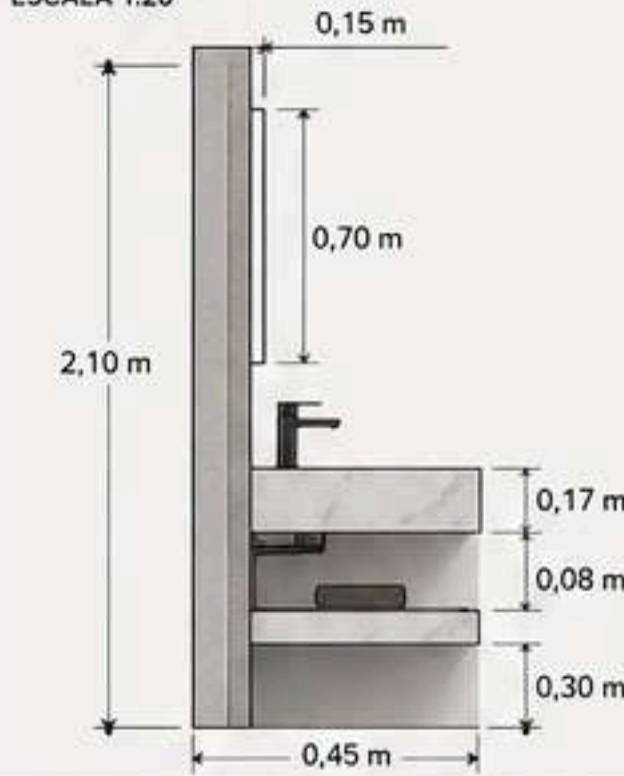

DETALHE BANCADA (CORTE)
ESCALA 1:10

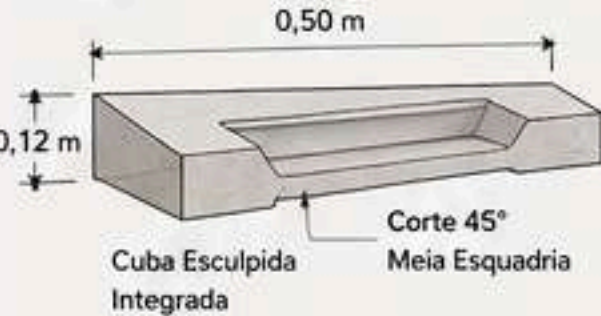


DETALHE PRATELEIRA INFERIOR
ESCALA 1:10

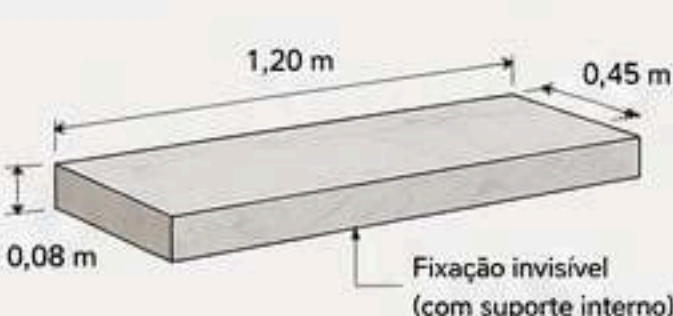

DETALHE NICHOS
ESCALA 1:10



PASSO A PASSO DE EXECUÇÃO
ESCALA 1:10

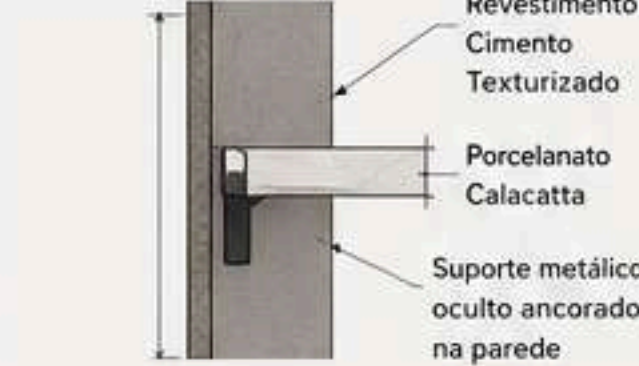


MEDIDAS E DISTÂNCIAS TÉCNICAS

- Altura do piso até o topo da bancada: 0,85 m
- Altura livre abaixo da bancada (até a prateleira): 0,17 m
- Altura entre prateleira e piso: 0,30 m
- Profundidade da bancada: 0,50 m
- Profundidade da prateleira: 0,45 m
- Espessura da bancada: 0,12 m
- Espessura da prateleira: 0,08 m
- Largura total da bancada e prateleira: 1,20 m
- Altura do espelho: 0,70 m (instalado a partir de 1,15 m do piso)
- Profundidade dos nichos: 0,15 m
- Altura de cada nicho: 0,30 m (x3)

SUGESTÃO DE METAIS E ACESSÓRIOS



ILUMINAÇÃO

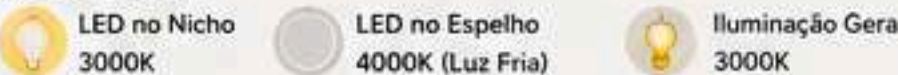

PASSO A PASSO DE EXECUÇÃO

- 1 Marcação precisa das medidas e pontos hidráulicos.
- 2 Fixação dos suportes metálicos na parede (nível e prumo).
- 3 Instalação da bancada com corte em meia esquadria.
- 4 Conexão hidráulica e vedação da cuba integrada.
- 5 Fixação da prateleira inferior com suportes ocultos.
- 6 Execução dos nichos, impermeabilização e acabamento.
- 7 Instalação da iluminação LED nos nichos e espelho.
- 8 Acabamentos finais e limpeza das juntas com silicone neutro.



POR QUE ESTE PROJETO VALORIZA O AMBIENTE?

A combinação do porcelanato Calacatta com o cimento texturizado cria um contraste sofisticado e atual. O espelho LED e os nichos iluminados trazem funcionalidade e elegância, enquanto o design flutuante amplia o espaço e facilita a limpeza, proporcionando um ambiente moderno e de alto padrão.

PROJETO 10

LAVABO DE LUXO COM BANCADAS FLUTUANTES EM PORCELANATO DRAMÁTICO



ESPECIFICAÇÕES TÉCNICAS DO PROJETO

Estilo do Projeto
Minimalista de Luxo Contemporâneo

Tipo de Porcelanato
Porcelanato Marmorizado de Grande Formato (Calacatta Oro e Preto Veado)

Técnica de Corte
Execução em Meia Esquadria (45°) e Corte Retificado de Alta Precisão


Aplicação
Bancadas de Lavabo Flutuantes e Revestimento de Parede Integrado

MATERIAIS E ACABAMENTOS

- Porcelanato Calacatta Oro Polido (Bancada da direita)
- Porcelanato Preto Veado Polido (Bancada da esquerda e paredes)
- Torneira de Mesa Bica Alta Dourada (Lavabo da direita)
- Torneira de Mesa Bica Alta Cromada (Lavabo da esquerda)
- Espelho Redondo com LED Perimetral
- Espelho Retangular com LED Perimetral
- Iluminação LED 3000K no nicho e abaixo da prateleira
- Acabamento minimalista com elementos flutuantes


PLANTA BAIXA

ESCALA 1:20

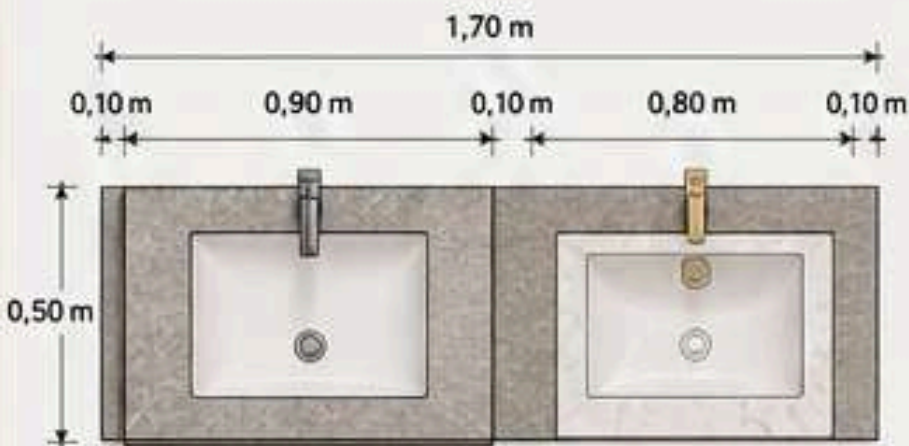


VISTA FRONTAL

ESCALA 1:20

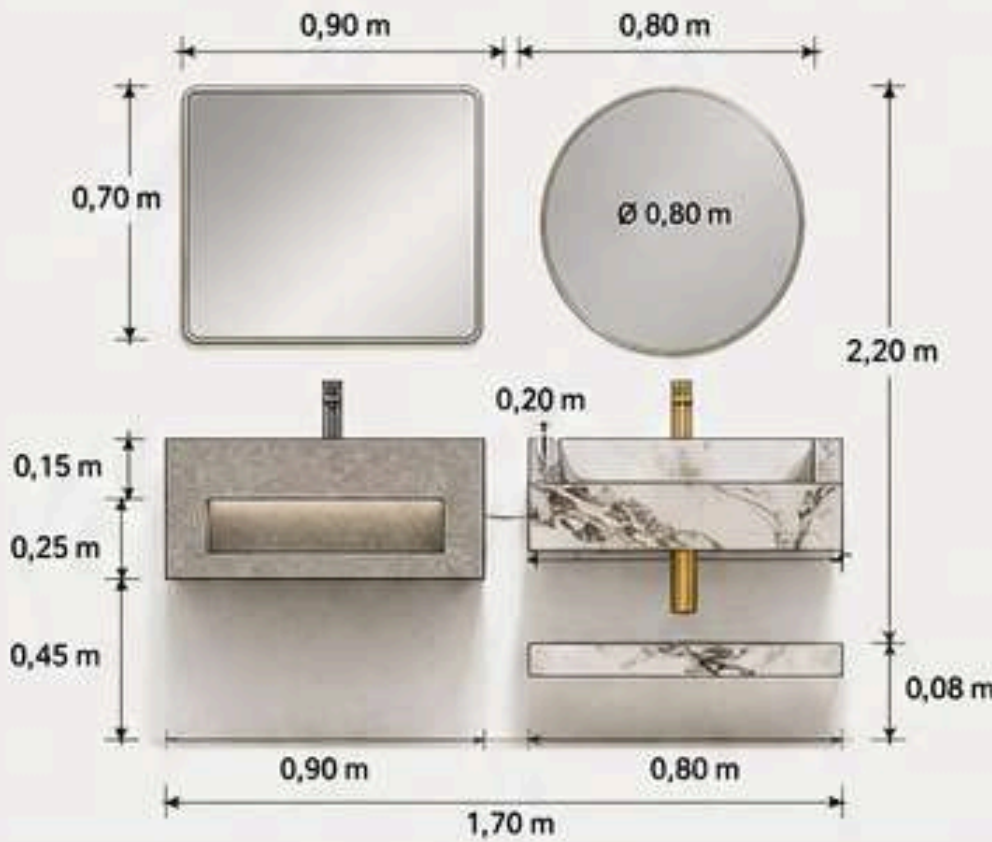

VISTA LATERAL

ESCALA 1:20

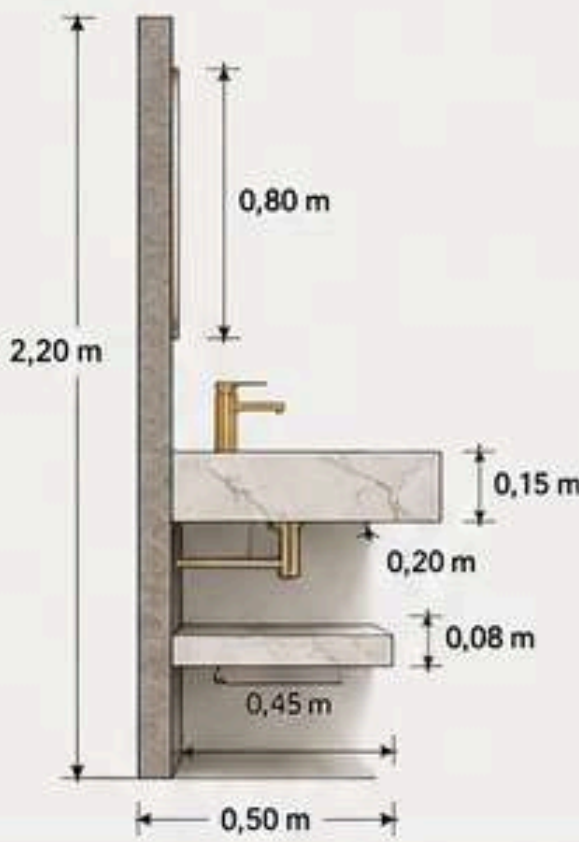

DETALHE BANCADA ESQUERDA

ESCALA 1:10



DETALHE BANCADA DIREITA

ESCALA 1:10




DETALHE PRATELEIRA INFERIOR

ESCALA 1:10



PARTE A PARTE (BAECUÃS)

ESCALA 1:10

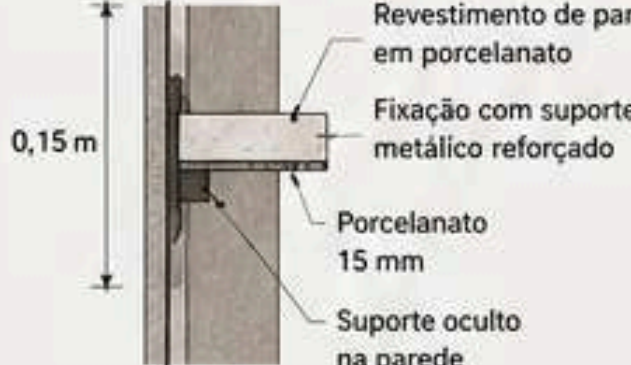


MEDIDAS E DISTÂNCIAS TÉCNICAS

- Altura do piso até o topo da bancada: 0,90 m
- Altura livre abaixo da bancada: 0,20 m (direita) / 0,25 m (esquerda)
- Profundidade das bancadas: 0,50 m
- Espessura das bancadas: 0,15 m
- Prateleira inferior: profundidade 0,45 m / espessura 0,08 m
- Altura da prateleira inferior até o piso: 0,45 m
- Altura do espelho redondo: centro a 1,60 m do piso
- Altura do espelho retangular: base a 1,50 m do piso
- Distância entre as bancadas: 0,10 m
- Largura total do conjunto: 1,70 m

SUGESTÃO DE METAIS E ACESSÓRIOS



ILUMINAÇÃO

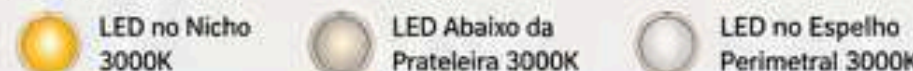

PASSO A PASSO DE EXECUÇÃO

- 1 Marcação precisa das medidas e pontos hidráulicos.
- 2 Instalação dos suportes metálicos reforçados na parede.
- 3 Corte das peças em meia esquadria (45°) com alto padrão.
- 4 Assentamento e fixação das bancadas flutuantes.
- 5 Instalação da prateleira inferior com suporte oculto.
- 6 Execução dos nichos e passagem de fiação.
- 7 Instalação da iluminação LED no nicho, prateleira e espelhos.
- 8 Instalação das cubas esculpidas e metais.
- 9 Acabamentos finais, vedação das juntas com silicone neutro e limpeza.

PROJETO 11

BANCADA ESCULPIDA MONOBLOCO E PRATELEIRA SUSPensa EM PORCELANATO CALACATTA



ESPECIFICAÇÕES TÉCNICAS DO PROJETO

Estilo do Projeto
Minimalista Luxuoso, Escultural

Tipo de Porcelanato
Porcelanato Marmorizado de Alto Brilho (Calacatta Gold)

Técnica de Corte
Execução em Monobloco (Esculpida com Meia Esquadria (45°))


Aplicação
Lavabo de Alto Padrão (Área Seca)

MATERIAIS E ACABAMENTOS

- Porcelanato Calacatta Gold Polido (Alta Qualidade)
- Torneira de Mesa Bica Alta Cromada
- Válvula Click Cromada
- Acabamento de registro cromado
- Rejunte epóxi na cor do porcelanato
- Silicone neutro transparente
- Suportes metálicos ocultos
- Niveladores e adesivo de alta aderência para porcelanato


PLANTA BAIXA

ESCALA 1:10

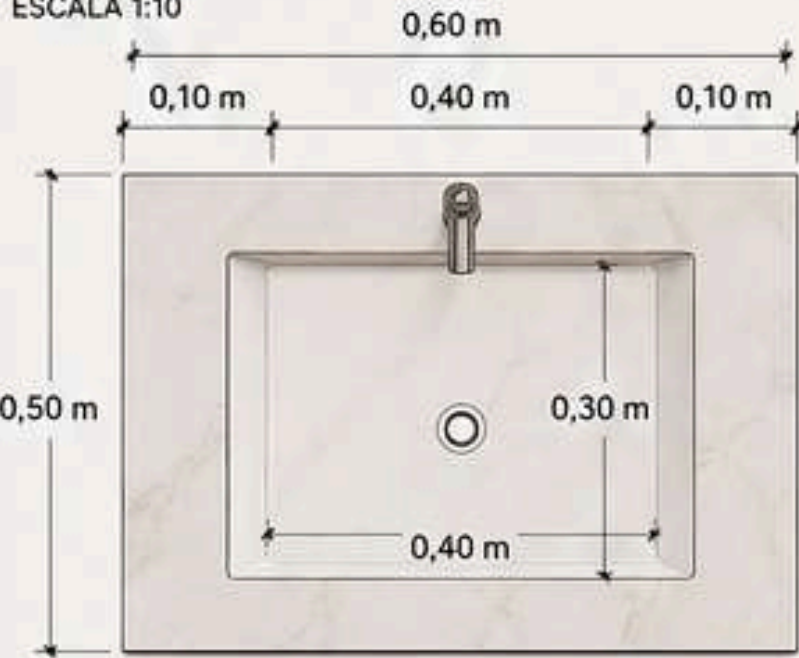


VISTA FRONTAL

ESCALA 1:10

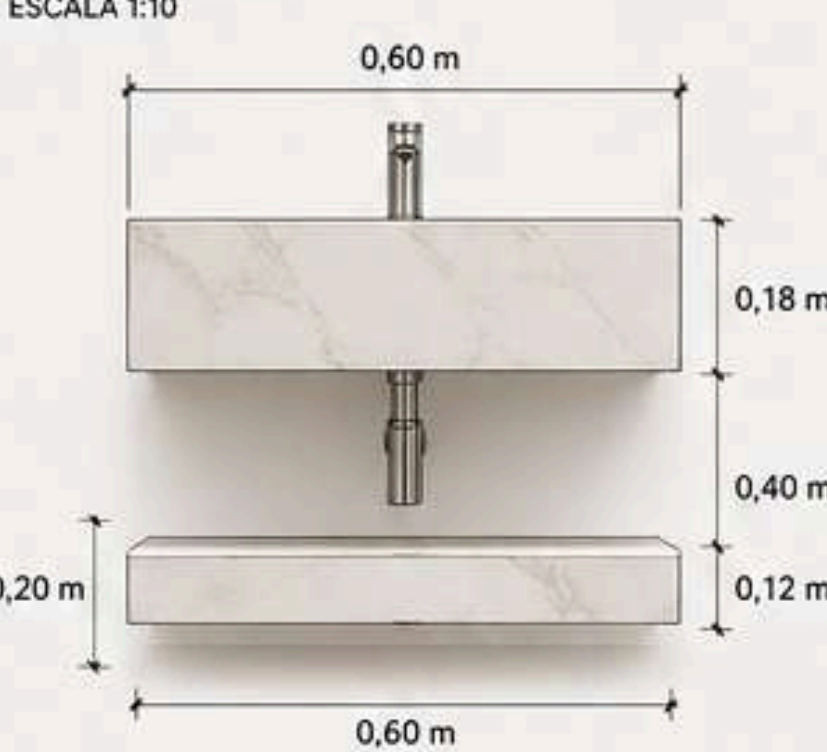

VISTA LATERAL

ESCALA 1:10

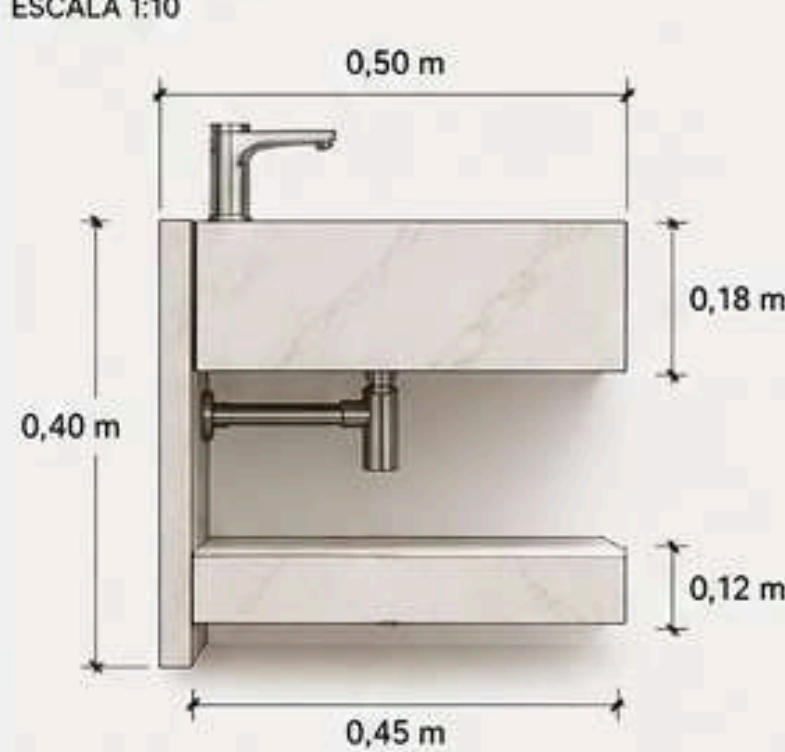

DETALHE BANCADA (MONOBLOCO)

ESCALA 1:5




DETALHE PRATELEIRA SUSPensa

ESCALA 1:5




DETALHE CORTE (MEIA ESQUADRIA)

ESCALA 1:5

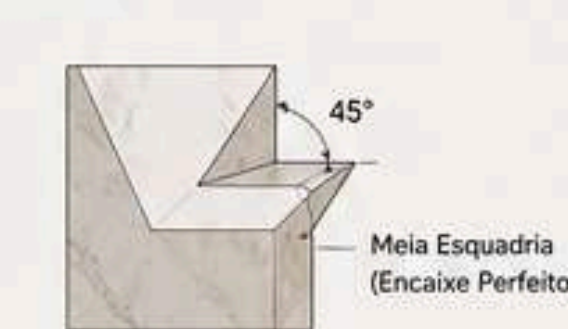

FIXAÇÃO E SUPORTE

ESCALA 1:5

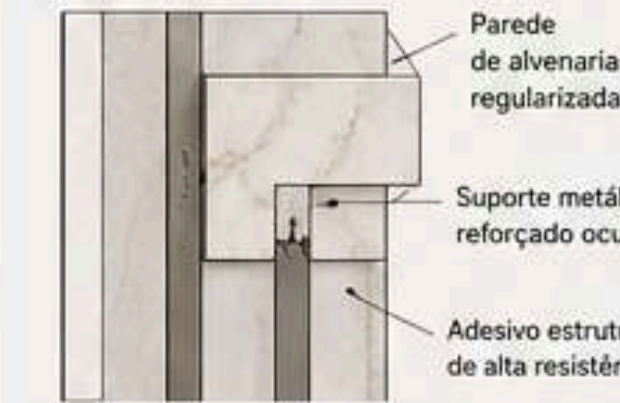

MEDIDAS E DISTÂNCIAS TÉCNICAS

- Altura do piso até o topo da bancada: 0,90 m
- Profundidade da bancada: 0,50 m
- Largura da bancada: 0,60 m
- Espessura da bancada (monobloco): 0,18 m
- Profundidade da cuba esculpida: 0,12 m
- Distância da prateleira ao piso: 0,20 m
- Espessura da prateleira: 0,12 m
- Profundidade da prateleira: 0,45 m
- Largura da prateleira: 0,60 m
- Altura entre bancada e prateleira: 0,20 m

SUGESTÃO DE METAIS E ACESSÓRIOS



ILUMINAÇÃO



PASSO A PASSO DE EXECUÇÃO

- 1 Marcação precisa das medidas e pontos hidráulicos.
- 2 Regularização da parede para fixação dos suportes.
- 3 Fixação dos suportes metálicos nivelados.
- 4 Corte do porcelanato em meia esquadria (45°).
- 5 Colagem da bancada monobloco com adesivo estrutural e fixação nos suportes.
- 6 Instalação da prateleira suspensa no suporte inferior.
- 7 Instalação da cuba esculpida e conexão hidráulica.
- 8 Acabamentos, rejunte e vedação com silicone neutro.
- 9 Limpeza final e conferência de nivelamento.

BANCADA ESCULPIDA MONOBLOCO E PRATELEIRA SUSPensa EM PORCELANATO CALACATTA



MEDIDAS TÉCNICAS DO PROJETO

Largura da bancada:	0,90 m
Profundidade da bancada:	0,50 m
Altura da bancada:	0,15 m
Espessura das bordas:	0,06 m
Cuba interna (L x P x A):	0,50 x 0,30 x 0,10 m
Altura do piso até topo:	0,90 m
Distância bancada/prateleira:	0,22 m
Prateleira (L x P x E):	0,90 x 0,35 x 0,06 m
Altura da prateleira do piso:	0,45 m
Iluminação LED:	3000K (luz quente)

ESPECIFICAÇÕES TÉCNICAS DO PROJETO

Estilo do Projeto	Minimalista, Luxuoso, Escultural
Tipo de Porcelanato	Marmorizado Alto Brilho (Calacatta Gold)
Técnica de Corte	Execução em monobloco (esculpido) com meia esquadria (45°)
Aplicação	Lavabo de Alto Padrão (Área Seca)

ANÁLISE DE DESIGN E FUNCIONALIDADE


- Contraste sofisticado:** A bancada monobloco cria um visual contínuo e limpo, enquanto a prateleira inferior adiciona leveza.
- Funcionalidade inteligente:** Estrutura suspensa facilita limpeza e amplia a sensação de espaço.
- Valorização estética:** Continuidade dos veios do porcelanato reforça o aspecto premium.

PASSO A PASSO DO PROJETO

1 PLANEJAMENTO Definir medidas e paginação dos veios, marcar pontos hidráulicos e verificar nível da parede.	2 CORTE DO PORCELANATO Cortes em 45° (meia esquadria) e separar peças: base, laterais, fundo e cuba.	3 EXECUÇÃO DA CUBA ESCULPIDA Montagem interna com caimento, furação para ralo, vedação e acabamento.	4 MONTAGEM DO MONOBLOCO Colagem das peças externas, alinhamento dos veios e reforço estrutural interno.	5 INSTALAÇÃO DA BANCADA Fixação com estrutura metálica oculta, nivelamento preciso e instalação da torneira e sifão.	6 INSTALAÇÃO DA PRATELEIRA Suporte invisível embutido e alinhamento perfeito com a bancada.	7 ILUMINAÇÃO E ACABAMENTO Instalar fita LED, aplicar silicone neutro e limpeza e polimento final.
---	---	---	--	---	--	--

DETALHES TÉCNICOS E VISTAS

- Iluminação indireta cria efeito flutuante e sensação de leveza.
- Corte em meia esquadria elimina emendas visíveis e aumenta o padrão.
- Fixação oculta aumenta o nível de acabamento e sofisticação.

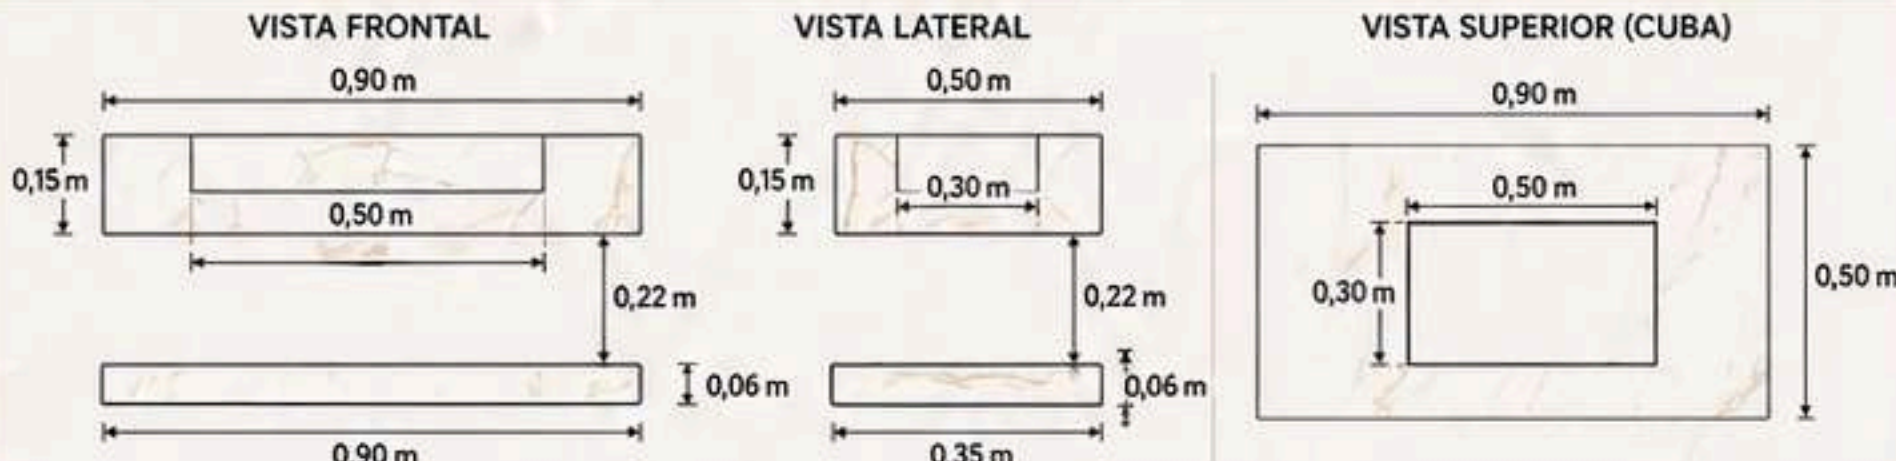

POR QUE ESTE PROJETO VALORIZA O SERVIÇO?

- Estética monolítica:** aparência de peça única esculpida.
- Execução técnica avançada:** exige precisão e experiência.
- Alto valor percebido:** cliente enxerga luxo e exclusividade.

OBSERVAÇÕES PROFISSIONAIS


Tolerância de execução: ± 2 mm

Utilizar cola específica para porcelanato.

Reforço interno é obrigatório.

Conferir esquadro antes da colagem.

ARQUITETURA
DE VALOR

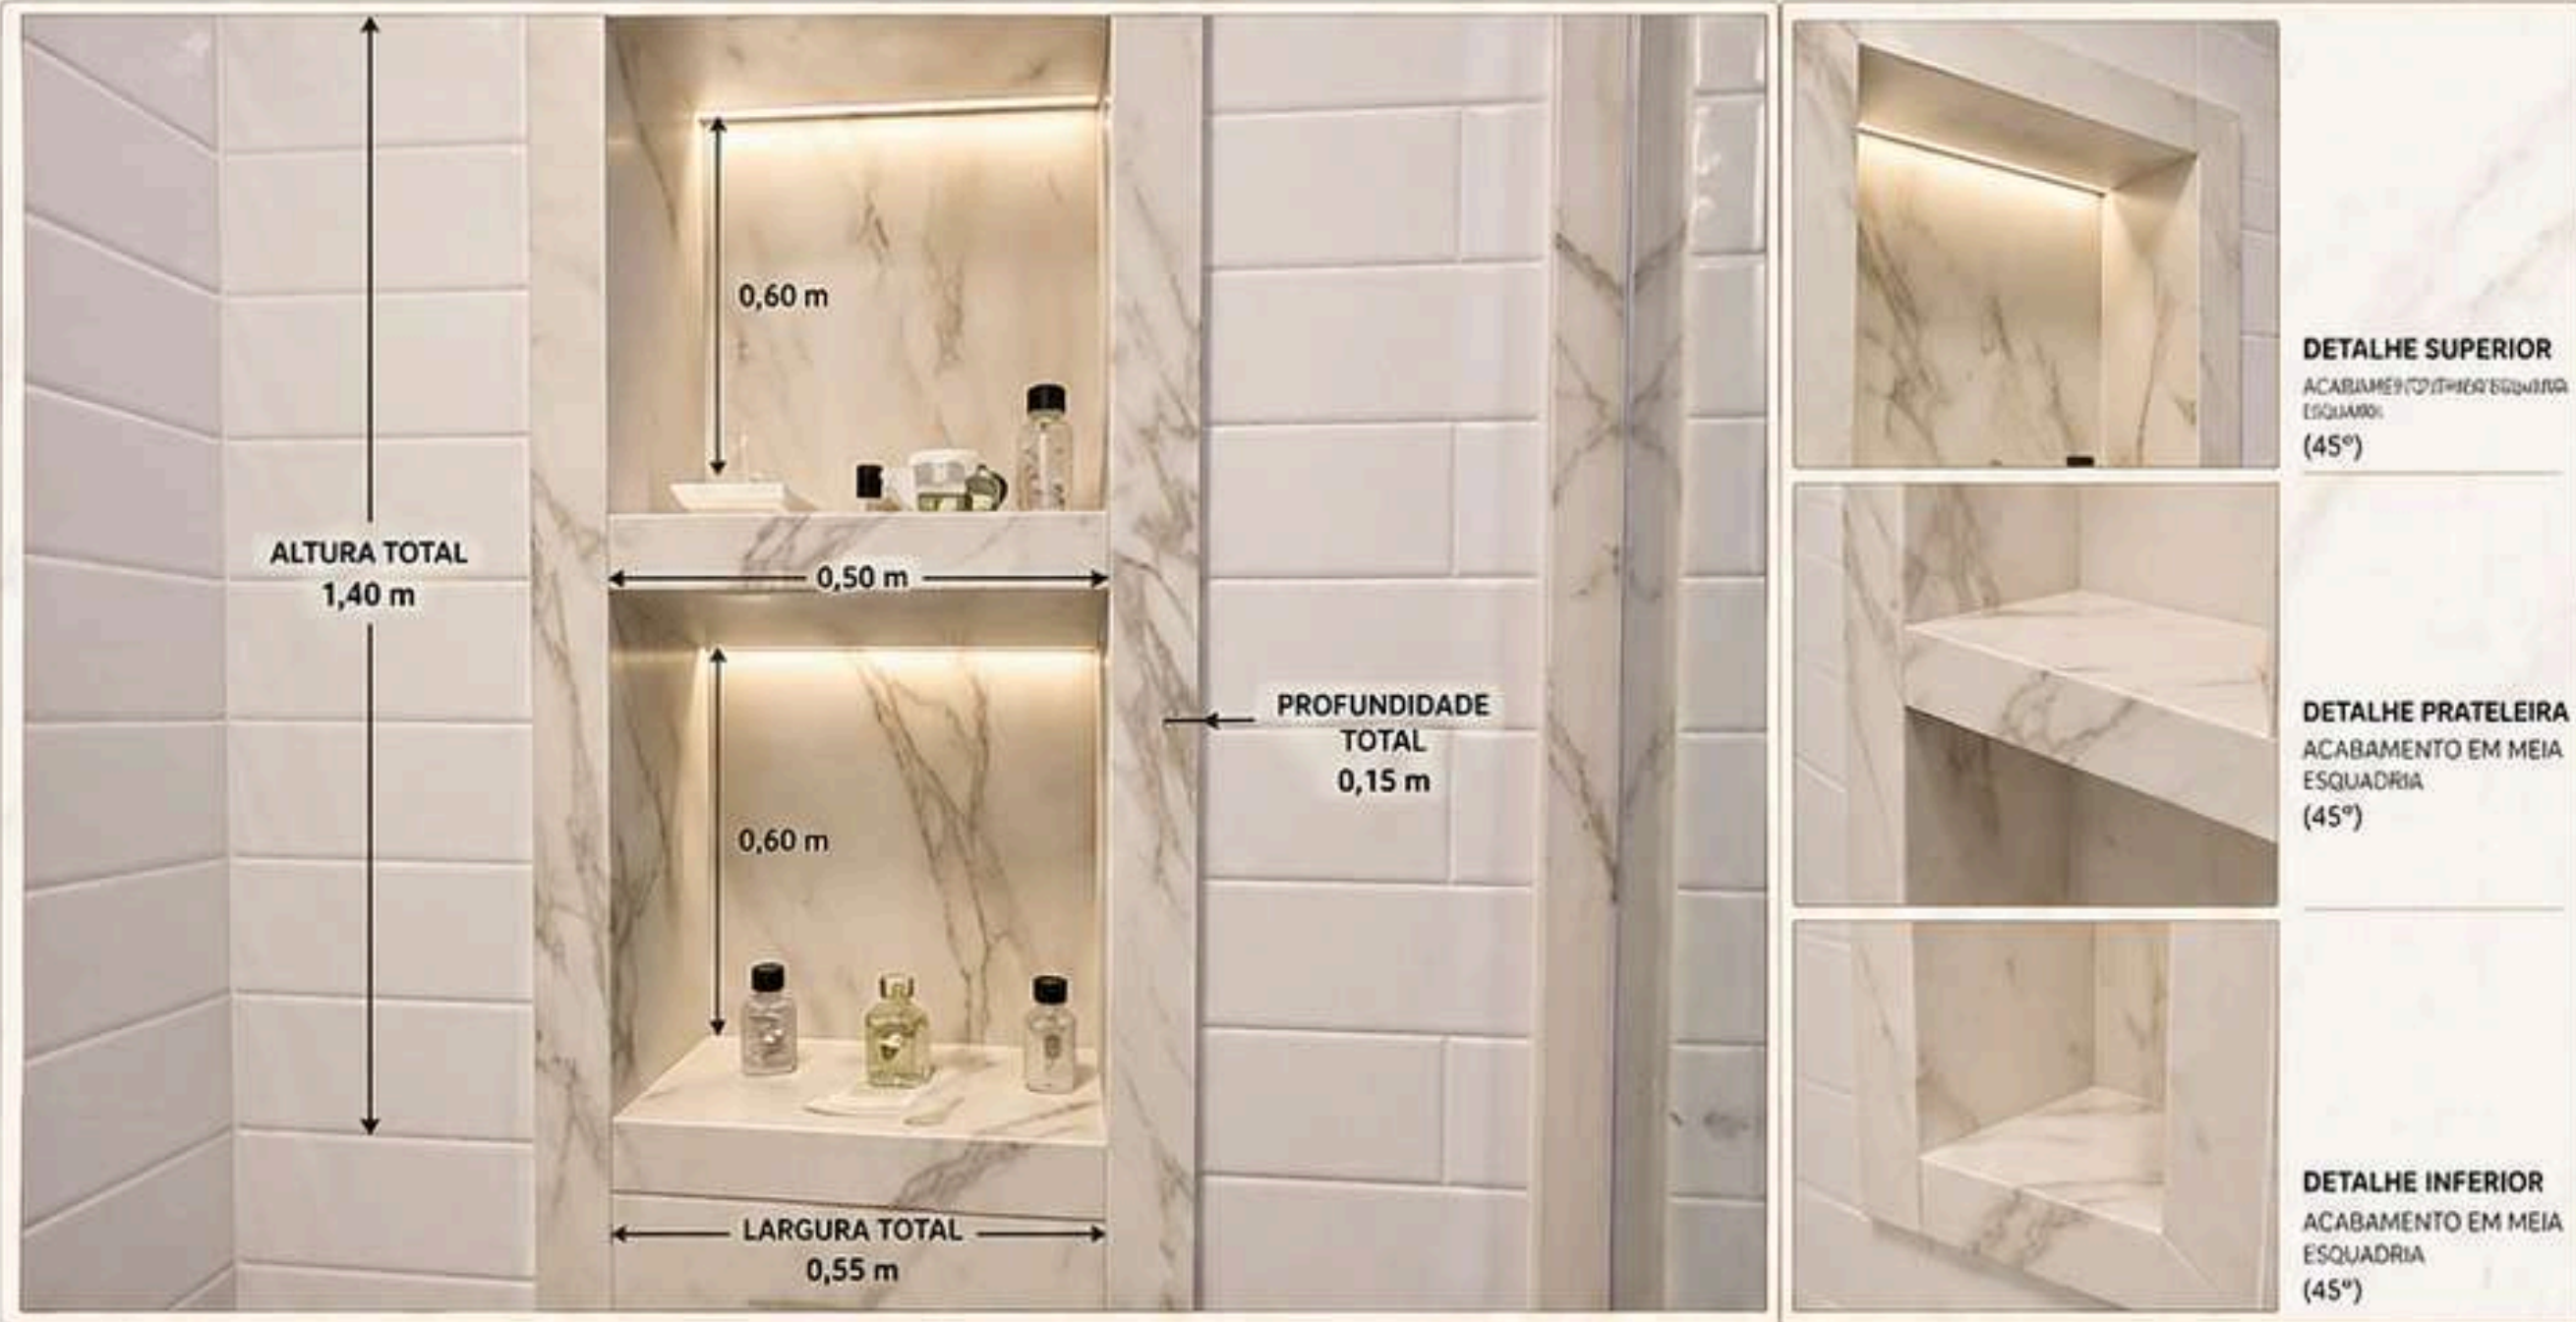NICHU VERTICAL ALTO EM PORCELANATO MARMORIZADO
COM ACABAMENTO EM MEIA ESQUADRIA

MEDIDAS TÉCNICAS DO PROJETO

Altura total do nicho:	1,40 m
Largura total do nicho:	0,55 m
Profundidade total do nicho:	0,15 m
Largura interna do nicho:	0,50 m
Altura de cada vão interno:	0,60 m
Profundidade interna:	0,13 m
Espessura das prateleiras (frente):	0,05 m
Espessura das laterais (moldura):	0,05 m
Distância entre prateleiras:	0,02 m
Iluminação LED:	3000K (luz quente)

ESPECIFICAÇÕES TÉCNICAS DO PROJETO

Estilo do Projeto	Minimalista Contemporâneo, Sofisticado
Tipo de Porcelanato	Porcelanato Marmorizado Polido (Statuario/Calacatta)
Técnica de Corte	Execução em Meia Esquadria (45°)
Aplicação	Área de Box (Banheiro)

ANÁLISE DE DESIGN E FUNCIONALIDADE

- Destaque do Projeto:** Nicho vertical alto e embutido em porcelanato marmorizado, criando um elemento escultural e funcional.
- Sugestão de Aplicação para Clientes:** Perfeito para áreas de box compactas, maximizando o armazenamento sem comprometer a estética minimalista.
- Sugestão de Aplicação para Clientes:** Ideal para criar uma sensação de hotel boutique, permitindo a exibição elegante de amenidades de higiene pessoal.


PASSO A PASSO DO PROJETO

1 PLANEJAMENTO Definir medidas do nicho, posicionamento dos vãos, iluminação e paginação dos veios do porcelanato.	2 CORTE DO PORCELANATO Cortes em 45° (meia esquadria) e separar peças: fundo, laterais, prateleiras e moldura.	3 PREPARAÇÃO DAS PEÇAS Verificar esquadro e nivelamento das peças e preparar a estrutura de fixação.	4 MONTAGEM DO NICHU Colagem das peças internas e externas, alinhamento dos veios e acabamento perfeito.	5 INSTALAÇÃO NA PAREDE Fixação embutida na parede com estrutura reforçada e conferência de prumo e nível.	6 INSTALAÇÃO DA ILUMINAÇÃO Instalar fitas LED no topo de cada vão interno para iluminação indireta e aconchegante.	7 ACABAMENTO FINAL Aplicar silicone neutro nas juntas, limpeza e polimento final das bordas.
---	---	---	--	--	---	---


DETALHES TÉCNICOS E VISTAS

- Iluminação indireta cria efeito de destaque e sensação de profundidade.
- Corte em meia esquadria elimina emendas visíveis e valoriza o acabamento.
- Fixação oculta aumenta o nível de acabamento e sofisticação.


VISTA FRONTAL

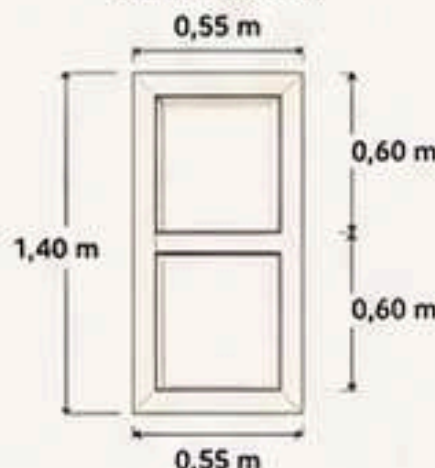

VISTA LATERAL (CORTE)

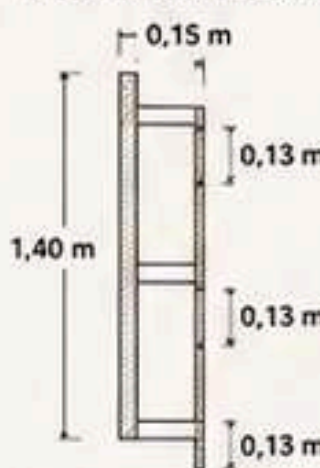

VISTA SUPERIOR (CORTE)

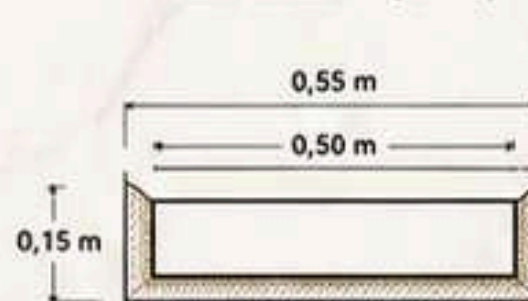

OBSERVAÇÃO:

Medidas internas podem variar conforme a espessura do porcelanato utilizado.

POR QUE ESTE PROJETO VALORIZA O SERVIÇO?

- Valor Percebido:** Eleva o design do banheiro, convertendo uma parede de box simples em um vitrine de luxo para produtos de banho.
- Organização Arquitetônica:** Solução embutida que elimina a desordem visual e maximiza o armazenamento, criando um ambiente limpo e organizado.
- 0 finas é um atestado** de pericia técnica, agindo como um selo de qualidade de acabamento premium.

OBSERVAÇÕES PROFISSIONAIS

Tolerância de execução: ± 2 mm

Utilizar cola específica para porcelanato.

Reforço interno e estruturação é obrigatório.

Conferir esquadro antes da colagem.

ARQUITETURA
DE VALOR

PROJETO 13

ESTANTE VERTICAL COM NICHOS ILUMINADOS EM PORCELANATO MARMORIZADO



MEDIDAS TÉCNICAS DO PROJETO

Altura total da estante:	2,40 m
Largura total da estante:	0,80 m
Profundidade total da estante:	0,20 m
Largura interna dos nichos:	0,70 m
Altura interna de cada nicho:	0,45 m
Profundidade interna dos nichos:	0,18 m
Espessura das bordas (moldura):	0,05 m
Espaçamento entre os nichos:	0,05 m
Distância do piso ao 1º nicho:	0,20 m
Iluminação LED:	3000K (luz quente)

ESPECIFICAÇÕES TÉCNICAS DO PROJETO

Estilo do Projeto	Minimalista Contemporâneo, Luxuoso, Sofisticado
Tipo de Porcelanato	Porcelanato Marmorizado Alto Brilho (Calacatta) e Porcelanato Cinza Acetinado (Piso)
Técnica de Corte	Execução em Meia Esquadria (45°) e Corte Retificado
Aplicação	Nichos Decorativos e Piso de Sala de Jantar (Área Interna)

ANÁLISE DE DESIGN E FUNCIONALIDADE




- Destaque do Projeto:** Estante vertical escultural que combina a textura natural da madeira com o refinamento do porcelanato marmorizado nos nichos.
- Sugestão de Aplicação para Clientes:** Ideal para salas de estar e áreas de convivio que buscam elegância, organização e iluminação decorativa.
- Sugestão de Aplicação para Clientes:** Perfeito para exibir coleções de arte e objetos de design, elevando a experiência do ambiente.

PASSO A PASSO DO PROJETO

1 PLANEJAMENTO 	2 CORTE DO PORCELANATO 	3 PREPARAÇÃO DA ESTRUTURA 	4 MONTAGEM DOS NICHOS 	5 INSTALAÇÃO DA ESTANTE 	6 INSTALAÇÃO DA ILUMINAÇÃO 	7 ACABAMENTO FINAL
Definir medidas, paginação dos veios, marcar pontos hidráulicos (se houver) e verificar nível da parede.	Cortes em 45° (meia esquadria) e separar peças: moldura, fundo, laterais e prateleiras dos nichos.	Verificar nivelamento da parede e preparar estrutura de fixação interna (se necessário).	Colagem das peças internas e externas, alinhamento dos veios e acabamento perfeito.	Fixação da estante na parede com estrutura reforçada e conferência de prumo e nível.	Instalar fitas LED nas partes superiores dos nichos para iluminação indireta.	Aplicar silicone neutro nas junções, limpeza final e polimento das bordas.

DETALHES TÉCNICOS E VISTAS

- Iluminação indireta cria efeito flutuante e sensação de leveza.
- Corte em meia esquadria elimina emendas visíveis e aumenta o padrão.
- Fixação oculta aumenta o nível de acabamento e sofisticação.

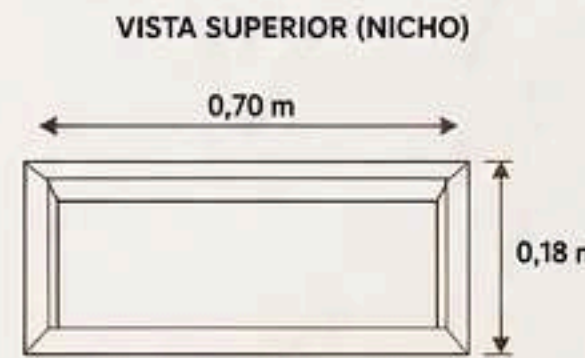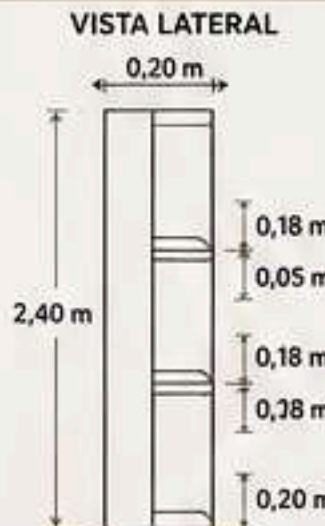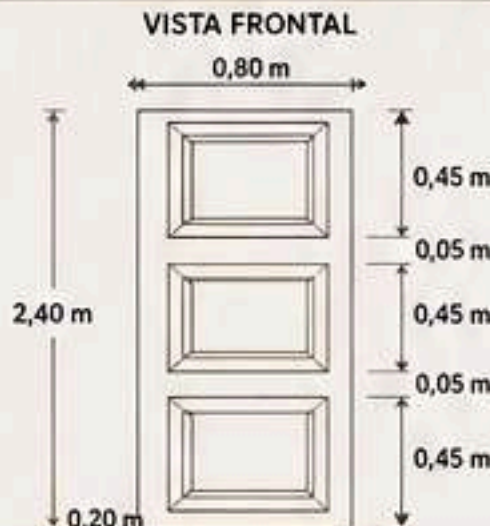

POR QUE ESTE PROJETO VALORIZA O SERVIÇO?

- Estética monolítica:** aparência de peça única esculpida.
- Execução técnica avançada:** exige precisão e experiência.
- Alto valor percebido:** cliente enxerga luxo e exclusividade.

OBSERVAÇÕES PROFISSIONAIS

Tolerância de execução: ± 2 mm

Utilizar cola específica para porcelanato.

Reforço interno é obrigatório.

Conferir esquadro antes da colagem.

ARQUITETURA
DE VALOR

PAREDE DE BOX COM TRÊS NICHOS ILUMINADOS EM PORCELANATO CALACATTA



MEDIDAS TÉCNICAS DO PROJETO

Largura total da parede:	1,20 m a 1,40 m
Altura total da parede:	2,40 m
Profundidade do box:	0,80 m a 0,90 m
NICHOS EMBUTIDOS (3 UNIDADES)	
Nicho superior (L x A x P):	0,60 x 0,25 x 0,10 m
Nicho central (L x A x P):	0,60 x 0,30 x 0,10 m
Nicho inferior (L x A x P):	0,60 x 0,25 x 0,10 m
Distância entre nichos:	0,10 m
Altura do piso até 1º nicho:	1,00 m
Altura total dos nichos:	1,10 m a 1,20 m
Iluminação LED:	3000K (luz quente)

ESPECIFICAÇÕES TÉCNICAS DO PROJETO


Estilo do Projeto	Minimalista Contemporâneo de Luxo
Tipo de Porcelanato	Porcelanato Marmorizado de Alto Brilho (Calacatta)
Técnica de Corte	Execução em Meia Esquadria (45°)
Aplicação	Área de Box (Banheiro Master)
Rejunte	Mínimo ou Invisível
Iluminação	Fita LED embutida em cada nicho Perfil de alumínio embutido

ANÁLISE DE DESIGN E FUNCIONALIDADE

- Nichos iluminados criam efeito sofisticado e funcional.
- Integração total com o revestimento da parede.
- Valorização dos veios do porcelanato.
- Organização dos produtos de banho e fácil manutenção.

PASSO A PASSO DO PROJETO

1 PLANEJAMENTO	2 CORTE DO PORCELANATO	3 EXECUÇÃO DOS NICHOS	4 INSTALAÇÃO NA PAREDE	5 ILUMINAÇÃO	6 ACABAMENTOS
Definir posição dos nichos, marcar pontos hidráulicos e verificar estrutura da parede.	Cortes em 45° (meia esquadria) e separar peças: fundo, laterais, base e topo dos nichos.	Montar estrutura interna, garantir leve caimento para água e impermeabilizar totalmente.	Embutir nichos na alvenaria, fixar com argamassa adequada e nivelar todos os nichos.	Instalar fita LED nos nichos, embutir perfil de alumínio e fazer isolamento contra umidade.	Aplicar rejunte fino, silicone nas bordas e limpeza final.

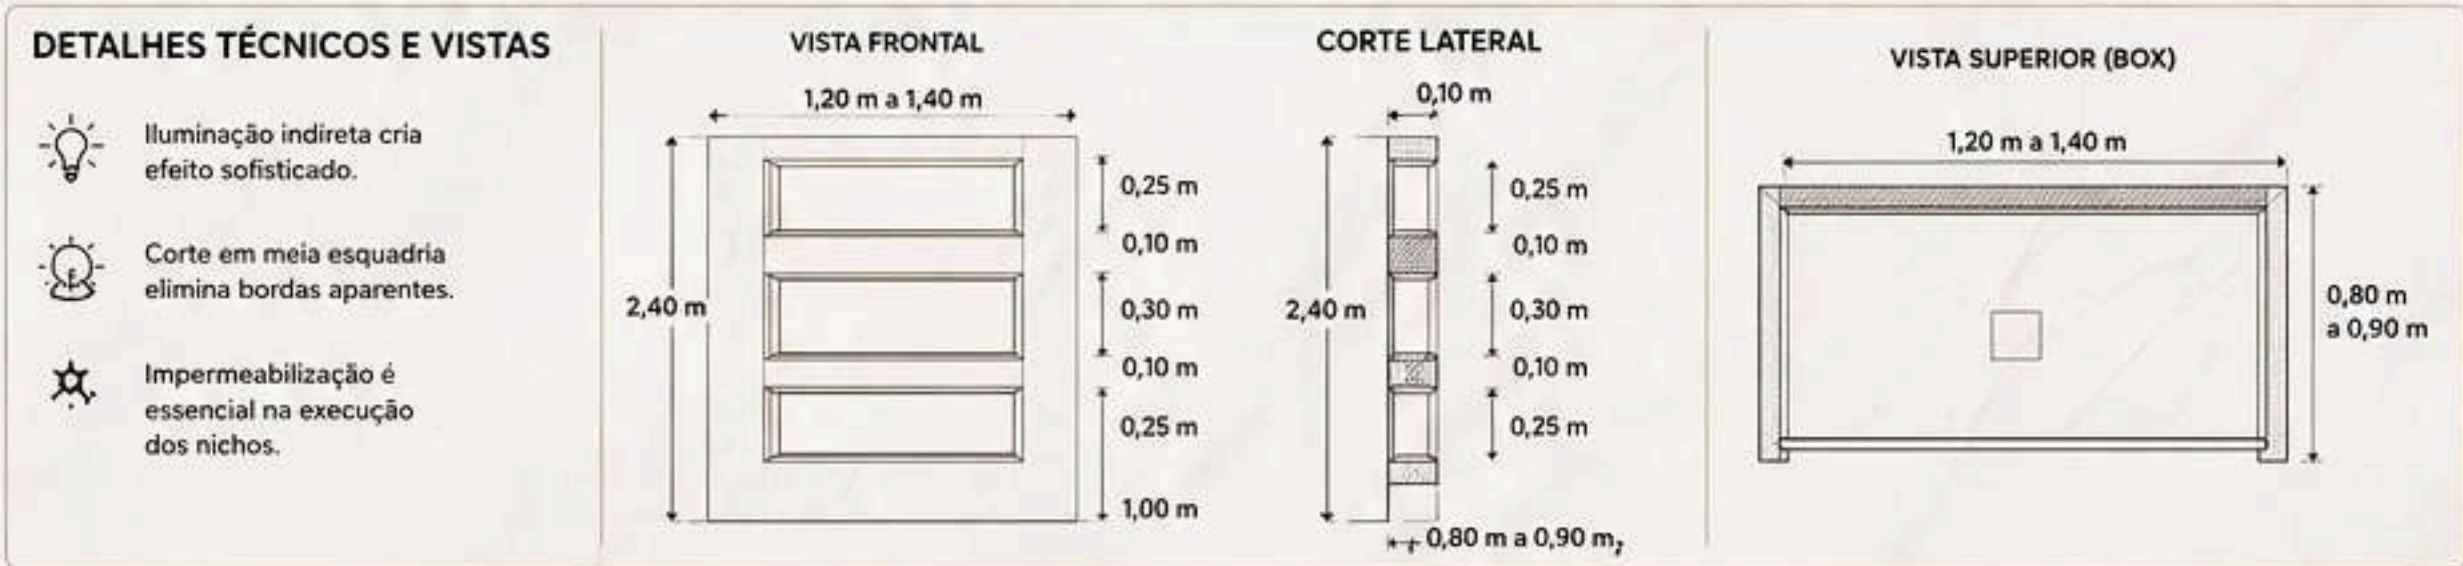

POR QUE ESTE PROJETO VALORIZA O SERVIÇO? - Alto padrão visual que eleva o nível do ambiente. - Execução técnica especializada e detalhada. - Grande valor percebido pelo cliente.	OBSERVAÇÕES PROFISSIONAIS - Impermeabilização é obrigatória. - Usar LED próprio para área úmida. - Tolerância de execução: ± 2 mm - Conferir alinhamento antes da colagem.	ARQUITETURA DE VALOR
--	---	----------------------

PROJETO 16

BANCADA ESCULPIDA E ESPELHO LED EM PORCELANATO MARMORIZADO MONOBLOCO



MEDIDAS TÉCNICAS DO PROJETO

Largura da bancada:	1,20 m a 1,80 m
Profundidade da bancada:	0,50 m a 0,60 m
Altura da bancada:	0,15 m
Altura do piso até topo da bancada:	0,90 m
Cuba esculpida (L x P x A):	0,60 x 0,30 x 0,10 m
Espessura do tampo (borda):	0,06 m
Espaço inferior (prateleira):	0,20 m
Altura do espelho:	0,90 m
Largura do espelho:	0,70 m a 1,20 m
Iluminação LED (espelho):	3000K (luz quente)
Iluminação LED (nicho):	3000K (luz quente)

ESPECIFICAÇÕES TÉCNICAS DO PROJETO

Estilo do Projeto	Minimalista Luxuoso, Escultural, Contemporâneo
Tipo de Porcelanato	Porcelanato Marmorizado de Alto Brilho (Calacatta)
Técnica de Corte	Execução em Meia Esquadria (45°) e Corte Esculpido
Aplicação	Lavabo de Alto Padrão (Área Seca)

ANÁLISE DE DESIGN E FUNCIONALIDADE


- Contraste Sofisticado:** A bancada monobloco esculpida cria um visual contínuo e clean, enquanto o grande espelho LED emoldurado adiciona amplitude e luxo.
- Sugestão de Aplicação para Clientes:** Perfeito para lavabos e banheiros de suítes master que buscam um ponto focal elegante e funcional.
- Otimização de Espaço:** A prateleira inferior flutuante oferece armazenamento visível e elegante, contribuindo para a sensação de organização.

PASSO A PASSO DO PROJETO

1 PLANEJAMENTO Definir medidas, paginar os veios do porcelanato, posicionar pontos hidráulicos e verificar estrutura da parede.	2 CORTE DO PORCELANATO Cortes em 45° (meia esquadria) e separar peças: tampo, laterais, fundo, prateleira e cuba esculpida.	3 EXECUÇÃO DA CUBA ESCULPIDA Execução da cuba com caimento interno, furação para ralo e acabamento perfeito.	4 MONTAGEM DO MONOBLOCO Colagem e alinhamento das peças, reforço interno e verificação de nível.	5 INSTALAÇÃO DA BANCADA Fixação com estrutura metálica oculta, nivelamento preciso e instalação da torneira e sifão.	6 INSTALAÇÃO DO ESPELHO LED Fixação do espelho, conexão elétrica e conferência da iluminação LED.	7 ACABAMENTO FINAL Aplicar silicone neutro nas junções, limpeza e polimento final das superfícies.
--	--	---	---	---	--	---

DETALHES TÉCNICOS E VISTAS

- Iluminação indireta no espelho cria efeito flutuante e sensação de amplitude.
- Corte em meia esquadria elimina emendas visíveis e valoriza o acabamento.
- Fixação oculta aumenta o nível de acabamento e de sofisticação.

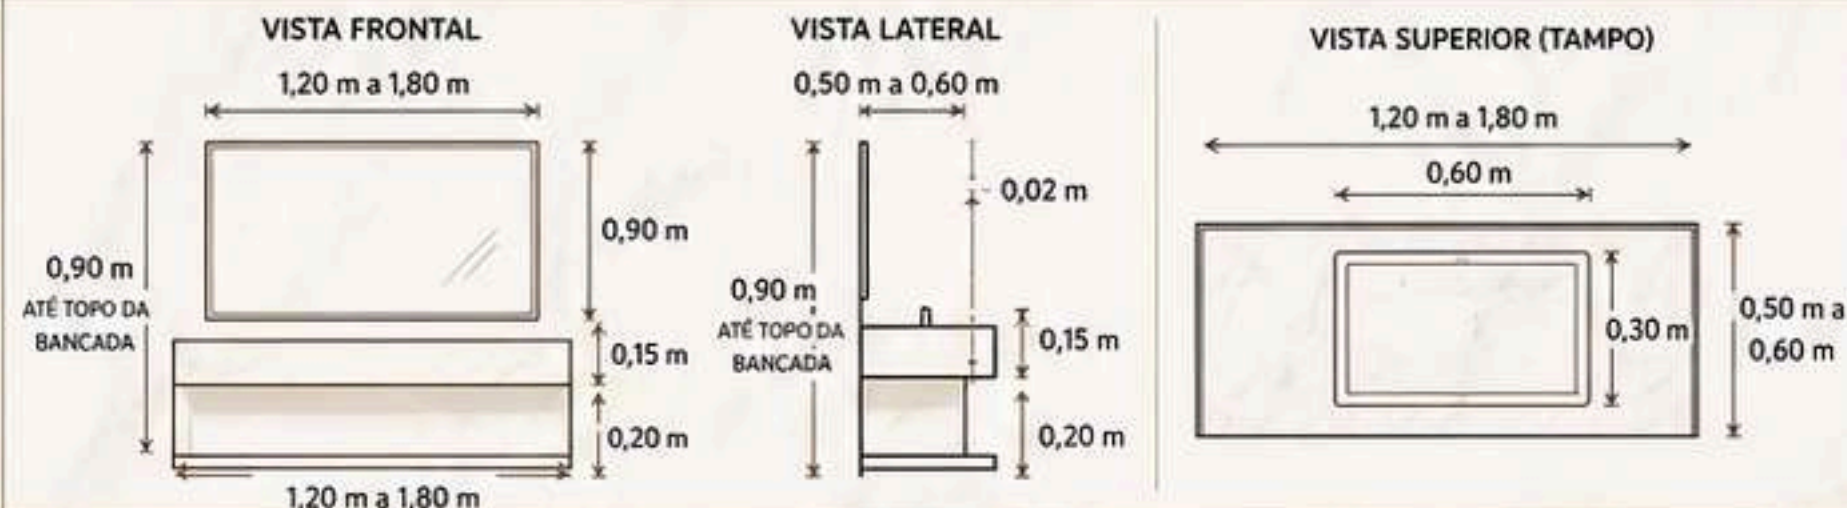

POR QUE ESTE PROJETO VALORIZA O SERVIÇO?

- Valor Percebido:** Transforma o ambiente em um espaço de luxo e bem-estar.
- Execução Técnica Avançada:** Exige precisão, experiência e domínio em porcelanato de alto padrão.
- Grande Valor Percebido pelo Cliente:** Solução sofisticada que eleva o padrão do imóvel e do acabamento.

OBSERVAÇÕES PROFISSIONAIS

Impermeabilização é obrigatória.

Usar LED próprio para área seca.

Tolerância de execução: ± 2 mm.

Conferir alinhamento antes da colagem.

ARQUITETURA
DE VALOR

NICHU TÉCNICO E ILUMINADO EM PORCELANATO
MARMORIZADO CALACATTA PARA COZINHA PLANEJADA

DETALHE ILUMINAÇÃO LED



DETALHE CORTE MEIA ESQUADRIA



DETALHE DA PRATELEIRA (TAMPO)



MEDIDAS TÉCNICAS DO PROJETO

Largura interna do nicho:	0,90 m a 1,20 m
Altura interna do nicho:	0,45 m
Profundidade interna do nicho:	0,30 m
Altura total do nicho (externa):	0,60 m
Espessura da prateleira (tampo):	0,02 m
Espessura das laterais:	0,02 m
Espessura do fundo:	0,02 m
Recuo da iluminação LED:	2 cm (do fundo)
Iluminação LED:	3000K (luz quente)

ESPECIFICAÇÕES TÉCNICAS DO PROJETO

Estilo do Projeto	Minimalista Gourmet Planejado
Tipo de Porcelanato	Porcelanato Marmorizado Alto Brilho (Calacatta)
Técnica de Corte	Execução em Meia Esquadria (45°) e Corte Retificado
Aplicação	Bancada e Nicho Técnico de Cozinha
Iluminação	Fita LED embutida em perfil de alumínio 3000K (luz quente)

ANÁLISE DE DESIGN E FUNCIONALIDADE

- Destaque do Projeto:** Nicho técnico e iluminado traz sofisticação, organização e valorização da bancada da cozinha.
- Sugestão de Aplicação para Clientes:** Perfeito para apoio de eletrodomésticos, organização de temperos, utensílios ou itens decorativos.
- Otimização de Espaço:** Aproveitamento inteligente da marcenaria planejada, com iluminação que valoriza o acabamento.


PASSO A PASSO DO PROJETO

1 PLANEJAMENTO 	2 CORTE DO PORCELANATO 	3 PREPARAÇÃO DA ESTRUTURA 	4 INSTALAÇÃO DO REVESTIMENTO 	5 INSTALAÇÃO DA ILUMINAÇÃO LED 	6 INSTALAÇÃO DA PRATELEIRA (TAMPO) 	7 ACABAMENTO FINAL
Definir medidas do nicho e posicionamento na marcenaria planejada.	Cortes em 45° (meia esquadria) e separar peças: fundo, laterais e prateleira.	Verificar nivelamento, resistência e fixação da estrutura do móvel.	Fixar o fundo e as laterais com argamassa adequada e nivelar as peças.	Instalar fita LED embutida em perfil de alumínio, recuada 2 cm do fundo.	Assentar a prateleira (tampo) com corte em meia esquadria e acabamento perfeito.	Aplicar rejunte fino, silicone nas juntas e limpeza final.


DETALHES TÉCNICOS E VISTAS

- Iluminação indireta cria conforto visual e destaque ao ambiente.
- Corte em meia esquadria garante acabamento limpo e sem emendas aparentes.
- Integração com marcenaria gera um visual sofisticado e funcional.


VISTA FRONTAL

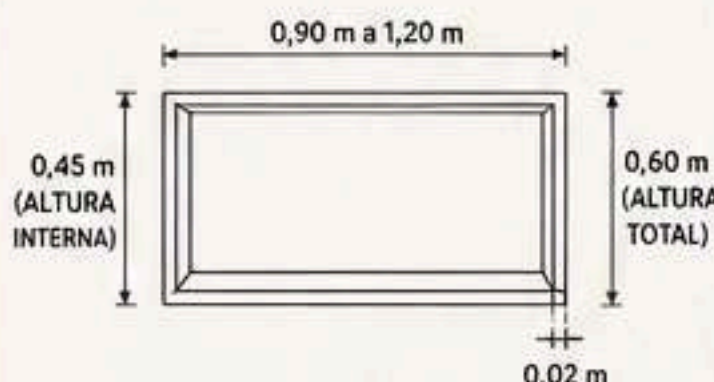

VISTA LATERAL (CORTE)

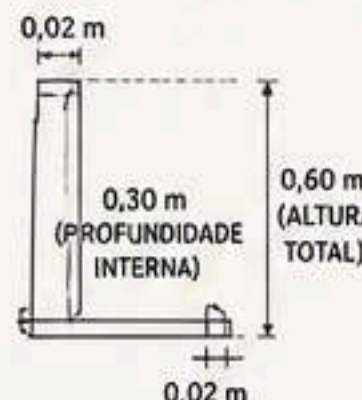

VISTA SUPERIOR (PLANTA)

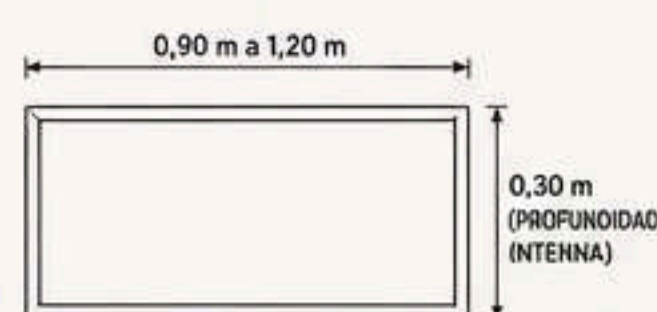

POR QUE ESTE PROJETO VALORIZA O SERVIÇO?

- Valorização do Ambiente:** transforma a cozinha em um espaço sofisticado e funcional.
- Execução Técnica Avançada:** exige precisão, experiência e acabamento impecável.
- Grande Valor Percebido pelo Cliente:** solução prática que eleva o padrão de acabamento do mobiliário.

OBSERVAÇÕES PROFISSIONAIS

Impermeabilização é obrigatória.

Usar LED próprio para áreas internas úmidas.

Tolerância de execução: ± 2 mm.

Conferir alinhamento antes da colagem e acabamento final.

ARQUITETURA
DE VALOR

COZINHA MODERNISTA COM FRONTÃO E BANCADA EM PORCELANATO MARMORIZADO POLIDO E MARCENARIA INTEGRADA




DETALHE DO FRONTÃO

ALTURA DO FRONTÃO
0,45 m a 0,60 m

DETALHE DA BANCADA

ESPESSURA DA BANCADA
0,03 m (3 cm)

DETALHE DA MARCENARIA

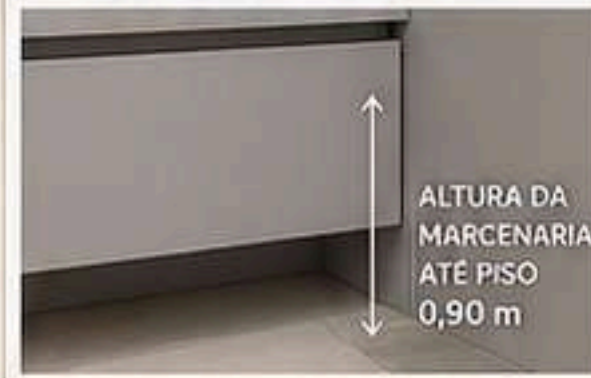ALTURA DA MARCENARIA
ATÉ PISO
0,90 m

MEDIDAS TÉCNICAS DO PROJETO

Comprimento total da bancada:	2,40 m a 3,60 m
Profundidade da bancada:	0,60 m
Espessura da bancada:	0,03 m (3 cm)
Altura da bancada (do piso):	0,90 m
Altura do frontão (armários superiores):	0,45 m a 0,60 m
Profundidade dos armários superiores:	0,35 m
Altura entre bancada e armários superiores:	0,55 m a 0,60 m
Altura total do conjunto (piso ao topo):	2,25 m a 2,40 m
Espessura do backsplash (revestimento):	0,01 m (1 cm)
Recuo do rodapé (móveis):	0,08 m
Iluminação LED (temperatura):	3000K (luz quente)
Tensão LED recomendada:	12V

ESPECIFICAÇÕES TÉCNICAS DO PROJETO

Estilo do Projeto:	Modernista Contemporâneo
Tipo de Porcelanato:	Porcelanato Marmorizado Alto Brilho (com veios cinza contínuos)
Técnica de Corte:	Execução em Meia Esquadria (45°) e Corte Retificado
Aplicação:	Cozinha Planejada (Bancada, Frontão e Piso)
Acabamento:	Polido (bancada e frontão)
Marcenaria:	MDF ou MDP com acabamento amadeirado (ou laca fosca) integrado
Iluminação:	Fita LED embutida sob os armários superiores
Ambiente:	Cozinha Residencial Gourmet

ANÁLISE DE DESIGN E FUNCIONALIDADE

- Destaque do Projeto:** Contraste Sofisticado: Integração de madeira quente nos armários superiores com o porcelanato marmorizado frio e polido do frontão e bancada.
- Sugestão de Aplicação para Clientes:** Ideal para Áreas Gourmet: Perfeito para cozinhas de conceito aberto ou áreas integradas, unindo estética e funcionalidade.
- Sugestão de Aplicação para Clientes:** Manutenção Simplificada: A superfície polida e sem emendas visíveis do frontão facilita a limpeza e higiene diária, ideal para áreas de preparo de alimentos.

POR QUE ESTE PROJETO VALORIZA O SERVIÇO DE PORCELANATO?

- Estética de Luxo:** A combinação de mármore polido e marcenaria sob medida eleva o padrão de acabamento e sofisticação de um ambiente residencial.
- Integração de Materiais:** Unifica bancada, frontão e piso com um elemento de design de alto valor percebido, transmitindo modernidade e elegância.
- Valorização do Imóvel:** Projetos com materiais nobres e execução precisa impactam diretamente na valorização do imóvel.
- Durabilidade e Praticidade:** Porcelanato de alta performance garante beleza contínua, resistência a manchas, calor e riscos, ideal para cozinhas.
- Execução Técnica de Alto Nível:** Cortes retificados, meia esquadria e acabamento polido exigem mão de obra especializada e atenção aos detalhes.


PASSO A PASSO DO PROJETO

1 PLANEJAMENTO 	2 CORTE DO PORCELANATO 	3 PREPARAÇÃO DA BASE 	4 INSTALAÇÃO DA BANCADA 	5 INSTALAÇÃO DO FRONTÃO 	6 ILUMINAÇÃO LED 	7 ACABAMENTO FINAL
Definir medidas, verificar pontos elétricos, hidráulicos e exaustão. Planejar marcenaria e iluminação.	Cortes em 45° (meia esquadria) e separar peças: bancada, frontão, laterais e piso.	Nivelar e preparar a base da bancada e frontão com impermeabilização adequada.	Assentar e fixar a bancada com argamassa específica, garantir nivelamento e alinhamento.	Fixar o frontão com cortes precisos e acabamento em meia esquadria nas extremidades.	Instalar fita LED embutida em perfil de alumínio sob os armários superiores.	Aplicar rejunte fino, selicone em juntas e limpeza técnica final.


DETALHES TÉCNICOS E VISTAS

- Iluminação indireta cria efeito de leveza e sofisticação.
- Corte em meia esquadria elimina bordas aparentes e valoriza os veios contínuos.
- Integração perfeita entre porcelanato e marcenaria planejada.


VISTA FRONTAL

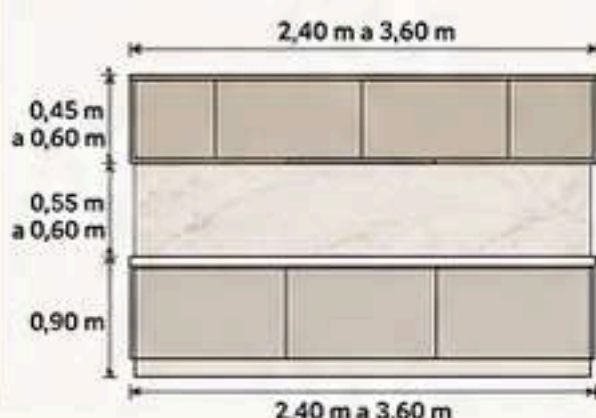

VISTA LATERAL (CORTE)

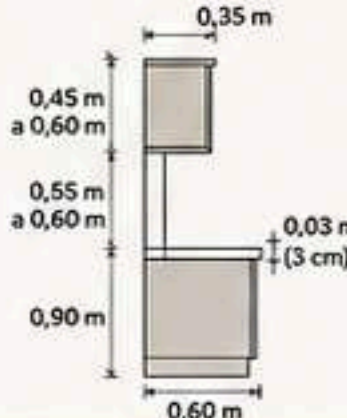

VISTA SUPERIOR (PLANTA)

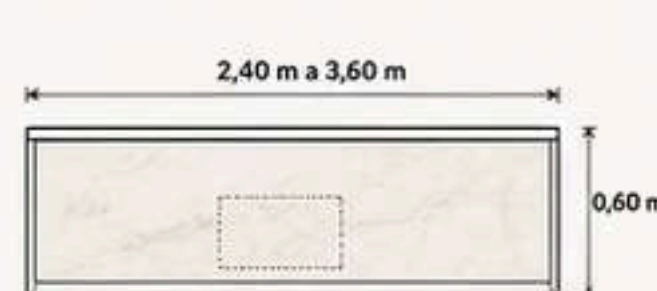

POR QUE ESTE PROJETO VALORIZA O SERVIÇO?

- Alto valor percebido:** design exclusivo com materiais nobres e integração perfeita.
- Execução técnica avançada:** exige precisão, acabamento impecável e domínio de cortes.
- Grande valor percebido pelo cliente:** solução elegante, funcional e que agrega muito valor ao imóvel.

OBSERVAÇÕES PROFISSIONAIS

Impermeabilização é obrigatória.

Usar LED próprio para áreas úmidas.

 Tolerância de execução: ± 2 mm.

Conferir alinhamento antes da colagem.

ARQUITETURA
DE VALOR

COZINHA MINIMALISTA COM NICHOS VERTICAIS DUPLOS E REVESTIMENTO TEXTURIZADO EM PORCELANATO




DETALHE DO NICHOS SUPERIOR



DETALHE DO NICHOS INFERIOR



DETALHE DO REVESTIMENTO

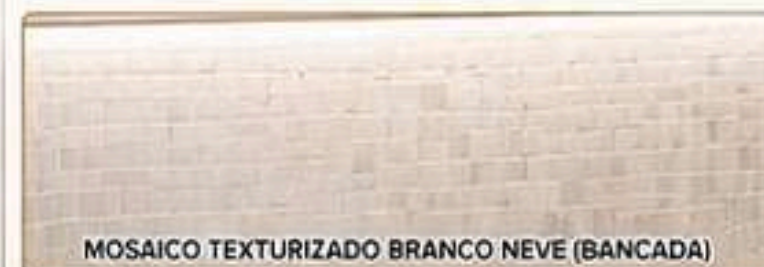

MOSAICO TEXTURIZADO BRANCO NEVE (BANCADA)

MEDIDAS TÉCNICAS DO PROJETO

Largura de cada nicho:	0,80 m
Altura de cada nicho:	0,40 m
Profundidade dos nichos:	0,12 m
Distância entre nichos:	0,10 m
Altura do nicho inferior até a bancada:	0,55 m
Altura total ocupada pelos nichos:	0,90 m
Espessura da prateleira (nicho):	0,02 m (2 cm)
Largura da parede onde estão os nichos:	1,00 m a 1,20 m
Altura total da parede:	2,40 m até o teto (média)
Iluminação LED:	Fita LED embutida 3000K (luz quente)
Potência recomendada:	9,6W/m
Tensão:	12V

ESPECIFICAÇÕES TÉCNICAS DO PROJETO

Estilo do Projeto	Minimalista Contemporâneo, Funcional
Tipo de Porcelanato	Porcelanato Mosaico Texturizado (Paredes) e Porcelanato Branco Neve (Bancada)
Técnica de Corte	Corte Retificado e Acabamento de Nichos Embutidos
Aplicação	Área de Bancada e Parede de Cozinha
Rejunte	Rejunte Acrílico Branco ou Cinza Claro (mínimo)
Iluminação	Fita LED embutida sob os armários e nos nichos
Ambiente	Cozinha Residencial
Acabamentos	Bancada em Porcelanato, Nichos alinhados com corte perfeito e iluminação integrada

ANÁLISE DE DESIGN E FUNCIONALIDADE

- Destaque do Projeto:** Nichos verticais duplos criam organização e otimizam o espaço de armazenamento vertical, exibindo itens de cozinha de forma estilosa.
- Sugestão de Aplicação para Clientes:** Perfeito para cozinhas modernas que buscam funcionalidade e estética limpa.
- Análise de Design:** A iluminação LED integrada sob os armários e nos nichos realça a textura do mosaico, criando um ambiente acolhedor e sofisticado.

POR QUE ESTE PROJETO VALORIZA O SERVIÇO DE PORCELANATO?

- Valorização do Ambiente:** O projeto combina nichos embutidos, iluminação e revestimento texturizado, criando um acabamento de alto padrão que valoriza o imóvel.
- Funcionalidade e Estética:** Mostra domínio técnico na execução de nichos embutidos e acabamentos refinados com porcelanato de mosaico.
- Resistência e Higiene:** O porcelanato é resistente a manchas, calor, umidade e fácil de limpar, ideal para cozinhas.
- Acabamento Premium:** A precisão nos cortes e no nivelamento dos nichos garante um visual de sofisticação e luxo percebido.


PASSO A PASSO DO PROJETO

1 PLANEJAMENTO 	2 MARCAÇÃO E CORTE 	3 EXECUÇÃO DOS NICHOS 	4 INSTALAÇÃO DO REVESTIMENTO 	5 INSTALAÇÃO DA ILUMINAÇÃO LED 	6 ACABAMENTOS E REJUNTE 	7 LIMPEZA FINAL E ENTREGA
Definir medidas dos nichos, posicionamento e pontos elétricos. Verificar estrutura da parede.	Marcar os nichos na parede e realizar os cortes com ferramentas adequadas.	Embutir os nichos na alvenaria e nivelar as superfícies internas.	Aplicar argamassa e assentar o mosaico texturizado na parede.	Instalar fita LED nos nichos e sob os armários com perfil de alumínio embutido.	Aplicar rejunte fino e silicone nas bordas internas e externas dos nichos.	Limpeza técnica final e nível antes geral do calagem final.


DETALHES TÉCNICOS E VISTAS

- Iluminação LED valoriza a textura do mosaico.
- Cortes em meia esquadria garantem acabamento perfeito e sem emendas aparentes.
- Impermeabilização da área da bancada para maior durabilidade.


VISTA FRONTAL (PAREDE)

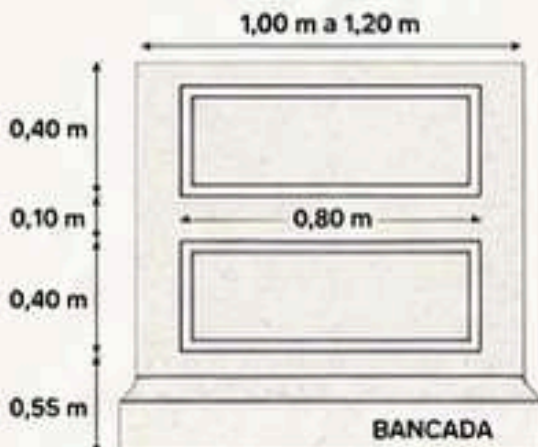

VISTA LATERAL (CORTE)

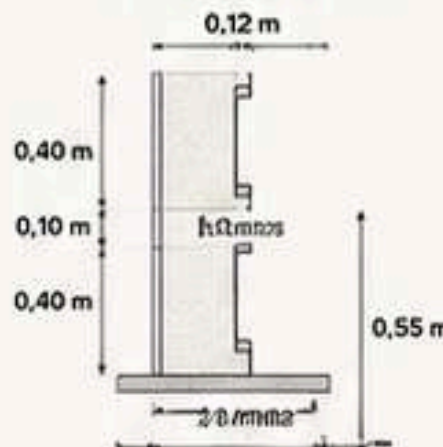

VISTA SUPERIOR (PLANTA)

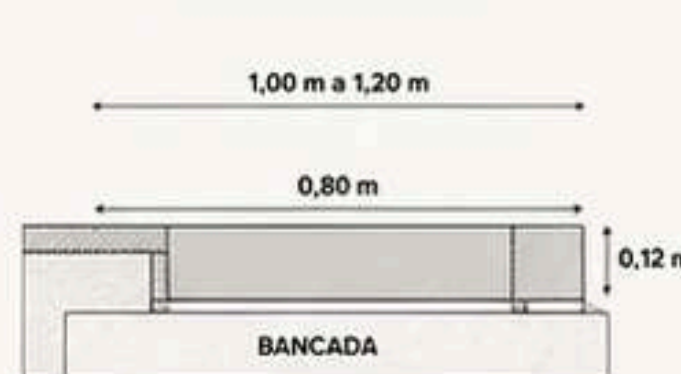

POR QUE ESTE PROJETO VALORIZA O SERVIÇO?

- Alto valor percebido:** Projeto moderno e funcional que agrega valor ao imóvel.
- Execução técnica avançada:** Nichos embutidos, iluminação e mosaico exigem especialização e precisão.
- Grande valor percebido pelo cliente:** Solução completa que une beleza, organização e praticidade.

OBSERVAÇÕES PROFISSIONAIS

Impermeabilização nos nichos e na bancada é obrigatória.

Usar LED próprio para áreas úmidas e perfil de alumínio.

Tolerância de execução: ± 2 mm.

Conferir alinhamento e nível antes da colagem final.

ARQUITETURA
DE VALOR


VAIDADE DE LUXO COM NICHOS DE MOSAICO DE PORCELANATO



DETALHE DO NICHU



DETALHE DO MOSAICO

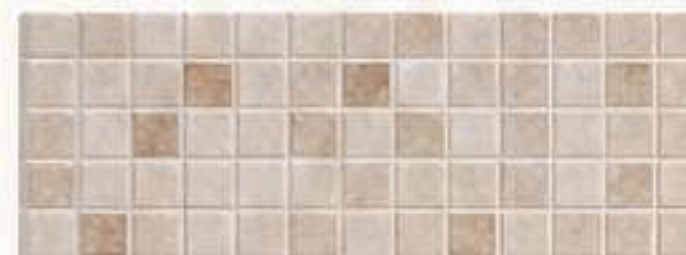MOSAICO DE PORCELANATO
TONS CREME E BEGE (PADRÃO GEOMÉTRICO)

DETALHE DA PRATELEIRA



MEDIDAS TÉCNICAS DO PROJETO

Largura do nicho:	0,80 m a 1,20 m
Altura de cada nicho:	0,35 m
Profundidade do nicho:	0,12 m
Espessura da prateleira:	0,04 m (4 cm)
Distância entre prateleiras:	0,35 m
Distância entre nichos:	0,10 m (mínimo)
Altura do primeiro nicho (do tampo):	0,20 m
Altura total da parede com nichos:	1,40 m a 2,20 m
Recuo da parede de fundo:	0,02 m (2 cm)
Iluminação LED:	Fita LED embutida 3000K (luz quente)
Tensão LED recomendada:	12V
Potência recomendada:	9,6W/m

ESPECIFICAÇÕES TÉCNICAS DO PROJETO

Estilo do Projeto	Eclético Sofisticado, Decorativo
Tipo de Porcelanato	Mosaico de Porcelanato em Tons Creme e Bege (Padrão Geométrico)
Técnica de Corte	Corte Retificado de Precisão (Mosaico)
Aplicação	Parede Decorativa com Nichos (Área de Vaidade/Vaidade)
Rejunte	Rejunte Epóxi ou Acrílico na cor bege claro
Iluminação	Fita LED embutida sob as prateleiras dos nichos
Acabamentos	Prateleiras em Porcelanato com Corte Reto e Acabamento Polido

ANÁLISE DE DESIGN E FUNCIONALIDADE

- O mosaico de porcelanato em tons creme e bege cria uma textura tátil e luxuosa no fundo dos nichos.
- A composição com prateleiras embutidas e sobrepostas adiciona área de exibição para coleções de perfumes e itens decorativos de alto padrão, demonstrando sofisticação.
- O espelho adjacente amplia o espaço e duplica a visualização da composição, reforçando o impacto visual.

POR QUE ESTE PROJETO VALORIZA O SERVIÇO DE PORCELANATO?

- Personalização de Espaço:** Transforma uma área de vaidade funcional em uma vitrine personalizada para coleções pessoais de luxo.
- Detalhe Arquitetônico:** O uso de mosaico de porcelanato adiciona um detalhe arquitetônico sofisticado e tátil que valoriza a parede.
- Execução Premium:** A precisão dos cortes de mosaico e a montagem das prateleiras sobrepostas atestam a qualidade superior da execução e do design.

PASSO A PASSO DO PROJETO

1 PLANEJAMENTO 	2 EXECUÇÃO DOS NICHOS 	3 PREPARAÇÃO DA PAREDE 	4 ASSENTAMENTO DO MOSAICO 	5 INSTALAÇÃO DAS PRATELEIRAS 	6 INSTALAÇÃO DA ILUMINAÇÃO LED 	7 ACABAMENTO FINAL
Definir medidas dos nichos, posicionamento, altura das prateleiras, pontos elétricos e estilo do mosaico.	Embutir os nichos na alvenaria com recuo e nivelamento perfeitos, garantindo prumo e esquadro.	Impermeabilizar o fundo dos nichos e a área da parede. Aplicar argamassa colante adequada.	Assentar o mosaico de porcelanato com juntas alinhadas e espaçamento uniforme.	Fixar as prateleiras em porcelanato com nível e prumo, garantindo perfeito alinhamento.	Instalar fita LED embutida sob as prateleiras com perfil de alumínio para dissipação de calor.	Aplicar rejunte adequado, fazer limpeza final e testar iluminação.

DETALHES TÉCNICOS E VISTAS



A iluminação LED embutida valoriza o mosaico e os objetos decorativos.




O mosaico em tons neutros proporciona elegância e intemporalidade.




Rejunte epóxi garante maior durabilidade e resistência à umidade.

VISTA FRONTAL

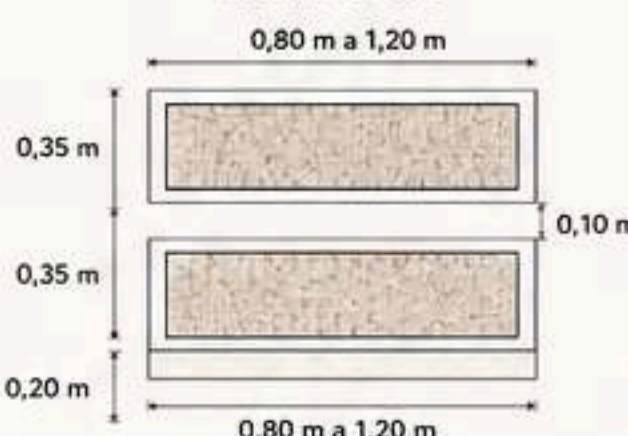

VISTA LATERAL (CORTE)

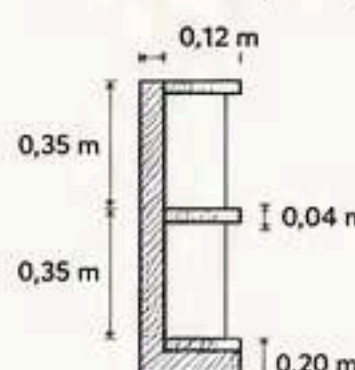

VISTA SUPERIOR (PLANTA DO NICHU)



POR QUE ESTE PROJETO VALORIZA O SERVIÇO?

- Alto Valor Percebido:** Nichos iluminados e acabamento em mosaico elevam o padrão do ambiente.
- Execução Técnica Avançada:** Mosaico pequeno exige precisão, alinhamento e domínio técnico.
- Grande Valor Percebido pelo Cliente:** Solução completa que une beleza, organização e sofisticação.



Impermeabilização dos nichos é obrigatória.



Usar LED próprio para ambientes internos.




Tolerância de execução: ± 2 mm.



Conferir alinhamento e nível antes da colagem final.

ARQUITETURA
DE VALOR

PROJETO 21

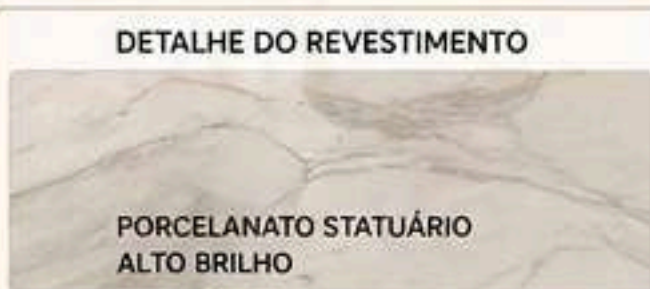COMPOSIÇÃO TRIPLEX DE NICHOS EM PORCELANATO
STATUÁRIO COM ILUMINAÇÃO INTEGRADA

MEDIDAS TÉCNICAS DO PROJETO

Largura de cada nicho:	1,20 m
Altura de cada nicho:	0,40 m
Profundidade dos nichos:	0,12 m
Distância entre nichos:	0,10 m
Altura do primeiro nicho (do piso):	0,60 m
Altura do centro do nicho:	0,80 m / 1,30 m / 1,80 m
Altura total ocupada pelos nichos:	1,40 m
Espessura da prateleira (frontal):	0,04 m (4 cm)
Espessura das laterais:	0,02 m (2 cm)
Recuo da parede de fundo:	0,02 m (2 cm)
Iluminação LED:	Fita LED embutida 3000K (luz quente)
Tensão LED recomendada:	12V
Potência recomendada:	9,6W/m

ESPECIFICAÇÕES TÉCNICAS DO PROJETO

Estilo do Projeto	Minimalista Contemporâneo, Sofisticado
Tipo de Porcelanato	Porcelanato Marmorizado Alto Brilho (Statuario)
Técnica de Corte	Execução em Meia Esquadria (45°)
Aplicação	Parede de Destaque (Sala de Estar / Estar Íntimo)
Rejunte	Rejunte Epóxi ou Acrílico na cor cinza claro (mínimo)
Iluminação	Fita LED embutida em perfil de alumínio
Acabamentos	Superfícies polidas, acabamento preciso e alinhamento perfeito

ANÁLISE DE DESIGN E FUNCIONALIDADE



- Destaque do Projeto:** Sistema triplex de nichos embutidos com revestimento marmorizado contínuo, criando uma galeria de arte privada em múltiplos níveis.
- Sugestão de Aplicação para Clientes:** Perfeito para salas de estar e corredores que buscam um elemento arquitetônico de luxo e ponto focal sofisticado.
- Análise de Design:** A iluminação integrada valoriza a textura contínua do Statuario, eleva a percepção de espaço e cria sofisticação atemporal.

PASSO A PASSO DO PROJETO

1 PLANEJAMENTO Definir medidas e posições dos nichos, verificar pontos elétricos e estrutura da parede.	2 MARCAÇÃO E CORTE Marcar e cortar as peças em meia esquadria (45°): laterais, fundo, topo, base e prateleiras.	3 EXECUÇÃO DOS NICHOS Embutir os nichos na alvenaria, nivelar e fixar garantindo prumo e esquadramento.	4 IMPERMEABILIZAÇÃO Impermeabilizar o fundo e laterais internas dos nichos antes da colagem do porcelanato.	5 INSTALAÇÃO DAS PEÇAS Assentar e colar cada peça de porcelanato com argamassa adequada, garantindo alinhamento perfeito.	6 ILUMINAÇÃO LED Instalar perfil de alumínio e fita LED embutida, testar funcionamento e organizar a fiação.	7 ACABAMENTO FINAL Aplicar rejunte fino, silicone nas juntas e limpeza técnica final.
--	--	--	--	--	---	--

DETALHES TÉCNICOS E VISTAS

- Iluminação LED integrada valoriza os volumes e cria atmosfera sofisticada.
- Corte em meia esquadria (45°) garante acabamento impecável sem cantos aparentes.
- Porcelanato Statuario polido oferece elegância, durabilidade e fácil manutenção.

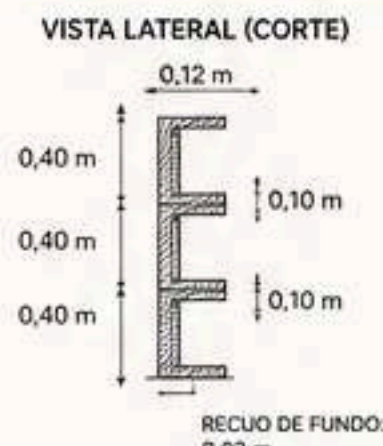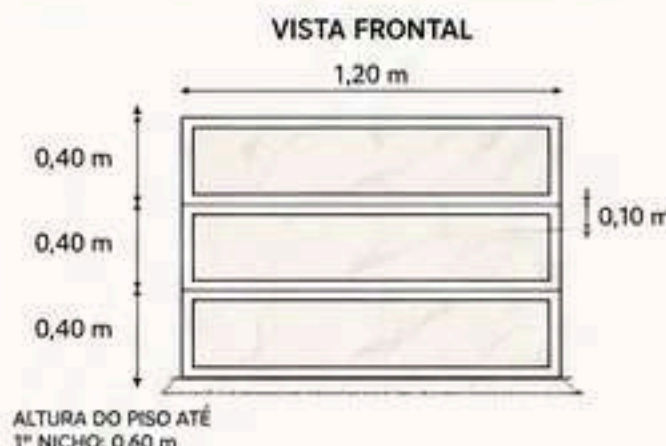

POR QUE ESTE PROJETO VALORIZA O SERVIÇO?

- Alto Valor Percebido:** Nichos iluminados com porcelanato Statuario agregam valor instantâneo ao ambiente.
- Execução Técnica Avançada:** Meia esquadria, iluminação embutida e alinhamentos precisos exigem mão de obra especializada.
- Grande Valor Percebido pelo Cliente:** Solução completa que une beleza, organização e sofisticação.

OBSERVAÇÕES PROFISSIONAIS

Impermeabilização dos nichos é essencial.

Usar LED próprio para ambientes internos.

Tolerância de execução: ± 2 mm.

Conferir alinhamento e nível antes da colagem final.

ARQUITETURA
DE VALOR