


PROJETOS PRONTOS

PAINÉIS E DETALHES DECORATIVOS

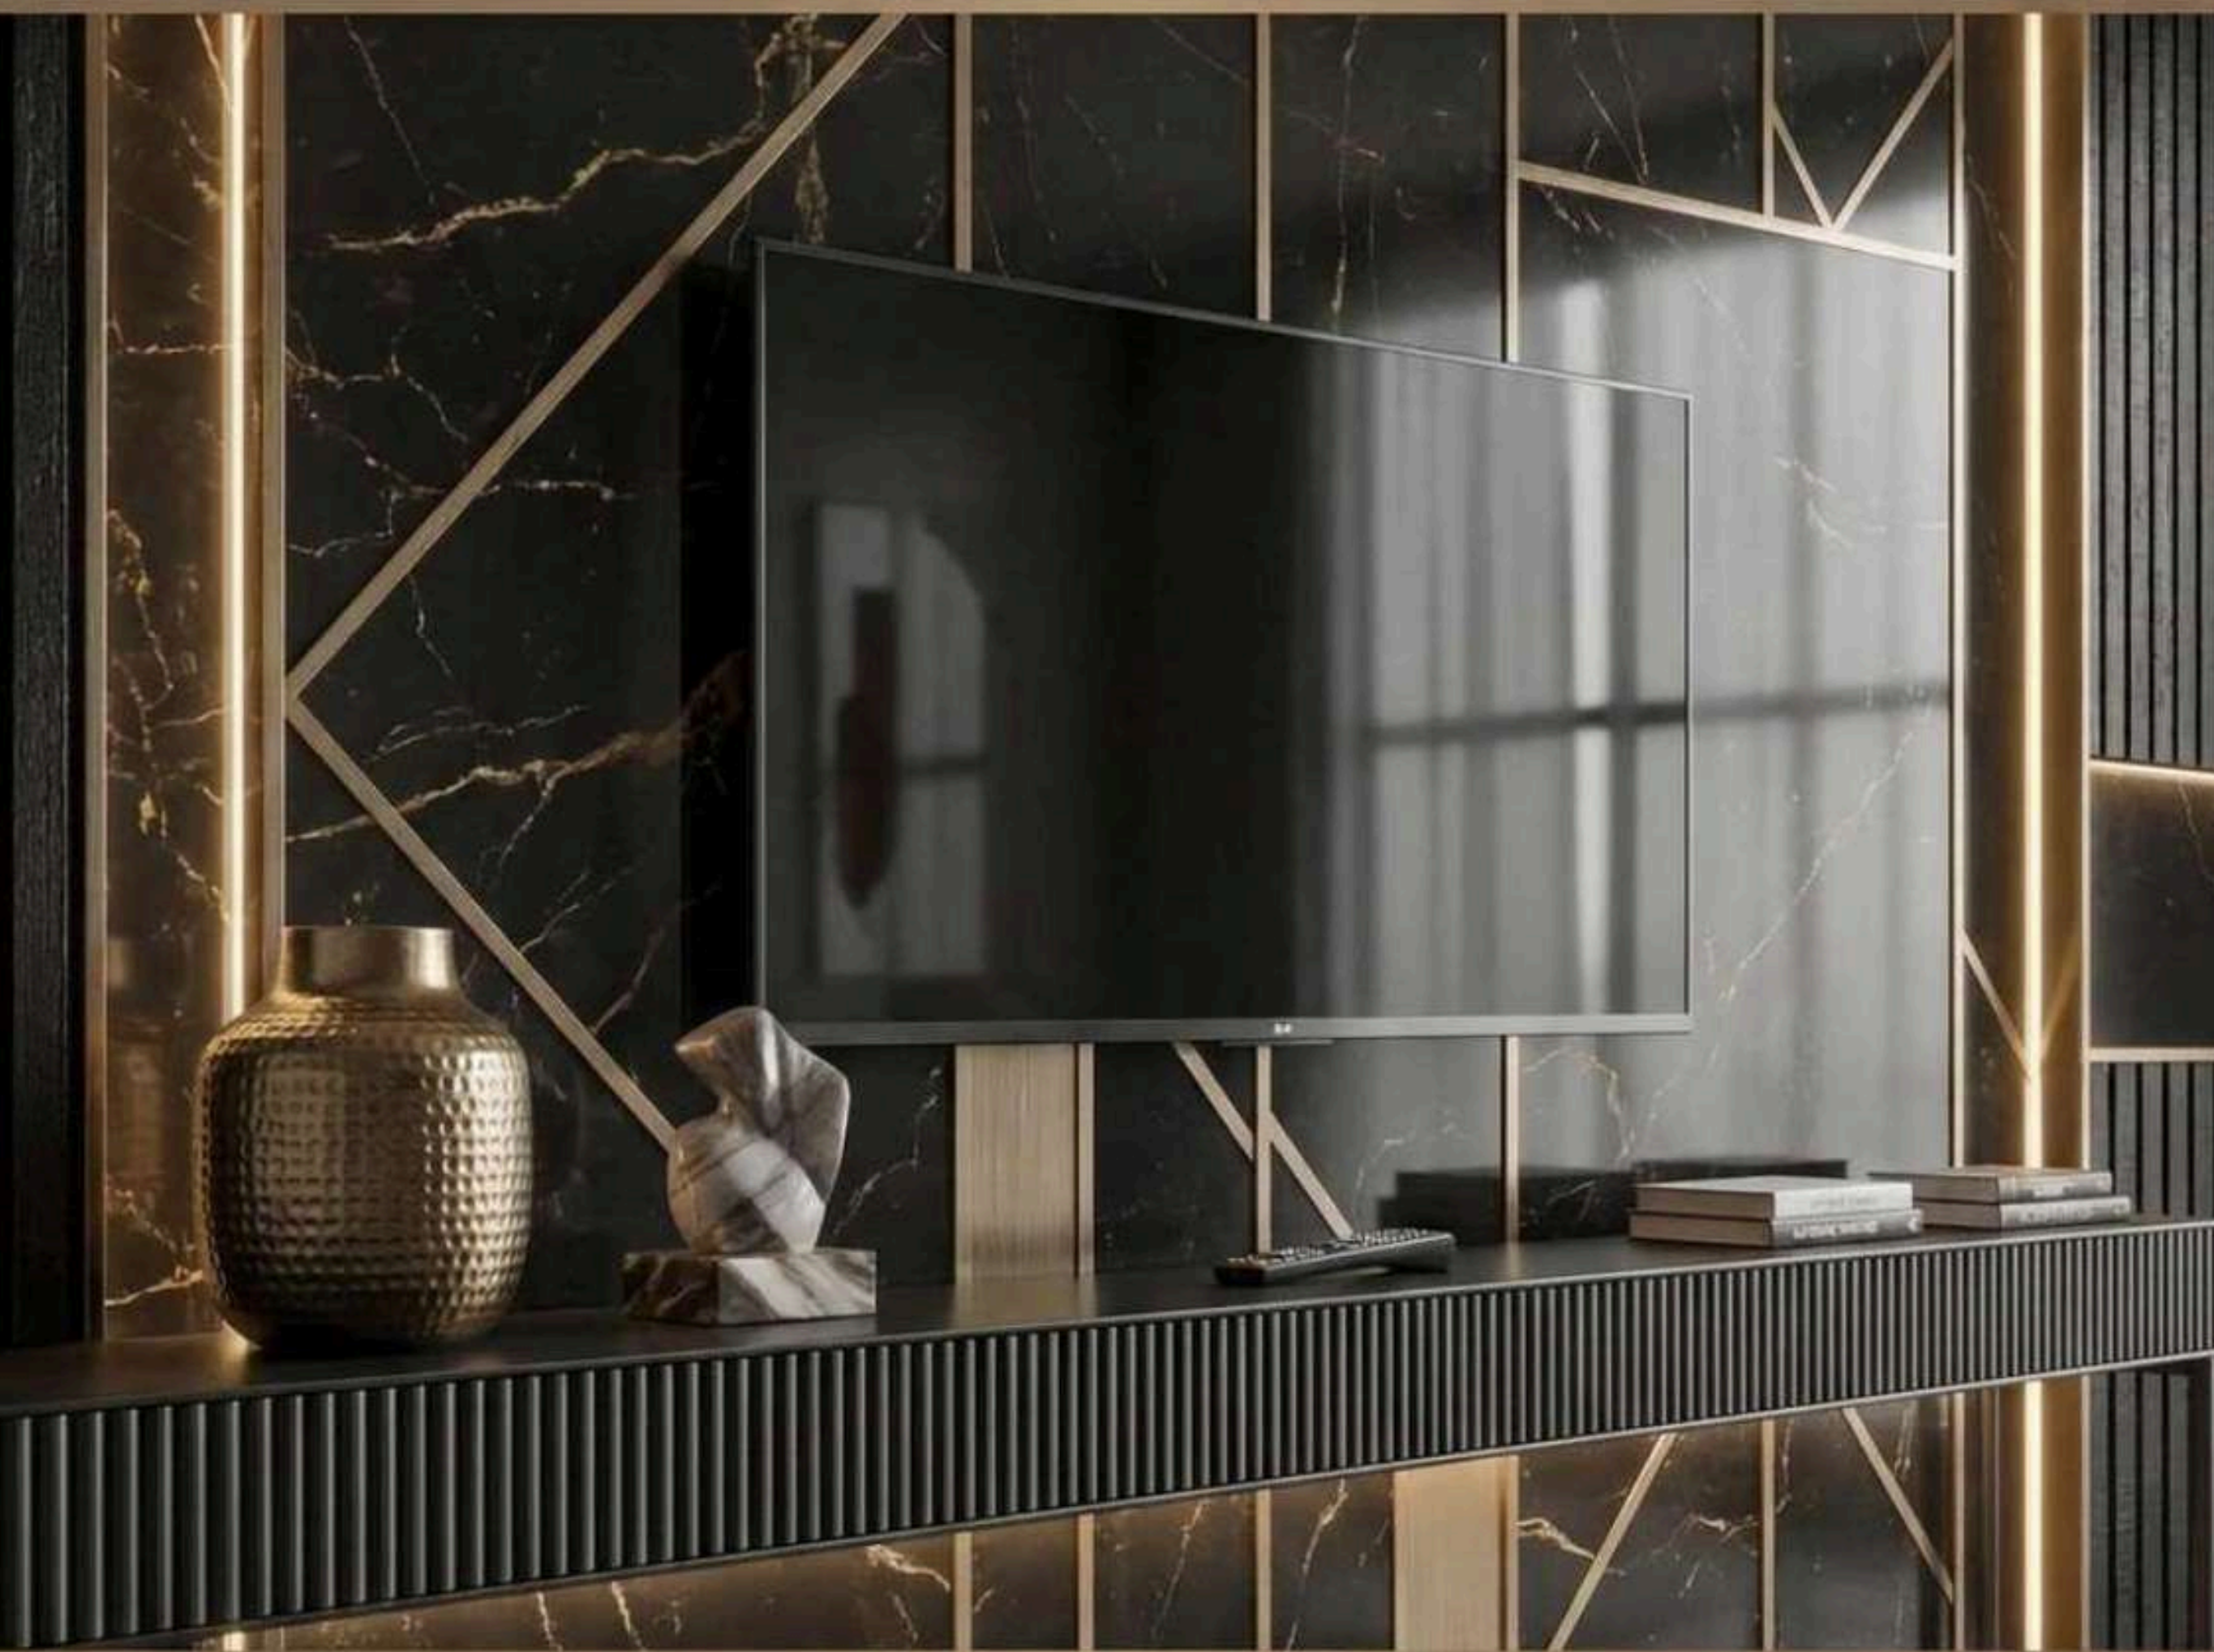

CATÁLOGO DIGITAL | EDIÇÃO PREMIUM

PROJETO 01

PAINEL DE TV MONOLÍTICO EM PORCELANATO CALACATTA COM DETALHE RIPADO E ILUMINAÇÃO INTEGRADA



ESPECIFICAÇÕES TÉCNICAS DO PROJETO

Estilo do Projeto
Contemporâneo Luxuoso e Integrado

Tipo de Porcelanato
Marmorizado de Aparência Calacatta (Branco/Cinza) – Grandes Formatos

Técnica de Corte
Execução de Grandes Formatos, Cortes em 45° e Acabamento Retificado

Aplicação
Painel de TV (Parede), Rack Suspenso e Piso (Área Social)


MATERIAIS E ACABAMENTOS

- Porcelanato Calacatta Polido Retificado (Grandes Formatos 120x270 cm)
- Ripado em MDF Amadeirado (Freijó ou Nogueira)
- Fita de LED 3000K embutida no ripado e no sancão de gesso
- Spot de LED 3000K no sancão
- Rack suspenso em MDF com frente de gaveta porcelanato
- Perfil de alumínio para acabamento
- Cola e argamassa específica para grandes formatos
- Rejunte epóxi na cor do porcelanato


PLANTA BAIXA
ESCALA 1:20




VISTA FRONTAL
ESCALA 1:20

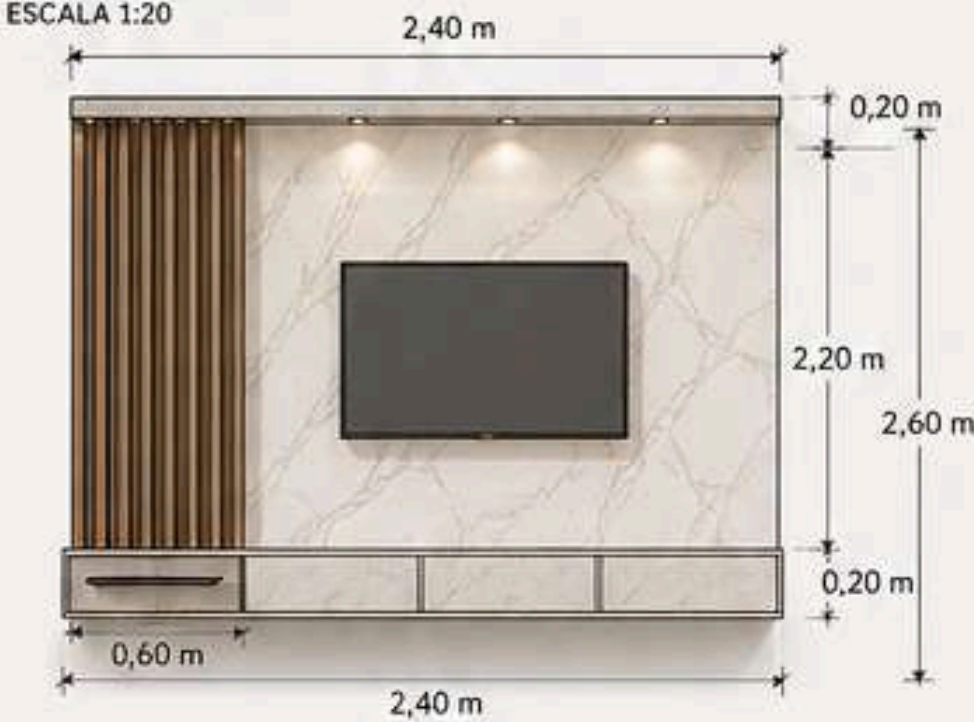


VISTA LATERAL
ESCALA 1:20

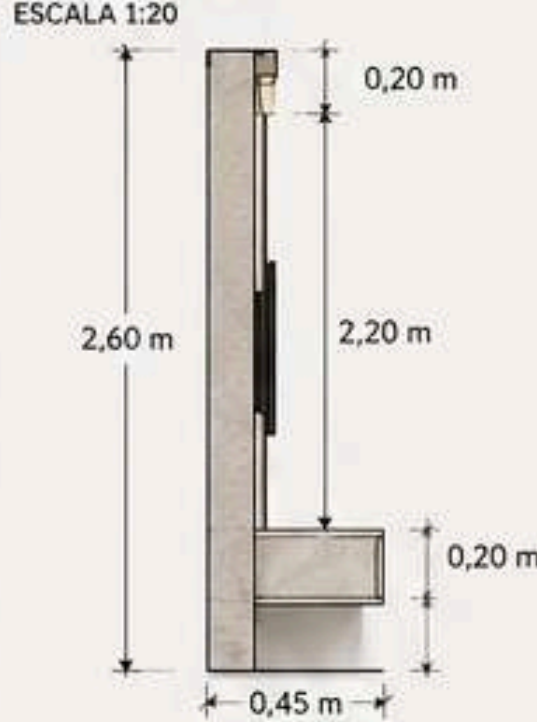


DETALHE RIPADO COM ILUMINAÇÃO
ESCALA 1:10

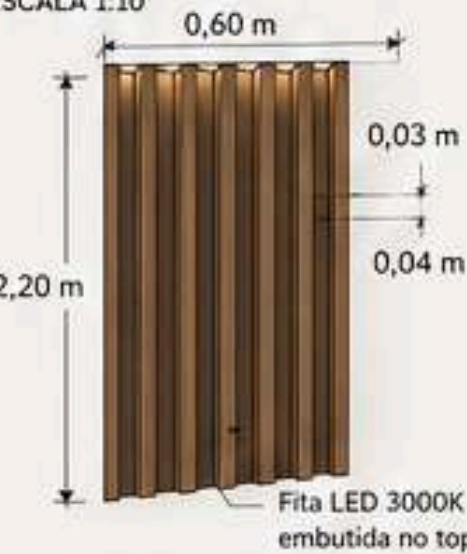


DETALHE PAINEL EM PORCELANATO CALACATTA
ESCALA 1:10

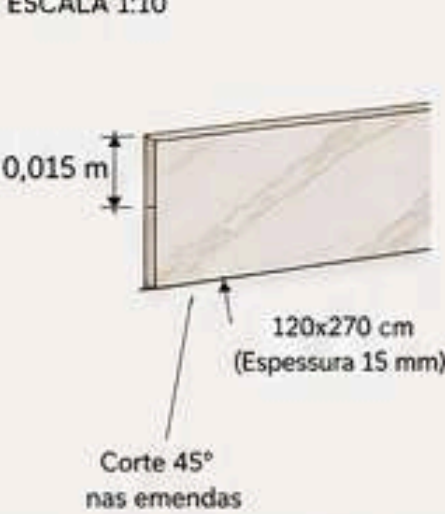


DETALHE RACK SUSPENSO
ESCALA 1:10

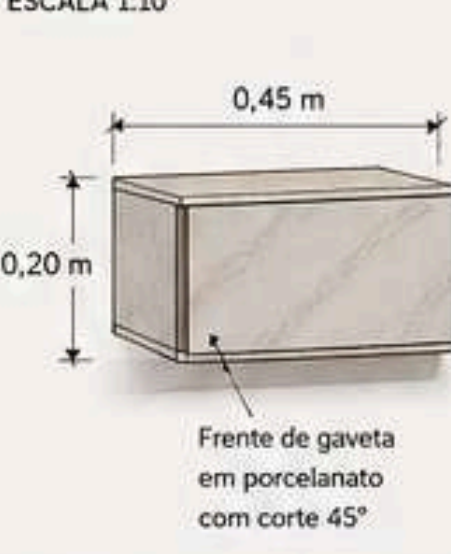

CORTE TRANSVERSAL (PAREDE)
ESCALA 1:10

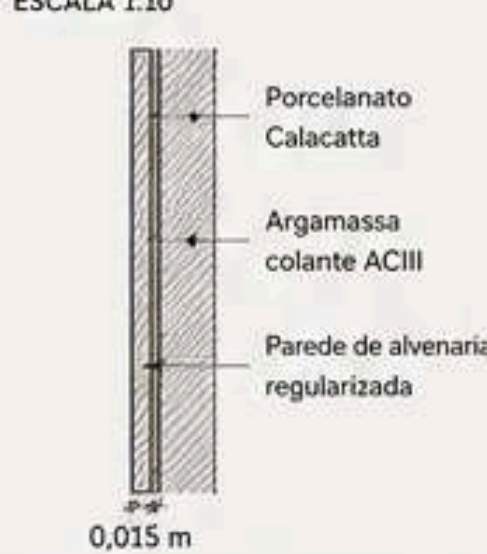

CORTE LONGITUDINAL (RACK)
ESCALA 1:10

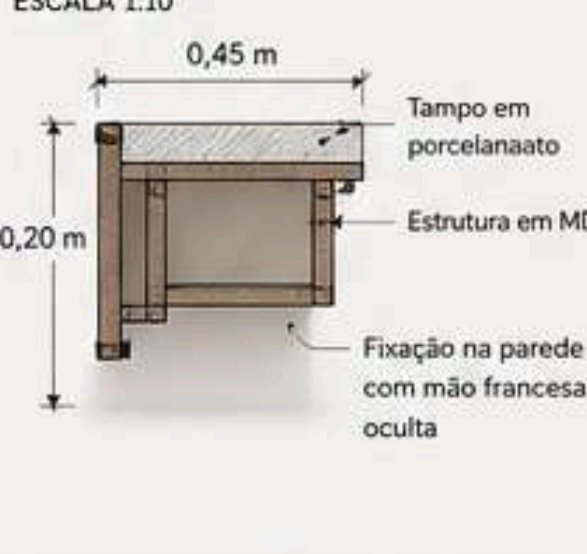

MEDIDAS E DISTÂNCIAS TÉCNICAS

- Altura total do painel (do piso ao sancão): 2,60 m
- Altura do painel em porcelanato: 2,20 m
- Largura total do painel: 2,40 m
- Largura do ripado: 0,60 m
- Profundidade do rack suspenso: 0,45 m
- Altura do rack suspenso: 0,20 m
- Altura do sancão rebaixado: 0,20 m
- Profundidade do sancão: 0,20 m
- Espaçamento entre ripas: 0,04 m
- Largura da ripa: 0,03 m
- Distância do piso ao rack: 0,20 m (vão livre)
- Centralização da TV: eixo a 1,20 m do piso (centro da tela)

SUGESTÃO DE METAIS E ACESSÓRIOS



ILUMINAÇÃO




PASSO A PASSO DE EXECUÇÃO

- 1 Marcação da parede e verificação do esquadro e nivelamento.
- 2 Regularização da parede para receber grandes formatos.
- 3 Instalação das placas de porcelanato com argamassa ACIII.
- 4 Aplicação de sistema de nivelamento (clips e cunhas).
- 5 Rejuntamento epóxi após 72h da instalação.
- 6 Instalação do ripado com fixação oculta e fita LED no topo.
- 7 Execução do sancão com instalação de spots LED.
- 8 Instalação do rack suspenso com suportes ocultos.
- 9 Limpeza final e conferência dos acabamentos.

PROJETO 02

PAINEL ARQUITETÔNICO EM PORCELANATO COM VEIOS DOURADOS, DETALHES RIPADOS SIMÉTRICOS E ILUMINAÇÃO CÊNICA

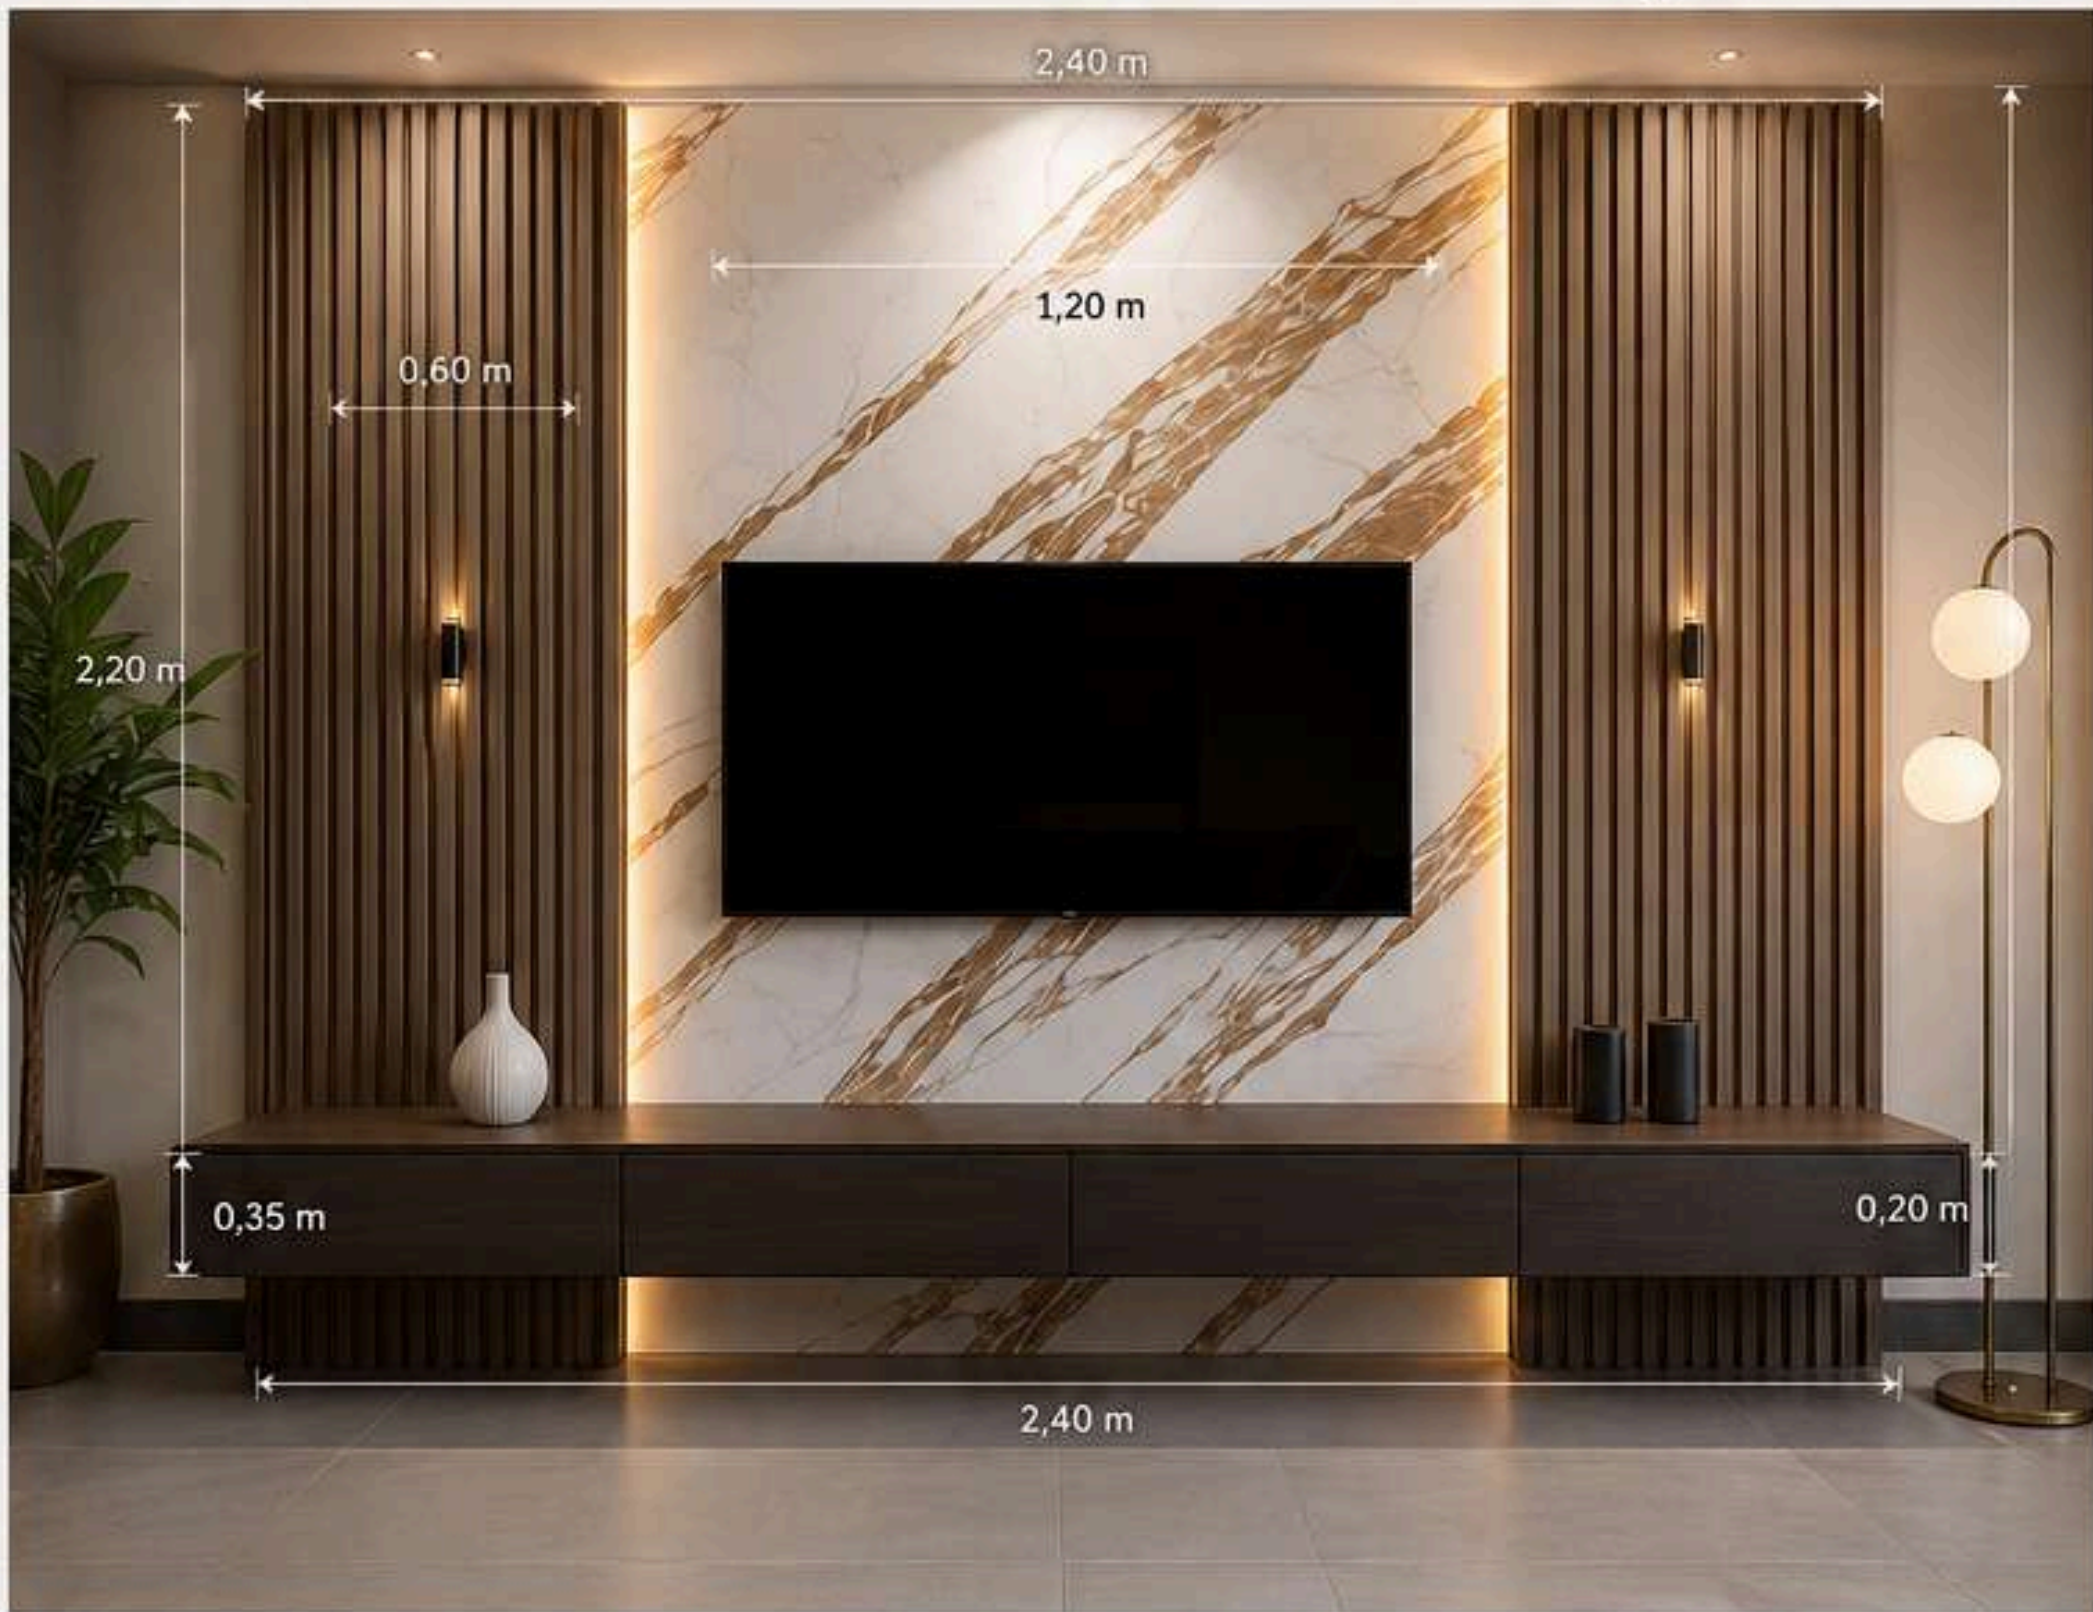

ESPECIFICAÇÕES TÉCNICAS DO PROJETO

Estilo do Projeto
Contemporâneo Luxuoso e Simétrico

Tipo de Porcelanato
Marmorizado com Veios DOURADOS e BRONZE (Aparência Calacatta Gold)
Grandes Formatos


Técnica de Corte
Execução de Grandes Formatos, Cortes em 45° e Acabamento Retificado

Aplicação
Painel de TV (Parede), Rack Suspenso e Piso de Madeira (Área Social)


MATERIAIS E ACABAMENTOS

- Porcelanato Calacatta Gold Polido Retificado (Painel Central)
- Ripado de MDF Amadeirado (Freijó ou Nogueira)
- Fita de LED 3000K embutida nas laterais e no ripado
- Arandela vertical LED dourada
- Rack suspenso em MDF com acabamento amadeirado
- Pintura acrílica fosca nas laterais
- Rodapé embutido ou invisível


PLANTA BAIXA
ESCALA 1:20

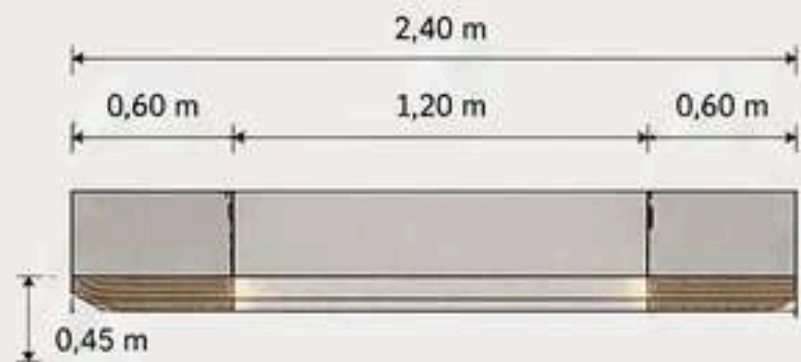


VISTA FRONTAL
ESCALA 1:20

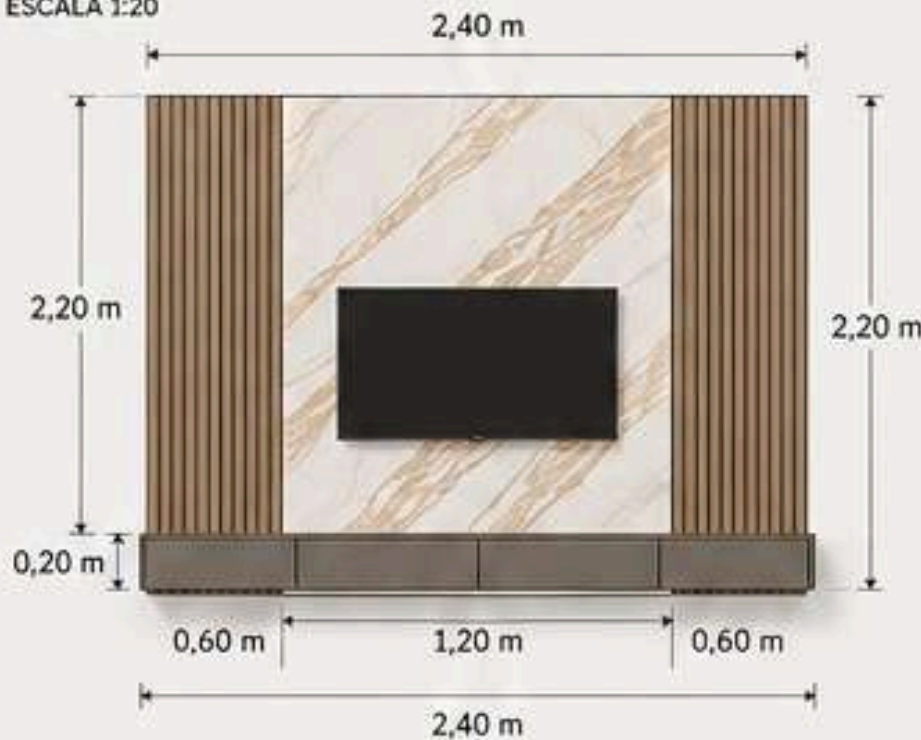

VISTA LATERAL
ESCALA 1:20

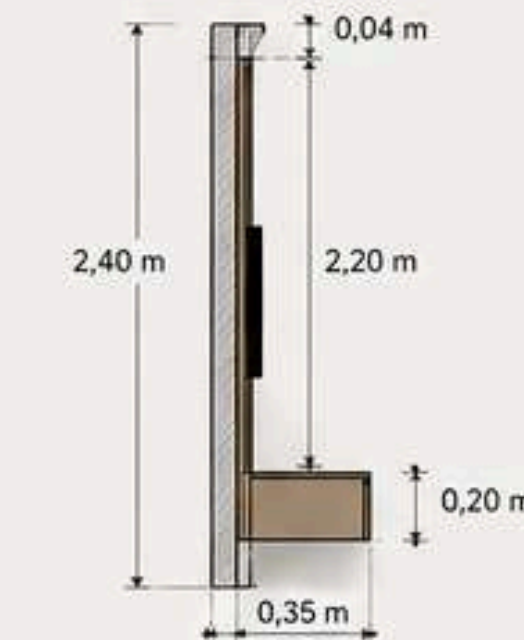


DETALHE RIPADO LATERAL
ESCALA 1:5

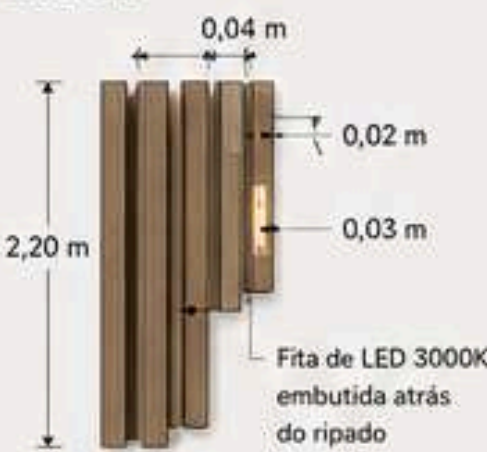

DETALHE PAINEL CENTRAL
ESCALA 1:5




CORTE TRANSVERSAL (PAINEL)
ESCALA 1:5

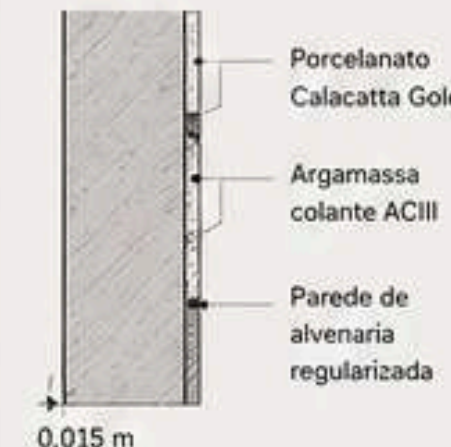

DETALHE ILUMINAÇÃO CÊNICA
ESCALA 1:5



CORTE LONGITUDINAL (RACK)
ESCALA 1:5

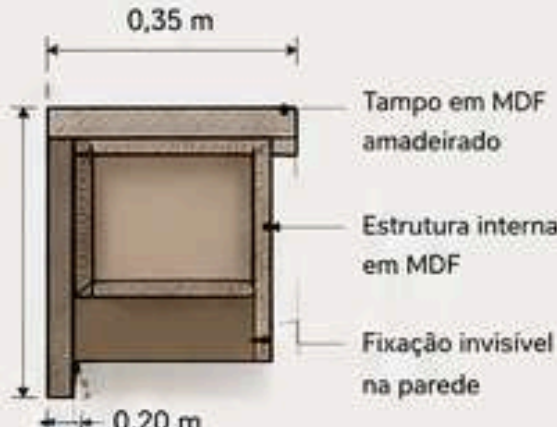

MEDIDAS E DISTÂNCIAS TÉCNICAS

- Altura total do painel (do piso ao teto): 2,40 m
- Altura do painel de porcelanato central: 2,20 m
- Largura total do painel: 2,40 m
- Largura do painel central: 1,20 m
- Largura de cada painel ripado: 0,60 m
- Profundidade do ripado: 0,03 m (com recuo de LED)
- Distância entre ripados: 0,02 m
- Altura do rack suspenso: 0,20 m
- Profundidade do rack: 0,35 m
- Distância do piso ao rack: 0,20 m (vão livre)
- Espaçamento entre rack e painel: 0,02 m (visual leve)

SUGESTÃO DE METAIS E ACESSÓRIOS



PASSO A PASSO DE EXECUÇÃO

- Marcação da parede e verificação de esquadro e nivelamento.
- Instalação das fitas de LED e preparação da fiação.
- Fixação do painel ripado nas laterais com parafusos ocultos.
- Instalação do porcelanato central com argamassa ACIII.
- Execução dos cortes em 45° nas bordas do porcelanato.
- Rejuntamento epôxi após 72h da instalação.
- Instalação do rack suspenso com suportes ocultos.
- Conexão elétrica e teste da iluminação.
- Limpeza final e conferência dos acabamentos.

PROJETO 03

PAINEL ARQUITETÔNICO EM PORCELANATO COM VEIOS DOURADOS E ILUMINAÇÃO SOBRE RIPADO



ESPECIFICAÇÕES TÉCNICAS DO PROJETO

Estilo do Projeto
Contemporâneo Sofisticado e Integrado

Tipo de Porcelanato
Marmorizado de Aparência Cinza com Veios Dourados (Gold)
Grandes Formatos

Técnica de Corte
Execução de Grandes Formatos, Cortes em 45° e Acabamento Retificado

Aplicação
Painel de TV (Parede), Detalhe de Ripado e Prateleiras Iluminadas (Área Social)


MATERIAIS E ACABAMENTOS

- Porcelanato Aparência Cinza com Veios Dourados (Gold) Retificado – Grande Formato
- Ripado em MDF Amadeirado (Freijó ou Nogueira)
- Fita de LED 3000K embutida no ripado e no nicho
- Prateleiras e Tampo em MDF amadeirado
- Rack suspenso com frentes em MDF laqueado
- Acabamento amadeirado fosco e toque suave
- Rodapé embutido ou invisível


PLANTA BAIXA
ESCALA 1:20




VISTA FRONTAL
ESCALA 1:20

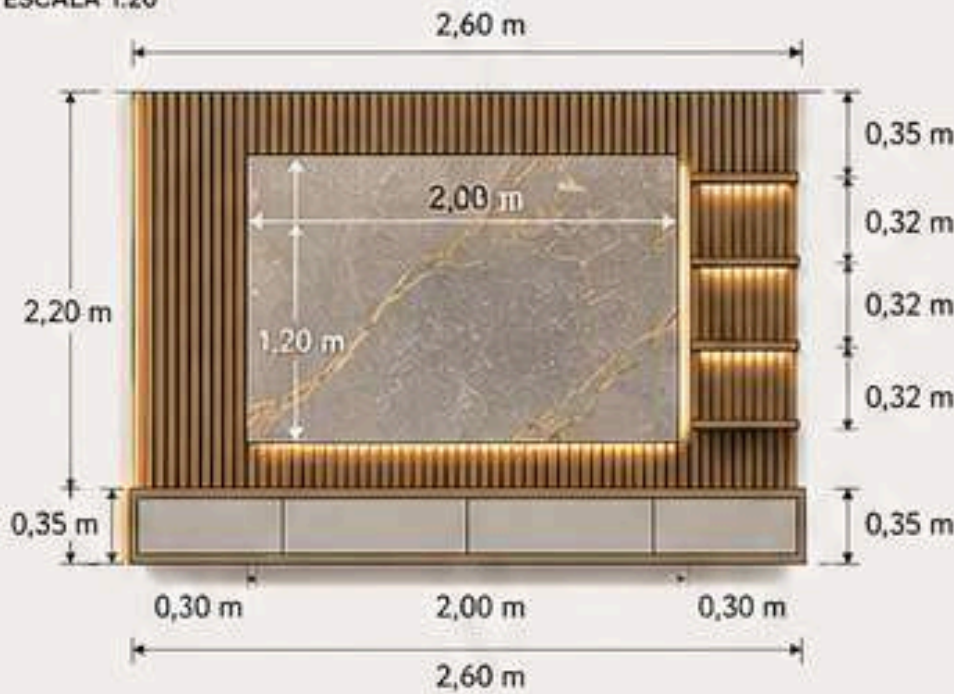


VISTA LATERAL
ESCALA 1:20

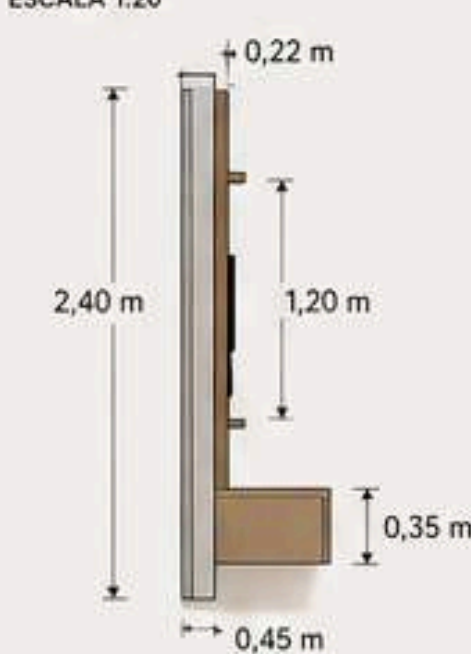

DETALHE PAINEL CENTRAL
ESCALA 1:10

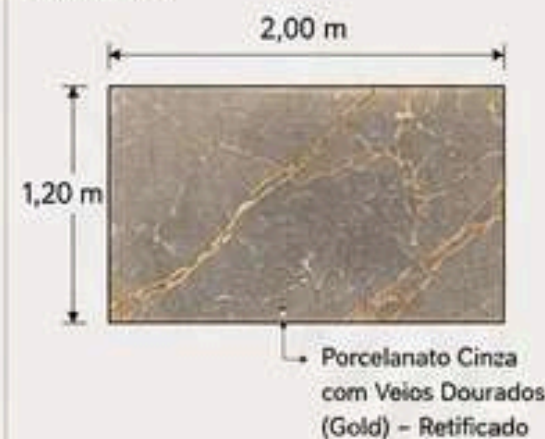

DETALHE RIPADO
ESCALA 1:10

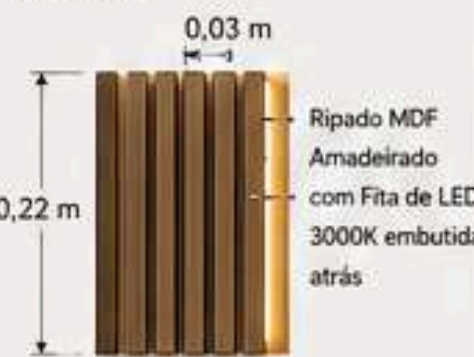


DETALHE PRATELEIRAS LATERAIS
ESCALA 1:10



CORTE TRANSVERSAL (PAINEL)
ESCALA 1:10



PASSO LONGITUDINAL (PRATELEIRA)
ESCALA 1:10

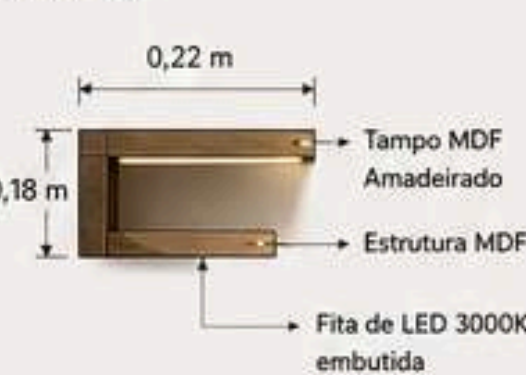

MEDIDAS E DISTÂNCIAS TÉCNICAS

- Altura total do painel (do piso ao teto): 2,40 m
- Altura do painel em porcelanato central: 1,20 m
- Largura total do painel: 2,60 m
- Largura do painel central em porcelanato: 2,00 m
- Profundidade total do painel: 0,22 m
- Profundidade do rack suspenso: 0,45 m
- Altura do rack suspenso: 0,35 m
- Altura das prateleiras laterais: 0,32 m (cada nicho)
- Largura das prateleiras laterais: 0,40 m
- Distância entre ripados (vão livre): 0,02 m
- Espaçamento entre painel central e ripado: 0,02 m (luz de LED)
- Distância do centro da TV ao piso: 1,20 m

SUGESTÃO DE METAIS E ACESSÓRIOS



ILUMINAÇÃO



PASSO A PASSO DE EXECUÇÃO

- Marcação do painel na parede e verificação de esquadro e nivelamento.
- Instalação das fitas de LED e passagem da fiação elétrica.
- Fixação do ripado em MDF na parede com cola e parafusos ocultos.
- Instalação do porcelanato central com argamassa ACIII e niveladores.
- Aplicação de juntas bem alinhadas e acabamento em 45° nas bordas.
- Fixação das prateleiras laterais e testes da iluminação embutida.
- Instalação do rack suspenso com suportes ocultos.
- Conexão elétrica e testes da iluminação.
- Limpeza final e conferência dos acabamentos.

PROJETO 04

PAINEL DE TV EM PORCELANATO NERO MARMORIZADO COM DETALHE RIPADO E ILUMINAÇÃO DE DESTAQUE



ESPECIFICAÇÕES TÉCNICAS DO PROJETO

Estilo do Projeto
Contemporâneo Luxuoso e Tecnológico

Tipo de Porcelanato
Marmorizado de Aparência Nero (Preto/Branco) Grandes Formatos

Técnica de Corte
Execução de Grandes Formatos, Cortes em 45° e Acabamento Retificado

Aplicação
Painel de TV (Parede), Rack Suspenso e Piso (Área Social)

MATERIAIS E ACABAMENTOS

- Porcelanato Aparência Nero Polido (Grande Formato)
- Ripado em MDF Amadeirado (Freijó ou Nogueira)
- Fita de LED 3000K embutida nas laterais e no nicho superior
- Prateleiras em MDF Amadeirado com iluminação inferior
- Rack suspenso em MDF com frentes em MDF laqueado preto fosco
- Acabamento amadeirado fosco e toque suave
- Rodapé embutido ou invisível


PLANTA BAIXA

ESCALA 1:20




VISTA FRONTAL

ESCALA 1:20

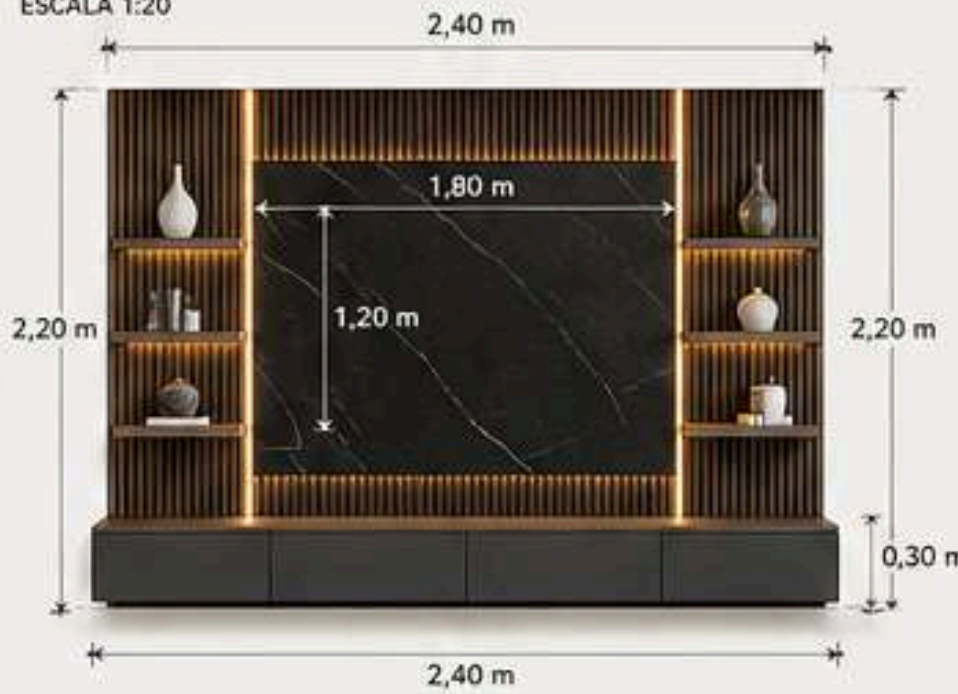


VISTA LATERAL

ESCALA 1:20

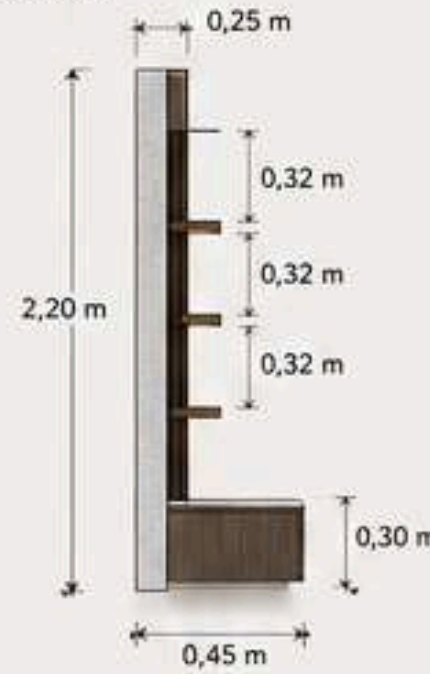


DETALHE PAINEL CENTRAL (NERO)

ESCALA 1:10

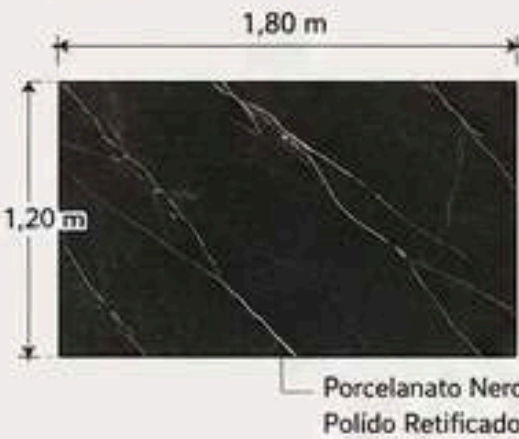

DETALHE RIPADO (LATERAL)

ESCALA 1:10

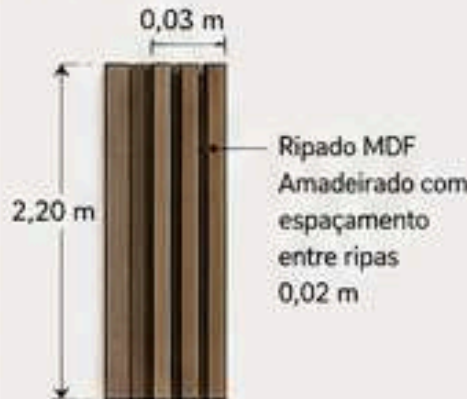


DETALHE PRATELEIRAS

ESCALA 1:10



DETALHE ILUMINAÇÃO

ESCALA 1:10

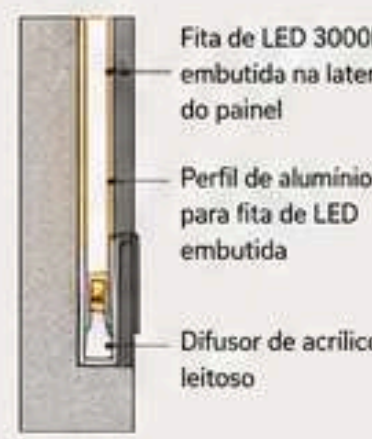

CORTE RACK SUSPENSO

ESCALA 1:10



MEDIDAS E DISTÂNCIAS TÉCNICAS

- Altura total do painel (do piso ao teto): 2,20 m
- Largura total do painel: 2,40 m
- Largura do painel central (Nero): 1,80 m
- Altura do painel central (Nero): 1,20 m
- Profundidade total do painel com prateleiras: 0,25 m
- Profundidade do rack suspenso: 0,45 m
- Altura do rack suspenso: 0,30 m
- Distância entre prateleiras: 0,32 m
- Profundidade das prateleiras: 0,25 m
- Espaçamento entre ripas: 0,02 m
- Distância do piso ao rack: 0,20 m (vão livre)
- Iluminação LED 3000K com difusor para efeito contínuo

SUGESTÃO DE METAIS E ACESSÓRIOS



ILUMINAÇÃO



PASSO A PASSO DE EXECUÇÃO

- Marcação da parede e verificação de esquadro e nivelamento.
- Instalação da estrutura de fixação do painel e prateleiras.
- Fixação das ripas de MDF com espaçadores para alinhamento.
- Instalação do porcelanato Nero retificado (cortes em 45°).
- Embutimento dos perfis e fitas de LED nas laterais e nichos.
- Fixação das prateleiras com iluminação inferior.
- Instalação do rack suspenso e ajustes de alinhamento.
- Conexão elétrica e testes da iluminação.
- Limpeza final e conferência dos acabamentos.

PROJETO 06

BANCADA E PAINEL MONOLÍTICO CALACATTA COM NICHOS INTEGRADOS E CONTINUIDADE NO PISO



ESPECIFICAÇÕES TÉCNICAS DO PROJETO

Estilo do Projeto
Contemporâneo Minimalista e Monolítico

Tipo de Porcelanato
Marmorizado Calacatta Grandes Formatos (Branco/Cinza) e Piso Acetinado

Técnica de Corte
Cortes em 45° (Meia Esquadria) e Acabamento Retificado

Aplicação
Bancada e Painel Monolítico (Sala de TV), Piso Social

MATERIAIS E ACABAMENTOS

- Porcelanato Calacatta Retificado (Grandes Formatos)
- Ripado em MDF Amadeirado (Pintura ou BP)
- Fita de LED 3000K embutida no rasgo vertical e nos nichos
- Nichos integrados com acabamento no mesmo porcelanato
- Ponto de tomada e passa cabos embutidos nos nichos
- Rejunte epóxi na cor do porcelanato
- Acabamento acetinado no piso com continuidade


PLANTA BAIXA

ESCALA 1:20




VISTA FRONTAL

ESCALA 1:20

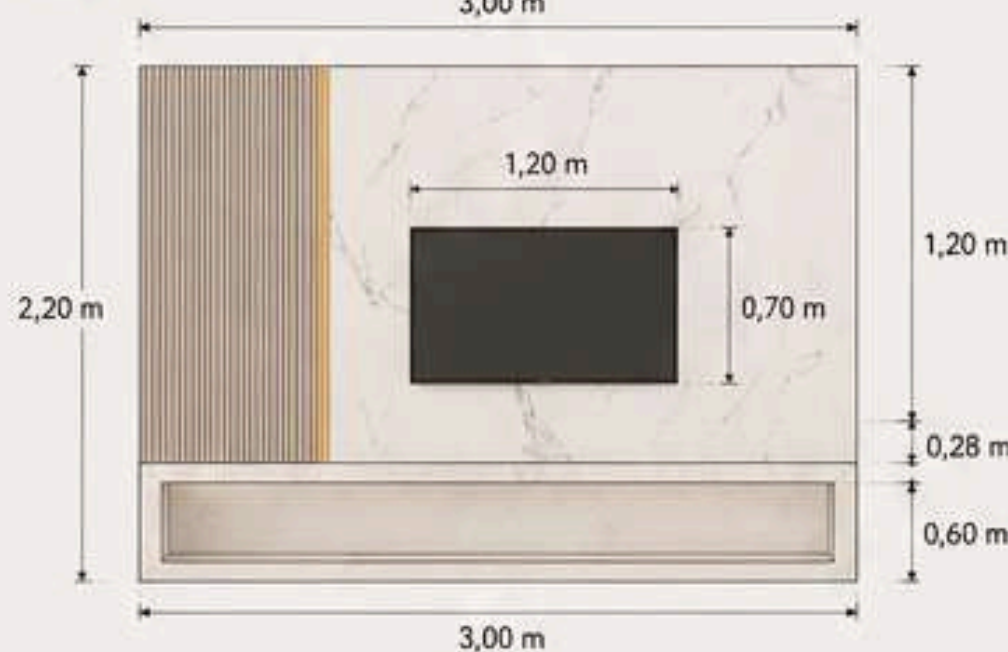

VISTA LATERAL

ESCALA 1:20

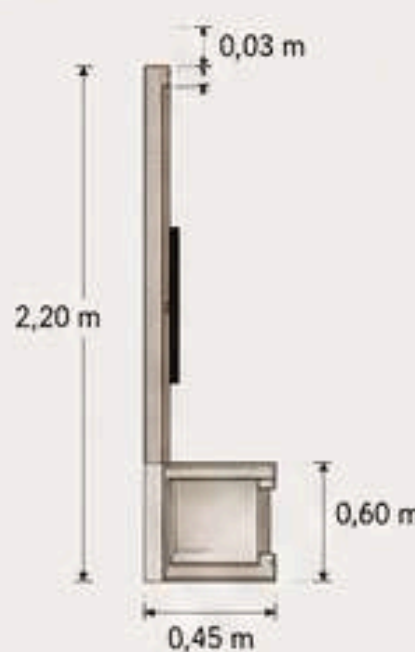


DETALHE NICHOS INTEGRADOS

ESCALA 1:10



DETALHE ENCONTRO 45° (MEIA ESQUADRIA)

ESCALA 1:5

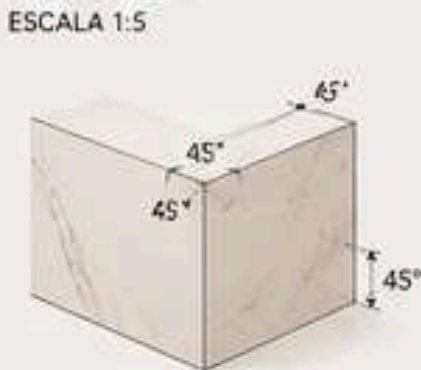


DETALHE PAINEL RIPADO COM ILUMINAÇÃO

ESCALA 1:10




CORTE TRANSVERSAL (PAINEL E BANCADA)

ESCALA 1:10

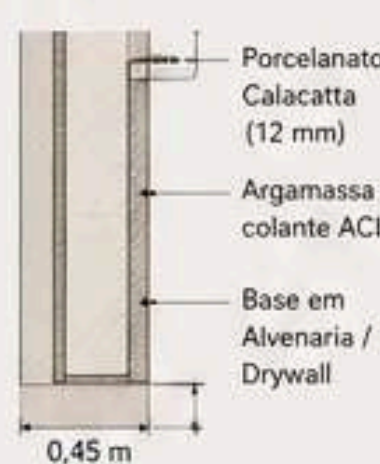

PASSO A PASSO LONGITUDINAL (BANCADA)

ESCALA 1:10

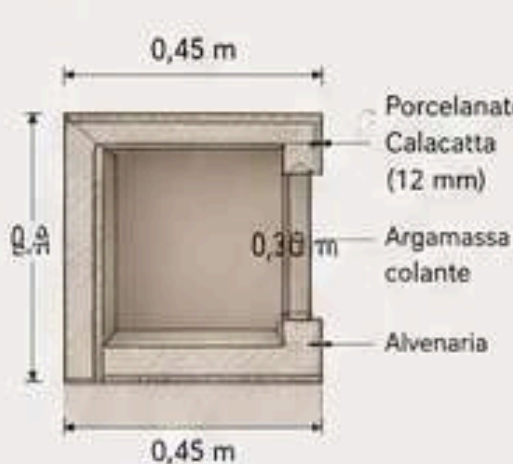

MEDIDAS E DISTÂNCIAS TÉCNICAS

- Altura total do painel (do piso ao teto): 2,20 m
- Largura total do painel e bancada: 3,00 m
- Largura da área ripada: 0,80 m
- Largura da área do painel liso: 2,20 m
- Altura da bancada: 0,60 m
- Profundidade da bancada: 0,45 m
- Altura do nicho: 0,28 m
- Profundidade útil do nicho: 0,15 m
- Altura do painel liso (até o teto): 2,20 m
- Distância do centro da TV ao piso: 1,10 m
- Espaçamento entre ripado e painel liso: 0,02 m (com LED)

SUGESTÃO DE METAIS E ACESSÓRIOS




ILUMINAÇÃO



PASSO A PASSO DE EXECUÇÃO

- Marcação e conferência de esquadro e nivelamento do painel.
- Instalação da estrutura de fixação do painel e da bancada.
- Fixação das chapas de porcelanato com argamassa ACIII.
- Execução dos cortes em 45° nas bordas e encontros.
- Instalação do ripado e do rasgo vertical com LED embutida.
- Execução da bancada monolítica com nicho integrado.
- Instalação das tomadas e passa cabos embutidos no nicho.
- Instalação da fita de LED 3000K nos rasgos e nichos.
- Verificação geral de alinhamento e acabamento.
- Limpeza final e conferência dos acabamentos.

PAINEL ARQUITETÔNICO MONOLÍTICO EM PORCELANATO CALACATTA COM RIPADO DE MADEIRA E CRISTALEIRA INTEGRADA

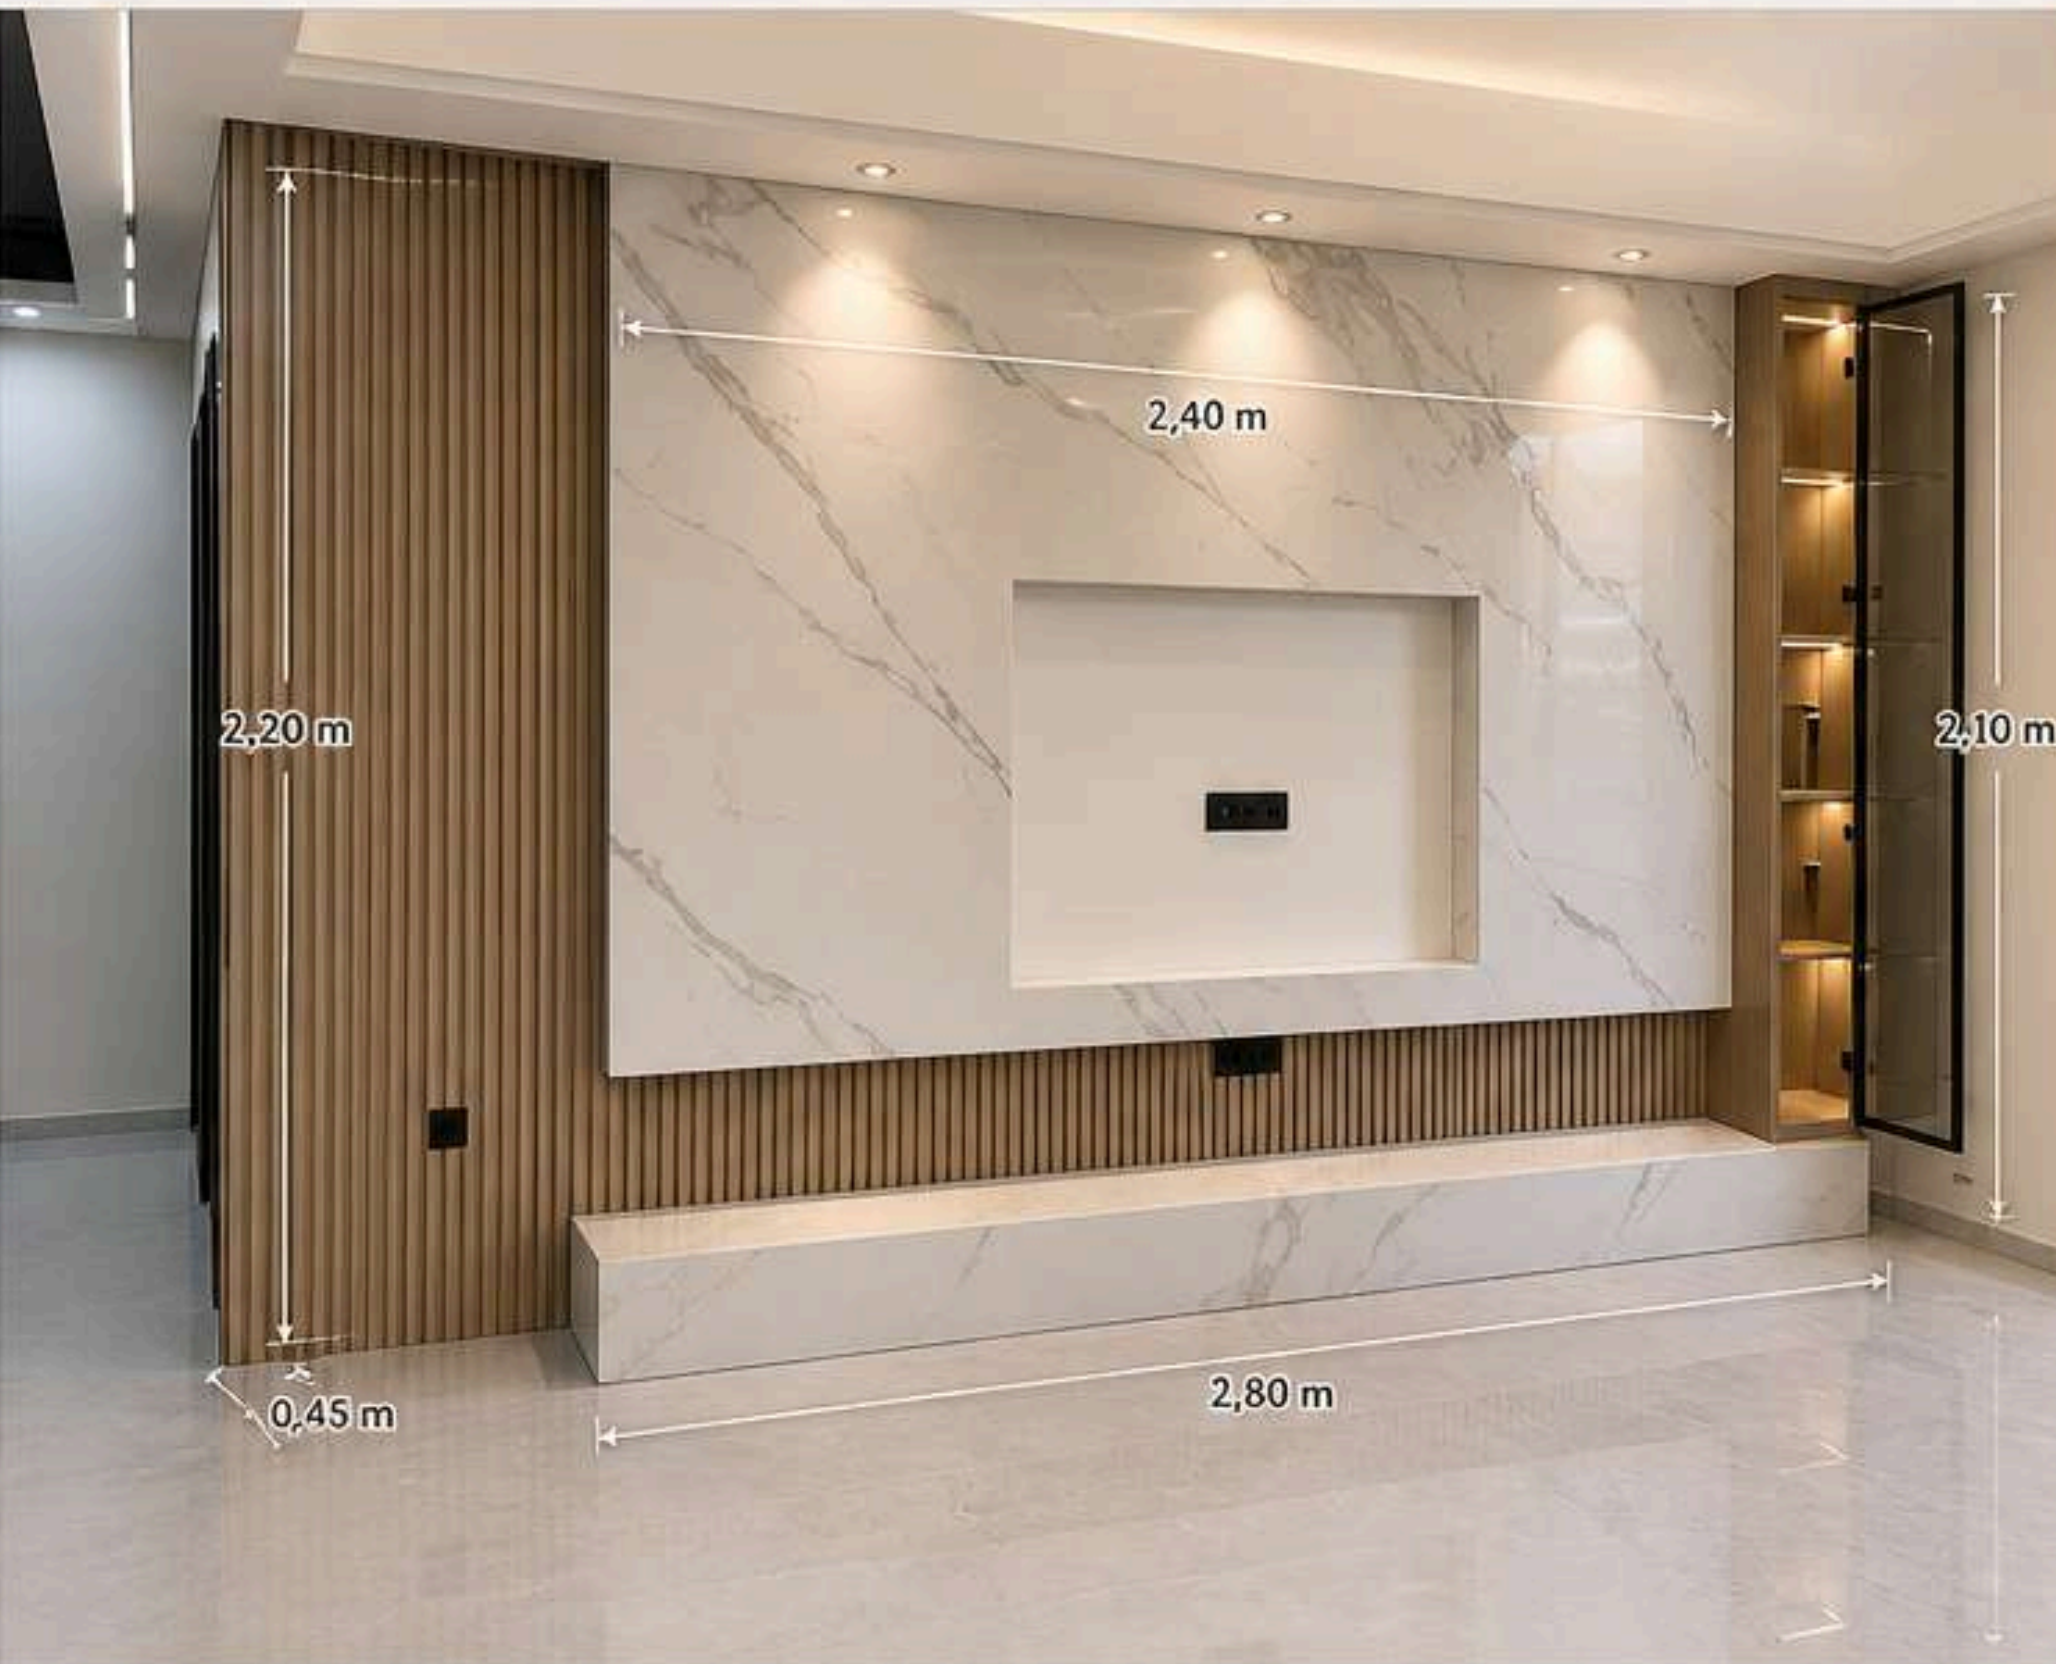

ESPECIFICAÇÕES TÉCNICAS DO PROJETO

Estilo do Projeto

Contemporâneo Luxuoso e Minimalista

Tipo de Porcelanato

Marmorizado de Aparência Calacatta (Branco/Cinza) Grandes Formatos e Piso Marmorizado Polido Cinza

Técnica de Corte

Execução de Grandes Formatos, Cortes em 45° (Meia Esquadria) e Acabamento Retificado

Aplicação

Painel de TV (Parede), Base de Rack e Piso (Área Social)

MATERIAIS E ACABAMENTOS

- Porcelanato Calacatta Polido Retificado (Grandes Formatos)
- Ripado de MDF Amadeirado (Pintura ou BP)
- Cristaleira com perfis de alumínio preto e vidro fumê temperado
- Fita de LED 3000K embutida no ripado, nicho e cristaleira
- Tomada e passa cabos embutidos
- Rejunte epóxi na cor do porcelanato
- Acabamento de rodapé embutido com continuidade


PLANTA BAIXA

ESCALA 1:20




VISTA FRONTAL

ESCALA 1:20

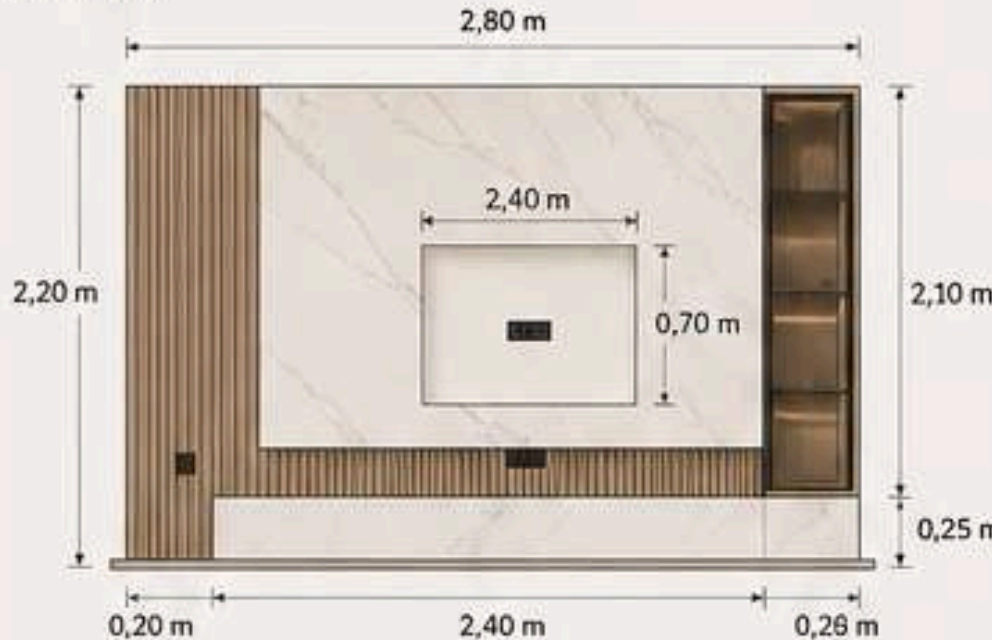

VISTA LATERAL

ESCALA 1:10

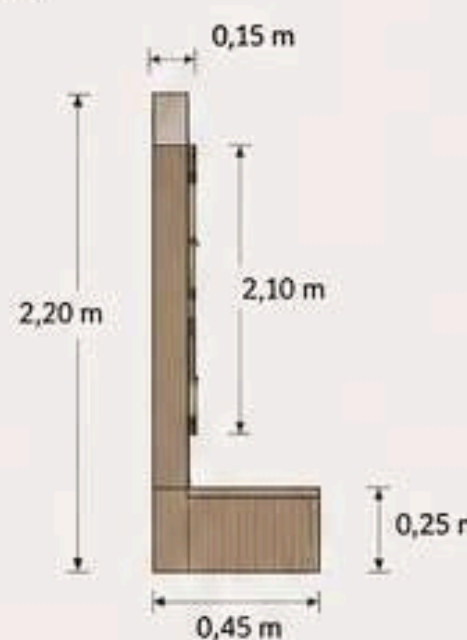

DETALHE RIPADO DE MADEIRA

ESCALA 1:10



DETALHE ENCONTRO 45° (MEIA ESQUADRIA)

ESCALA 1:10



DETALHE NICHU CENTRAL

ESCALA 1:10



CORTE TRANSVERSAL (PAINEL)

ESCALA 1:10



DETALHE CRISTALEIRA

ESCALA 1:10




MEDIDAS E DISTÂNCIAS TÉCNICAS

- Altura total do painel (do piso ao teto): 2,20 m
- Largura total do painel e bancada: 2,80 m
- Largura da área do painel: 2,40 m
- Altura da área do painel: 2,10 m
- Profundidade do nicho: 0,15 m
- Distância entre ripados: 0,02 m (vão livre)
- Largura do ripado: 0,03 m
- Espaçamento entre painel e piso (sombra): 0,02 m com fita de LED 3000K embutida

SUGESTÃO DE METAIS E ACESSÓRIOS



ILUMINAÇÃO

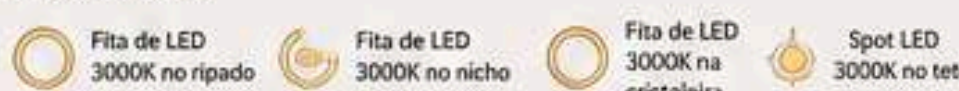

PASSO A PASSO DE EXECUÇÃO

- Marcação da parede e verificação de esquadro e nivelamento.
- Execução da alvenaria e regularização da parede.
- Instalação das fitas de LED e passa cabos nos pontos definidos.
- Fixação dos painéis de porcelanato com argamassa ACIII.
- Execução dos cortes em 45° nas bordas do painel e nicho.
- Instalação do ripado de MDF com iluminação embutida.
- Instalação do nicho central com acabamento interno.
- Instalação da cristaleira e ajustes das prateleiras de vidro.
- Execução da base (bancada) em porcelanato com acabamento 45°.
- Limpeza final e conferência dos acabamentos.

PROJETO 08

PAINEL DE TV FLUTUANTE EM PORCELANATO CALACATTA COM NICHOS EMBUTIDOS E ILUMINAÇÃO DE LED INTEGRADA



ESPECIFICAÇÕES TÉCNICAS DO PROJETO

Estilo do Projeto
Minimalista Moderno e Integrado

Tipo de Porcelanato
Marmorizado de Aparência Calacatta Grandes Formatos (Branco/Cinza)

Técnica de Corte
Execução de Grandes Formatos, Cortes em 45° e Acabamento Retificado

Aplicação
Painel de TV (Parede), Nichos Embutidos, Rack Suspenso e Piso (Área Social)


MATERIAIS E ACABAMENTOS

- Porcelanato Calacatta Polido Retificado (Grandes Formatos)
- Ripado em MDF Amadeirado (Pintura ou BP)
- Fita de LED 3000K embutida na parte superior, inferior e laterais do painel e no nicho
- Nicho com pintura fosca cinza escuro
- Rack suspenso em MDF laqueado com frentes sem puxadores
- Cristaleira com perfis de alumínio preto e vidro fumê
- Tomada e passa cabos embutidos
- Rodapé embutido ou invisível


PLANTA BAIXA
ESCALA 1:20



VISTA FRONTAL
ESCALA 1:20

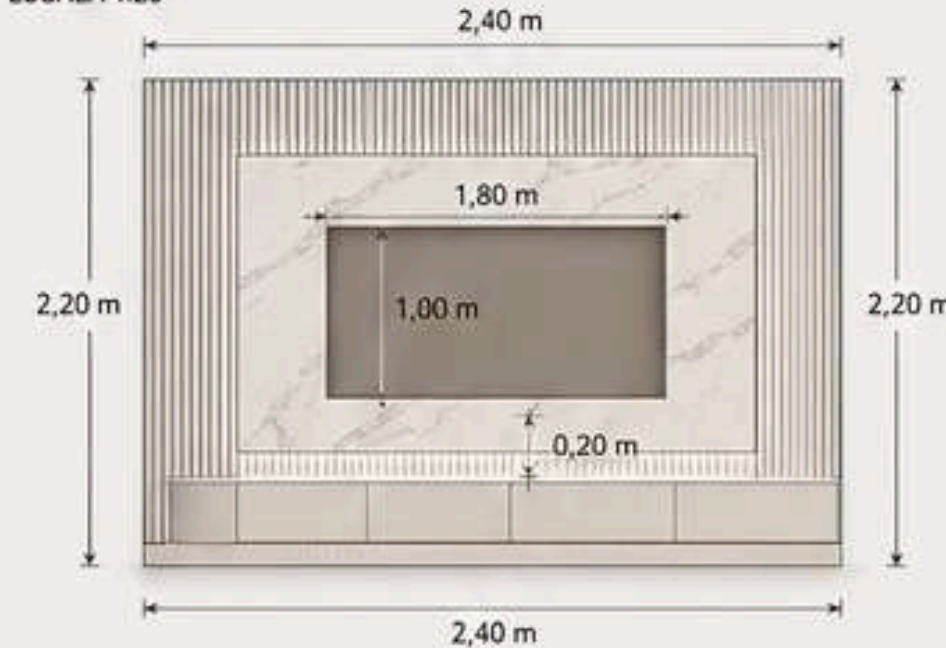

VISTA LATERAL
ESCALA 1:20

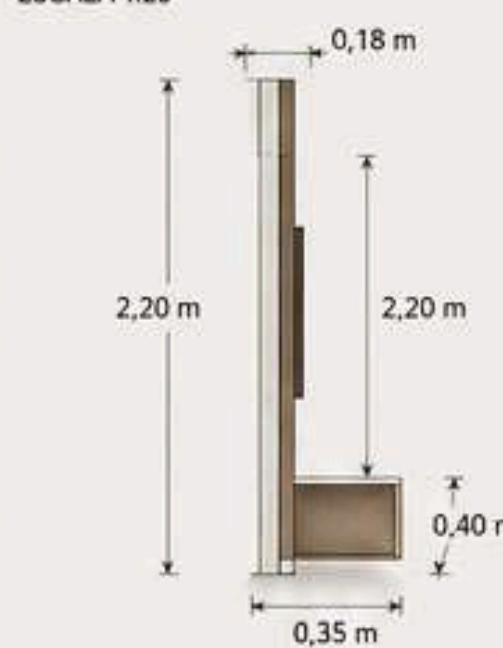

DETALHE RIPADO
ESCALA 1:10



DETALHE ENCONTRO 45° (MEIA ESQUADRIA)
ESCALA 1:5




DETALHE NICHOS
ESCALA 1:10



CORTE TRANSVERSAL (PAINEL)
ESCALA 1:10



PASSLHE CRISTALEIRA
ESCALA 1:10

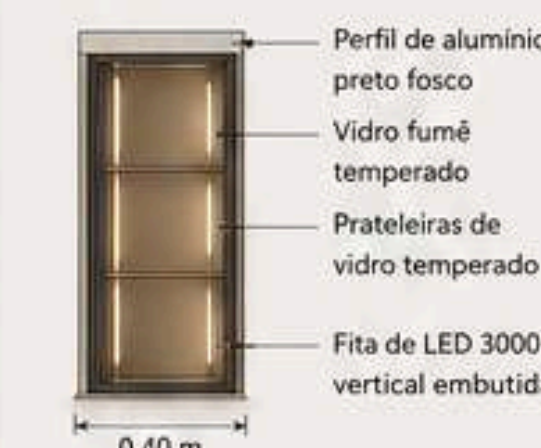


MEDIDAS E DISTÂNCIAS TÉCNICAS

- Altura total do painel (do piso ao teto): 2,20 m
- Largura total do painel: 2,40 m
- Largura do nicho para TV: 1,80 m
- Altura do nicho para TV: 1,00 m
- Profundidade do nicho: 0,18 m
- Profundidade da bancada: 0,40 m
- Altura da bancada: 0,20 m
- Distância do piso à parte inferior da bancada: 0,35 m
- Espaçamento entre ripado e painel (com LED): 0,02 m

SUGESTÃO DE METAIS E ACESSÓRIOS



ILUMINAÇÃO

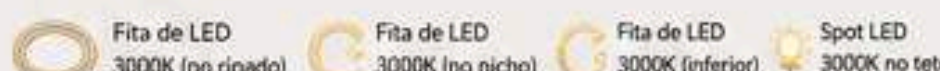

PASSO A PASSO DE EXECUÇÃO

- Marcação da parede e verificação de esquadro e nivelamento.
- Fixação da estrutura do painel e do nicho na parede.
- Execução do nicho de alvenaria e regularização interna.
- Instalação das fitas de LED e passagem da fiação elétrica.
- Fixação dos ripados em MDF com espaçadores para alinhamento.
- Assentamento do porcelanato Calacatta (cortes em 45°).
- Rejuntamento com epóxi na cor do porcelanato.
- Instalação da bancada e verificação do nível.
- Instalação da cristaleira e ajustes das prateleiras de vidro.
- Limpeza final e conferência dos acabamentos.

PROJETO 09

PAINEL DE TV EM PORCELANATO CALACATTA GOLD COM DETALHE RIPADO E RACK FLUTUANTE



ESPECIFICAÇÕES TÉCNICAS DO PROJETO

Estilo do Projeto
Contemporâneo Luxuoso e Aconchegante

Tipo de Porcelanato
Marmorizado Calacatta Gold Grandes Formatos (Branco/Ouro)
Ripado Marmorizado Cinza


Técnica de Corte
Meia Esquadria em 45° para Ripagem e Acabamento Retificado

Aplicação
Painel de TV (Parede),
Parede de Fundo (Ripado),
Mobiliário (Detalhamento do Rack),
Piso


MATERIAIS E ACABAMENTOS

- Porcelanato Calacatta Gold Retificado (Grandes Formatos)
- Ripado em MDF Amadeirado (Pintura ou BP)
- Fita de LED 3000K embutida atrás do porcelanato e no nicho do rack
- Nichos embutidos com vidro temperado fumê e perfis de alumínio preto fosco
- Prateleiras em vidro fumê temperado
- Rack suspenso em MDF laqueado off-white fosco
- Arandelas de parede com fecho duplo
- Acabamento de rodapé embutido


PLANTA BAIXA
ESCALA 1:20

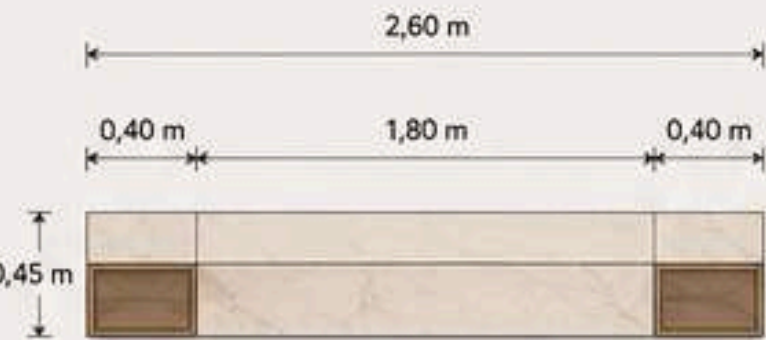

VISTA FRONTAL
ESCALA 1:20

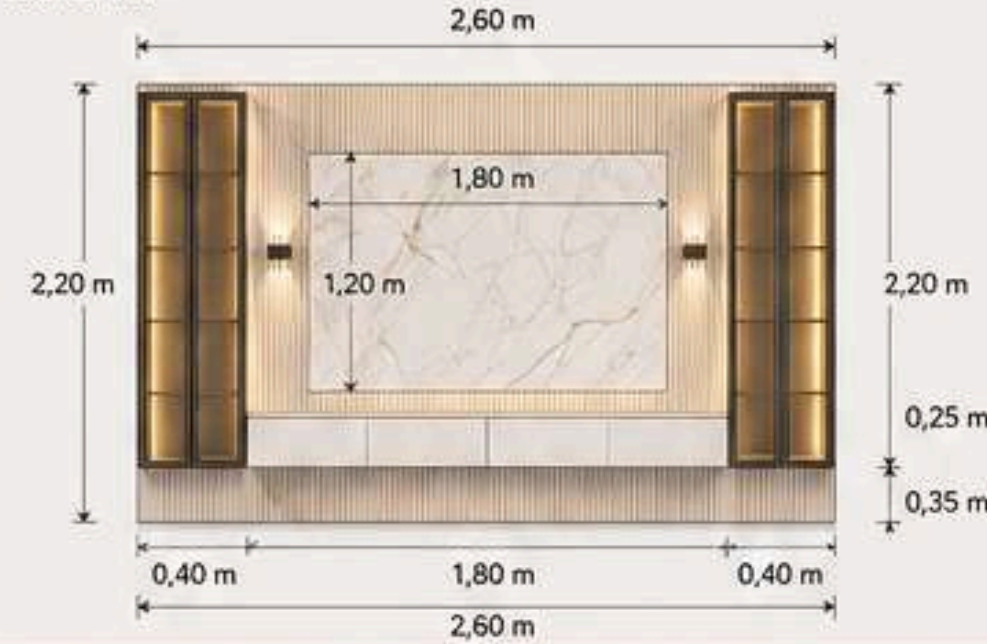

VISTA LATERAL
ESCALA 1:20

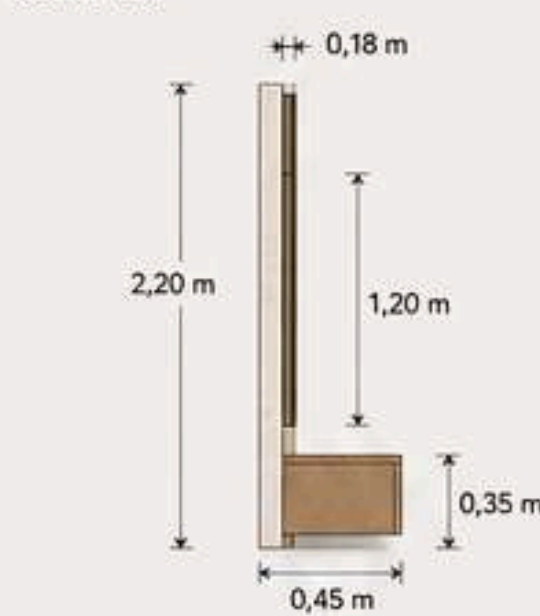

DETALHE RIPADO
ESCALA 1:10



DETALHE ENCONTRO 45°
(MEIA ESQUADRIA)
ESCALA 1:5




DETALHE PAINEL CENTRAL
ESCALA 1:10



CORTE TRANSVERSAL (PAINEL)
ESCALA 1:10



PASSO A PASSO DE EXCROS
ESCALA 1:10

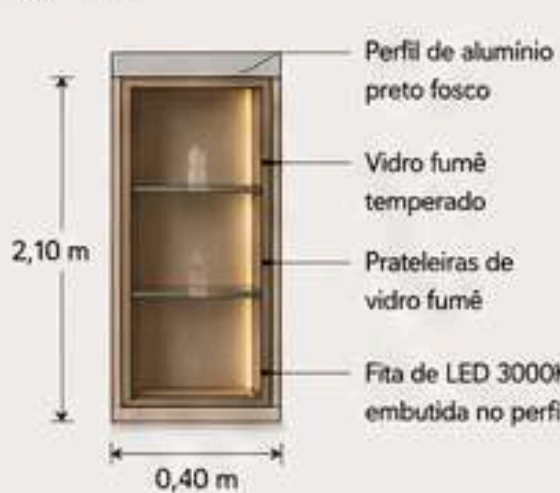


MEDIDAS E DISTÂNCIAS TÉCNICAS

- Altura total do painel (do piso ao teto): 2,20 m
- Largura total do painel: 2,60 m
- Largura do painel central (mármore): 1,80 m
- Altura do painel central (mármore): 1,20 m
- Profundidade do nicho do rack: 0,18 m
- Altura do rack suspenso: 0,35 m
- Profundidade do rack suspenso: 0,45 m
- Largura dos nichos laterais: 0,40 m
- Distância entre ripados: 0,02 m
- Espaçamento entre painel e rack: 0,25 m
- Altura da base do rack em relação ao piso: 0,35 m

SUGESTÃO DE METAIS E ACESSÓRIOS



ILUMINAÇÃO

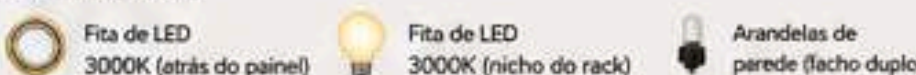


PASSO A PASSO DE EXECUÇÃO

- Marração da parede e verificação de esquadro e nivelamento.
- Fixação da base de alvenaria e regularização da superfície.
- Instalação das fitas de LED e passagem da fiação elétrica.
- Fixação do porcelanato Calacatta Gold com argamassa ACIII.
- Execução dos cortes em 45° (meia esquadria) nas junções.
- Instalação do ripado MDF com alinhamento e espaçamento.
- Instalação dos nichos com perfis de alumínio e vidros.
- Fixação do rack suspenso e ajustes do nivelamento.
- Instalação das arandelas e testes da iluminação.
- Limpeza final e conferência dos acabamentos.

PROJETO 10

PAINEL DE TV MONOLÍTICO EM PORCELANATO MARMORIZADO COM NICHOS ILUMINADOS E INTEGRAÇÃO DE TEXTURAS

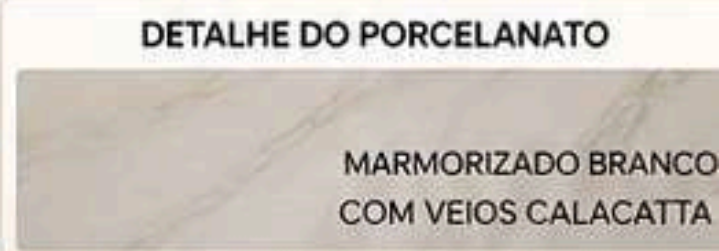

MEDIDAS TÉCNICAS DO PROJETO

Largura total do painel:	2,40 m a 3,20 m
Altura total do painel:	2,20 m a 2,60 m
Profundidade total do painel:	0,18 m a 0,22 m
Largura do nicho lateral:	0,35 m
Altura de cada nicho:	0,40 m
Profundidade dos nichos:	0,12 m
Distância entre nichos:	0,02 m
Distância entre nichos e ripado:	0,02 m
Área do painel central (TV):	1,10 m a 1,60 m (largura)
Altura da bancada inferior:	0,35 m a 0,45 m
Profundidade da bancada:	0,45 m a 0,50 m
Iluminação LED:	Fita LED embutida 3000K (luz quente)
Tensão LED recomendada:	12V
Potência recomendada:	9,6W/m

ESPECIFICAÇÕES TÉCNICAS DO PROJETO

Estilo do Projeto	Contemporâneo Moderno e Minimalista Integrado
Tipo de Porcelanato	Marmorizado Branco com Veios Calacatta (Grandes Formatos)
Técnica de Corte	Cortes Precisos em Meia Esquadria 45° e Acabamento Retificado
Aplicação	Painel de TV (Parede), Nichos Embutidos, Sanca de Teto e Piso (Área Social)
Rejunte	Rejunte Epóxi ou Acrílico na cor cinza claro (mínimo)
Iluminação	Fita LED embutida em perfis de alumínio
Acabamentos	Superfícies polidas, acabamento preciso e alinhamento perfeito

ANÁLISE DE DESIGN E FUNCIONAALIDADE

- Harmonia de Texturas e Luz:** O contraste sutil entre a superfície polida do mármore Calacatta e a textura ripada cria profundidade e sofisticação. A iluminação de LED embutida nos nichos e no contorno central valoriza o material e cria uma atmosfera acolhedora e elegante.
- Monolitismo e Continuidade:** O uso de grandes formatos de porcelanato marmorizado proporciona um visual limpo e contínuo, sem emendas aparentes, elevando o padrão do projeto.
- Funcionalidade Oculta:** Os nichos abertos com iluminação sutil e o rack suspenso oferecem funcionalidade sem comprometer o design limpo e moderno.

POR QUE ESTE PROJETO VALORIZA O SERVIÇO DE PORCELANATO?


- Valor Percebido e Exclusividade:** A aplicação de grandes formatos de porcelanato Calacatta no painel de TV e nichos cria um ambiente único e exclusivo, valorizando o imóvel.
- Precisão e Complexidade Técnica:** A execução de cortes de meia esquadria em grandes placas e a integração de perfis de iluminação exigem alto nível de habilidade técnica superior do profissional de porcelanato.
- Integração e Solução Monolítica:** A capacidade de criar volumes complexos e integrados (painel, nichos, rack) usando o mesmo material demonstra versatilidade do profissional e agrega valor significativo ao projeto.

PASSO A PASSO DO PROJETO


1 PLANEJAMENTO Definir medidas, layout dos nichos, pontos elétricos, iluminação e texturas.	2 MARCAÇÃO E CORTE Marcar e cortar as peças em meia esquadria (45°): nichos, painéis, ripados, bancada e detalhes.	3 PREPARAÇÃO DA PAREDE Nivelar e preparar a parede garantindo prumo, nivelamento e base adequada.	4 INSTALAÇÃO DOS NICHOS E PAINEL CENTRAL Fixar os nichos embutidos e o painel central com argamassa adequada, garantindo alinhamento.	5 INSTALAÇÃO DOS RIPADOS E SANCAS Instalar os ripados decorativos e a sanca de teto, garantindo alinhamento das texturas e encaixes.	6 INSTALAÇÃO DO LED Instalar fita LED embutida em perfil de alumínio nos nichos, sanca e contorno do painel central.	7 ACABAMENTO FINAL Aplicar rejunte fino, silicone nas juntas e limpar para entrega final impecável.
--	---	--	--	---	---	--

DETALHES TÉCNICOS E VISTAS


- Iluminação LED integrada valoriza a textura do mármore e cria atmosfera sofisticada.
- Cortes em meia esquadria (45°) garantem acabamento impecável sem emendas aparentes.
- Porcelanato marmorizado polido oferece elegância, durabilidade e fácil manutenção.

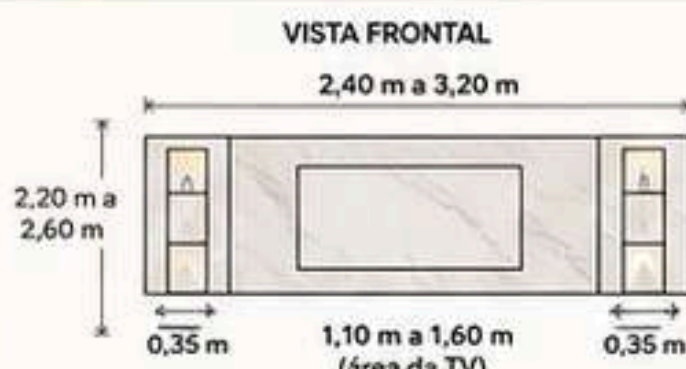

VISTA LATERAL (CORTE)

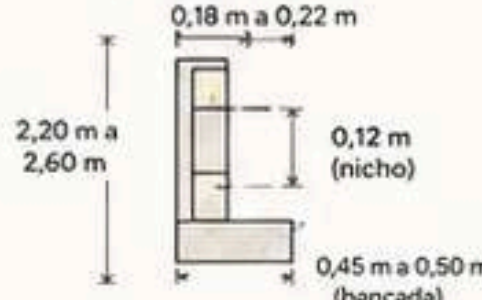

VISTA SUPERIOR (PLANTA)

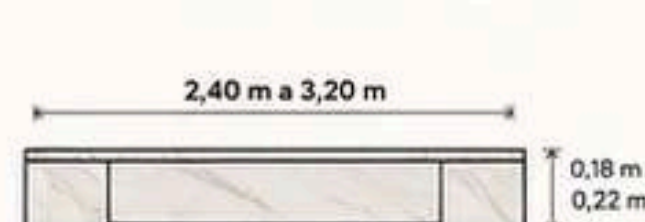

POR QUE ESTE PROJETO VALORIZA O SERVIÇO?

- Alto Valor Percebido:** Nichos iluminados e acabamento em mármore elevam o padrão do ambiente.
- Execução Técnica Avançada:** Cortes precisos, iluminação embutida e alinhamentos exigem




OBSERVAÇÕES PROFISSIONAIS

- Usar LED próprio para ambientes
- Tolerância de execução




ARQUITETURA DE VALOR


PAINEL DE TV EM PORCELANATO CALACATTA COM ESTANTES DE VIDRO ILUMINADAS E DETALHE RIPADO PERIMETRAL

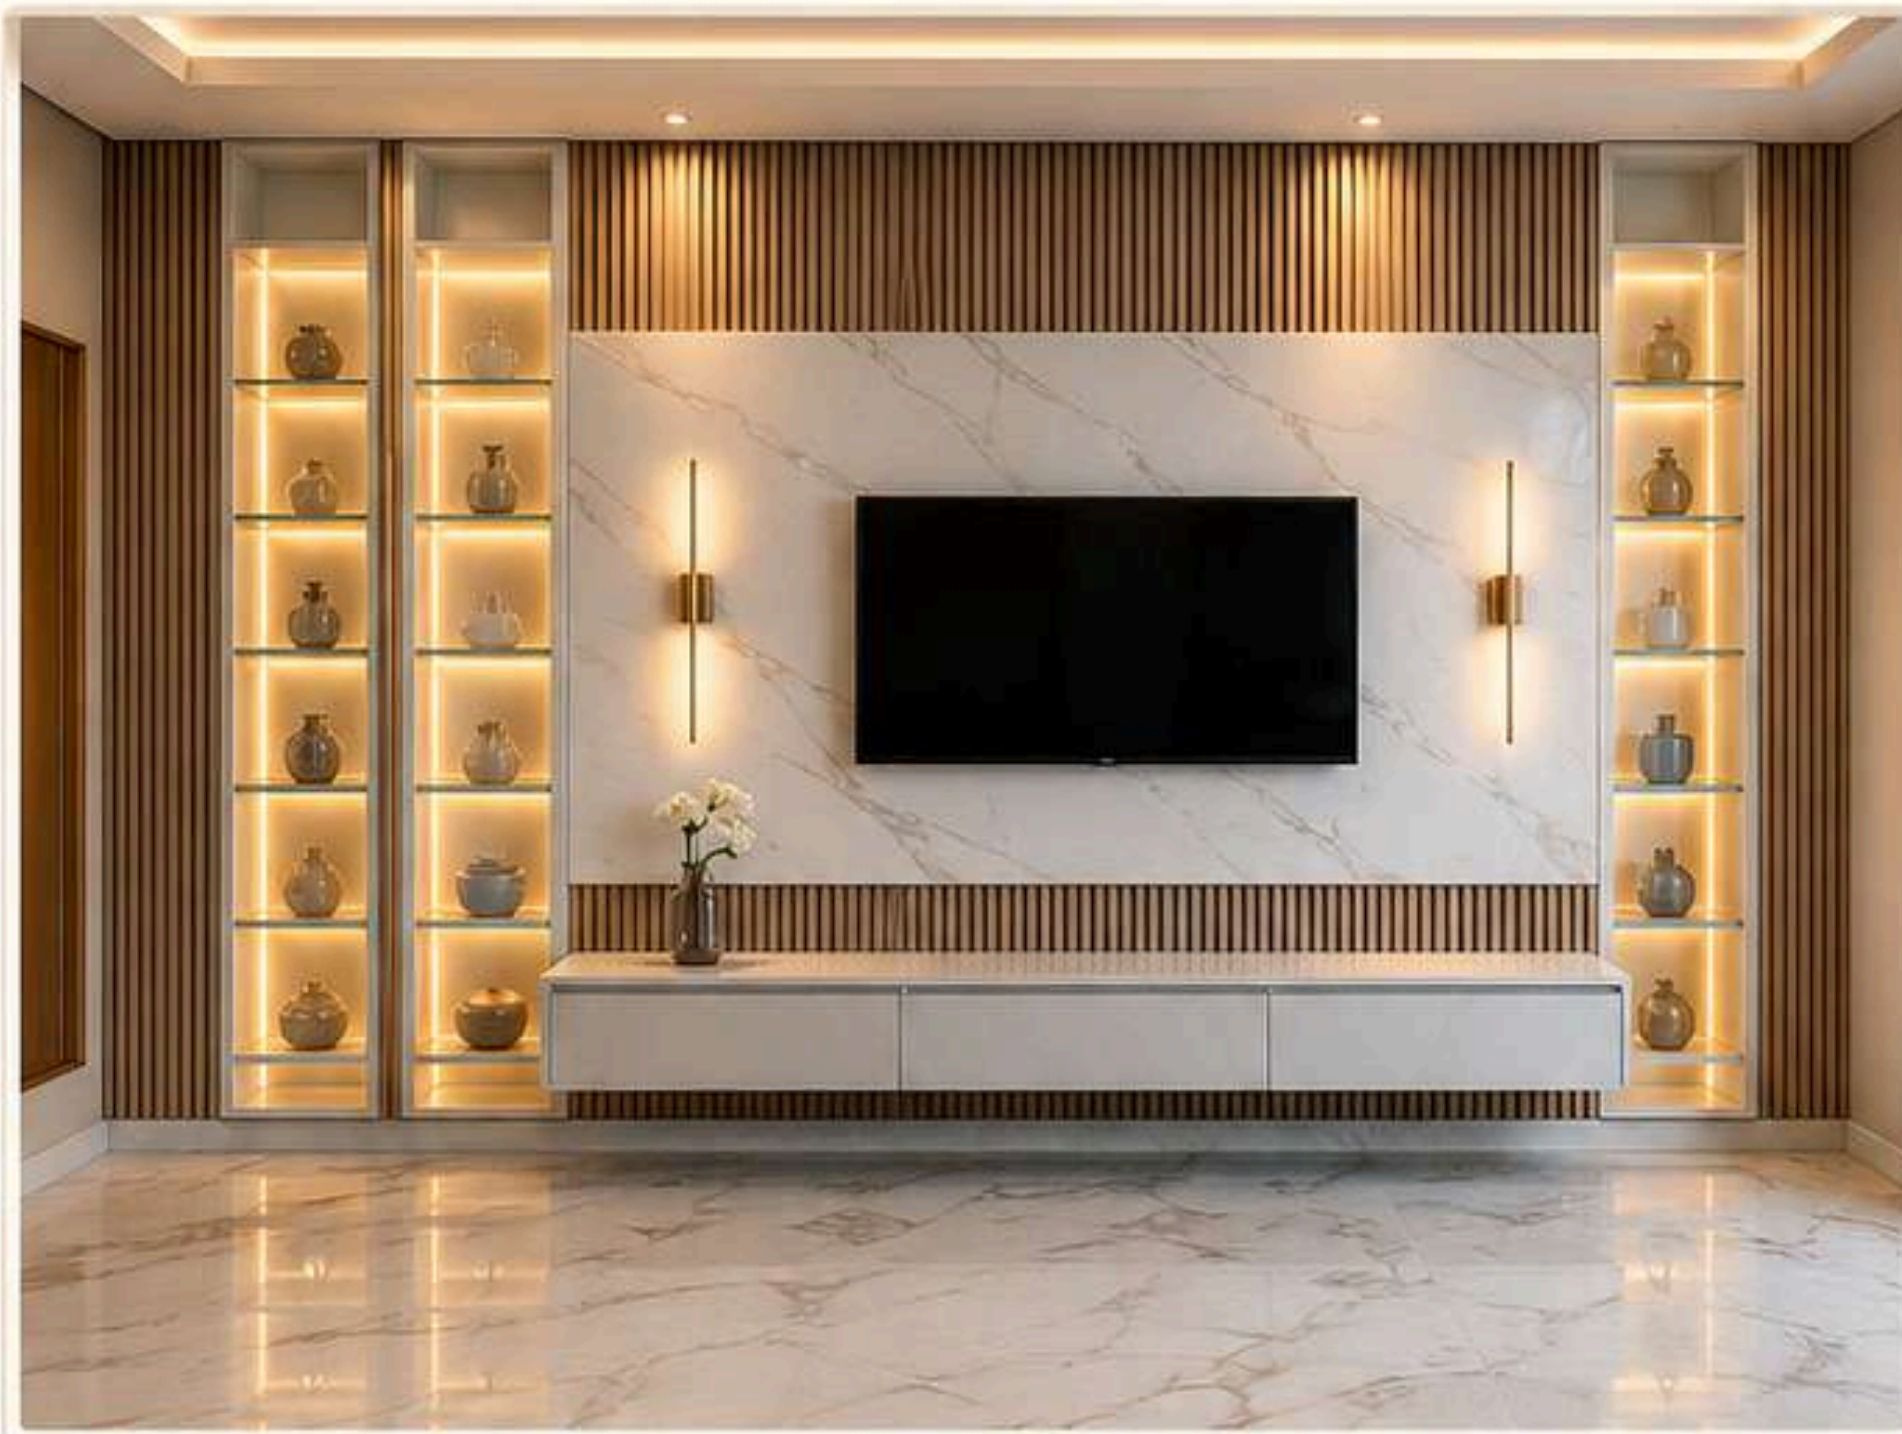


DETALHE DO ESTANTE DE VIDRO ILUMINADA

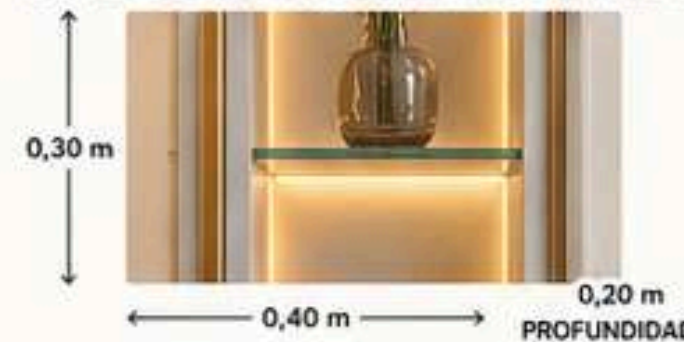

DETALHE DO RIPADO PERIMETRAL

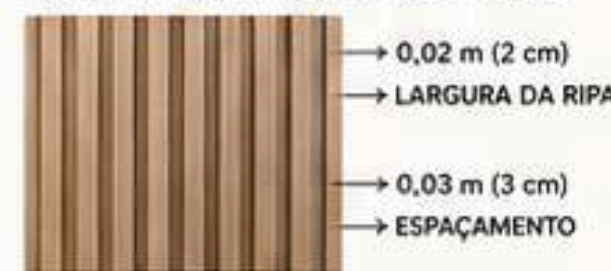

DETALHE DO PORCELANATO

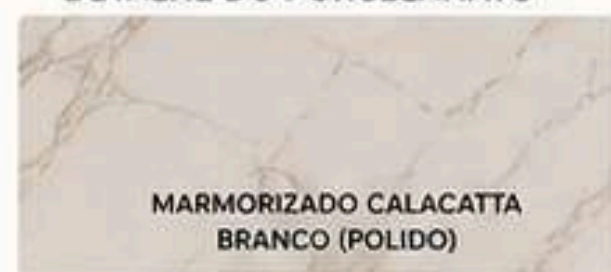

DETALHE DA SANCA (TETO)



MEDIDAS TÉCNICAS DO PROJETO

Largura total do painel:	2,60 m a 3,20 m
Altura total do painel:	2,40 m a 2,80 m
Profundidade total do painel:	0,22 m a 0,25 m
Largura do nicho central (TV):	1,40 m a 1,80 m
Altura do nicho central (TV):	1,00 m a 1,20 m
Largura das estantes laterais:	0,40 m cada
Profundidade das estantes:	0,20 m
Quantidade de prateleiras de vidro:	5 unidades por estante
Espessura do porcelanato (painel):	0,02 m (2 cm)
Espessura do tampo do rack:	0,02 m (2 cm)
Recuo do painel em relação à parede:	0,02 m a 0,03 m
Iluminação LED:	Fita LED 3000K (luz quente)
Tensão LED recomendada:	12V
Potência recomendada:	9,6W/m

ESPECIFICAÇÕES TÉCNICAS DO PROJETO

Estilo do Projeto:	Contemporâneo Moderno e Luxuoso
Tipo de Porcelanato:	Marmorizado de Aparência Calacatta (Branco/Cinza/Dourado Grandes Formatos) e Porcelanato Decorativo (Piso)
Técnica de Corte:	Execução de Grandes Formatos, Meia Esquadria 45° e Acabamento Retificado
Aplicação:	Painel de TV (Parede), Estantes de Vidro, Sanca de Gesso (Teto), Piso (Área Social)
Rejunte:	Rejunte Epóxi ou Acrílico na cor cinza claro (mínimo)
Iluminação:	Fita LED embutida nas estantes e atrás do painel
Acabamentos:	Superfícies polidas, acabamentos de alto padrão e integração de materiais (vidro, porcelanato e madeira ripada)

ANÁLISE DE DESIGN E FUNCIONALIDADE

- Sinergia de Materiais:** A combinação do porcelanato Calacatta polido com estantes de vidro iluminadas e ripado de madeira cria um visual moderno, sofisticado e com textura rica.
- Contrastes e Texturas Refinadas:** O contraste entre a nobreza do mármore, o calor da madeira e a transparência do vidro eleva o padrão estético do ambiente.
- Funcionalidade e Estética Integradas:** A iluminação integrada valoriza os objetos expostos e cria um ambiente acolhedor e elegante.
- Personalização e Exclusividade:** O projeto é único e adaptado ao espaço, refletindo o bom gosto e a personalidade do cliente.


PASSO A PASSO DO PROJETO

1 PLANEJAMENTO	2 MARCAÇÃO E CORTE	3 PREPARAÇÃO DA PAREDE	4 INSTALAÇÃO DO PAINEL E DOS NICHOS	5 INSTALAÇÃO DO RIPADO E DAS PRATELEIRAS	6 INSTALAÇÃO DA ILUMINAÇÃO LED	7 ACABAMENTO FINAL
Definir medidas do painel, posicionamento da TV, estantes, iluminação e detalhamento do ripado.	Marcar e cortar as placas de porcelanato em meia esquadria (45°), ripado e outros detalhes.	Nivelar e preparar a parede com impermeabilização e base resistente.	Fixar o painel central e as estantes embutidas com argamassa adequada, checar alinhamento.	Fixar o ripado perimetral e instalar prateleiras de vidro com suportes invisíveis ou metálicos.	Instalar fitas LED embutidas nas estantes e atrás do painel, conectar à fonte 12V.	Aplicar rejunte, silicone nas juntas, limpeza fina e verificação da iluminação.

DETALHES TÉCNICOS E VISTAS

- Iluminação LED integrada realça o design e cria ambiente sofisticado.
- Cortes em meia esquadria (45°) garantem acabamento impecável e sem quinas aparentes.
- Integração de materiais (porcelanato, vidro e ripado) oferece equilíbrio estético e durabilidade.


VISTA FRONTAL

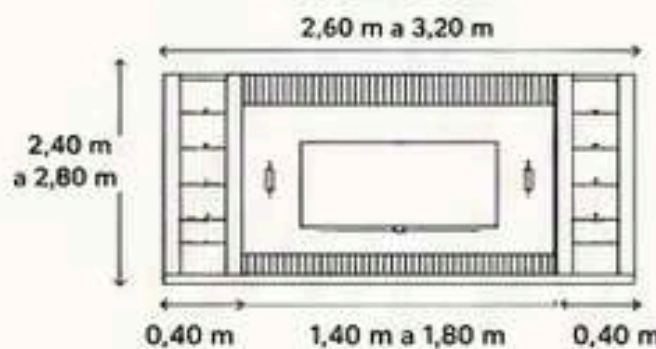

VISTA LATERAL (CORTE)



VISTA SUPERIOR (PLANTA)

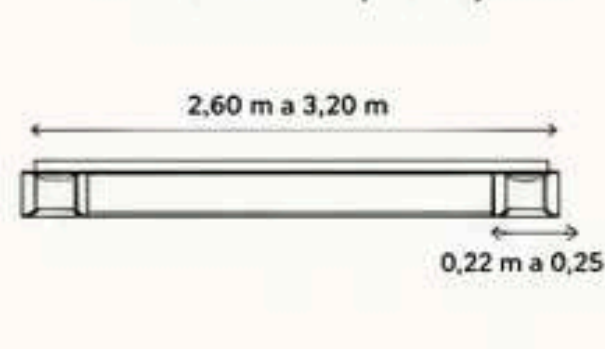



PROJETO 13

PAINEL DE TV EM PORCELANATO CALACATTA GOLD COM
ESTANTE DE MADEIRA LUZ-LEITOSA E DETALHES RIPADOS



ESPECIFICAÇÕES TÉCNICAS DO PROJETO	
Estilo do Projeto	Contemporâneo Minimalista
Tipo de Porcelanato	Marmorizado Calacatta Gold Grandes Formatos (Branco/Dourado/Preto). Ripado Amadeirado.
Técnica de Corte	Execução de Grandes Formatos, Cortes em 45° e Acabamento Retificado
Aplicação	Painel de TV (Parede), Estante de Madeira com Prateleiras de Vidro, Rack e Pannel Ripado (Área Social).

MATERIAIS E ACABAMENTOS	
• Porcelanato Calacatta Gold (Painel) 160 x 100 cm (peça única)	
• Pannel Ripado Amadeirado	
• MDF Amadeirado (Carvalho/Melamina BP)	
• Vidro Fumê 6 mm (Portas de Correr)	
• Fita de LED Luz Quente 3000K	
• Perfil de LED Embutido (Alumínio)	
• Suportes Invisíveis para Prateleira	
• Parafusos, buchas e cola PU	

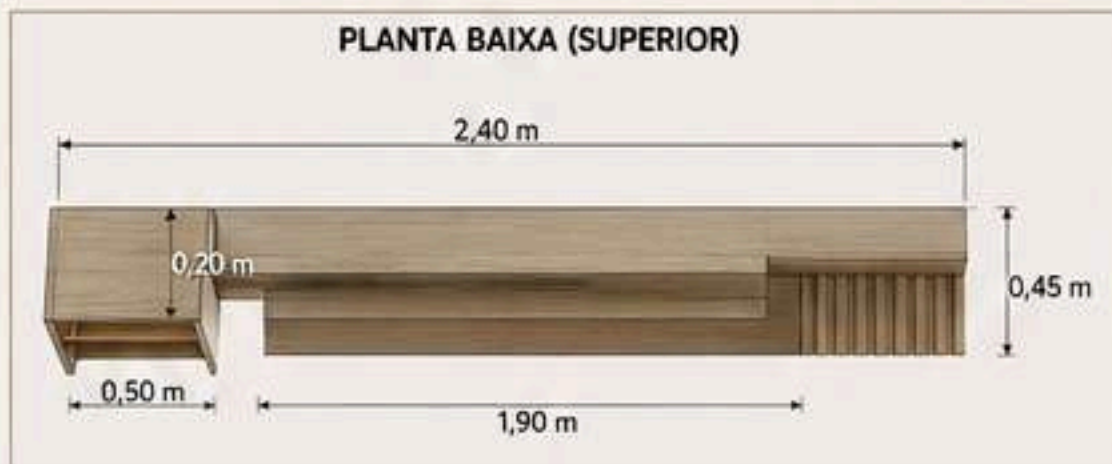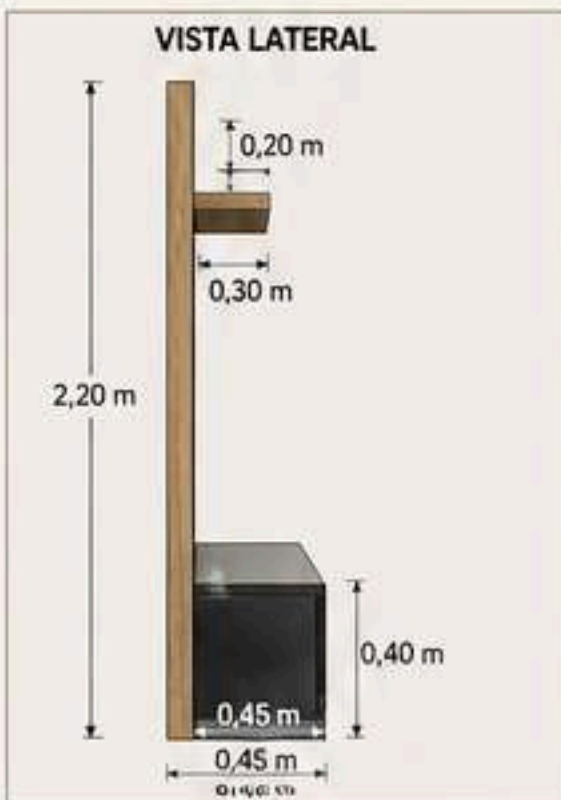

DETALHES CONSTRUTIVOS

DET. 01 - PRATELEIRA SUPERIOR

Fixação invisível com suporte oculto

DET. 02 - RIPADO EM MDF

Ripado MDF 2x3 cm espaçamento 1 cm

DET. 03 - NICHOS COM LED

Fita de LED embutida na parte superior

SUGESTÃO DE PORCELANATO

Calacatta Gold
120x120 cm ou 160x100 cm
Acabamento Polido Retificado

SUGESTÃO DE METAIS E ACESSÓRIOS

Perfil de LED Embutido

Suporte Invisível para Prateleira

Puxador Perfil Preto Fosco

Porta de Correr Vidro Fumê

Fita de LED 3000K

PASSO A PASSO EXECUTIVO

01 **PLANEJAMENTO E MARCAÇÃO**
Meça o ambiente e marque os pontos de fixação na parede (respeitando as medidas do projeto).

02 **FIXAÇÃO DA BASE E RACK**
Instale o rack suspenso nivelado na parede com parafusos e buchas adequadas.

03 **INSTALAÇÃO DO PAINEL RIPADO**
Fixe o pannel ripado MDF do lado direito da estrutura com cola PU e parafusos de acabamento.

04 **FIXAÇÃO DO PAINEL DE PORCELANATO**
Aplique cola PU no verso do porcelanato e fixe no centro do pannel. Utilize espaçadores e nivelamento.

05 **INSTALAÇÃO DAS PRATELEIRAS E NICHOS**
Fixe a coluna lateral (nicho) e as prateleiras de vidro com suportes invisíveis. Instale a prateleira superior.

06 **INSTALAÇÃO DA ILUMINAÇÃO LED**
Instale os perfis de LED nas prateleiras e nichos e faça a ligação elétrica (usar fonte adequada).

07 **INSTALAÇÃO DAS PORTAS DE VIDRO**
Encaixe as portas de correr de vidro fumê no trilho superior e inferior do rack.

08 **ACABAMENTOS FINAIS**
Verifique o nivelamento, faça ajustes e limpeza geral de todos os acabamentos.

DICAS IMPORTANTES

- Use porcelanato de grandes formatos com argamassa ACIII ou cola PU para melhor fixação.
- Reforce a parede para suportar o peso do pannel e do rack.
- Planeje a passagem da fiação antes de fechar o pannel.
- Utilize mão de obra especializada para cortes em 45° e instalação do porcelanato.

ILUMINAÇÃO RECOMENDADA

LED Fita 3000K

LED Perfil Embutido

LED Spot Direcionável


PROJETO 14

PAINEL DE TV GEOMÉTRICO CÊNICO EM PORCELANATO CALACATTA E OURO COM RIPADO E VITRINE INTEGRADA



ESPECIFICAÇÕES TÉCNICAS DO PROJETO	
Estilo do Projeto	Contemporâneo Artístico / Luxo Integrado
Tipo de Porcelanato	Marmorizado Calacatta (Branco/Cinza/Dourado) Ripado de Madeira de Aparência Natural
Técnica de Corte	Execução de Cortes Complexos, Composições Geométricas e Montagem 3D e Acabamento Retificado
Aplicação	Painel de TV (Parede), Vitrine Flanqueadora, Rack Suspensão e Piso (Área Social)

MATERIAIS E ACABAMENTOS	
• Porcelanato Calacatta Gold 120 x 120 cm (peça única)	
• Ripado MDF ou Madeira (freijó ou nogueira)	
• MDF Ultra ou Duratex (cor Branco)	
• Vidro Temperado 6 mm	
• Perfis de LED Embutido (Alumínio)	
• Fita de LED 3000K (Luz Quente)	
• Suportes Invisíveis para Prateleiras	
• Parafusos, buchas e cola PU	

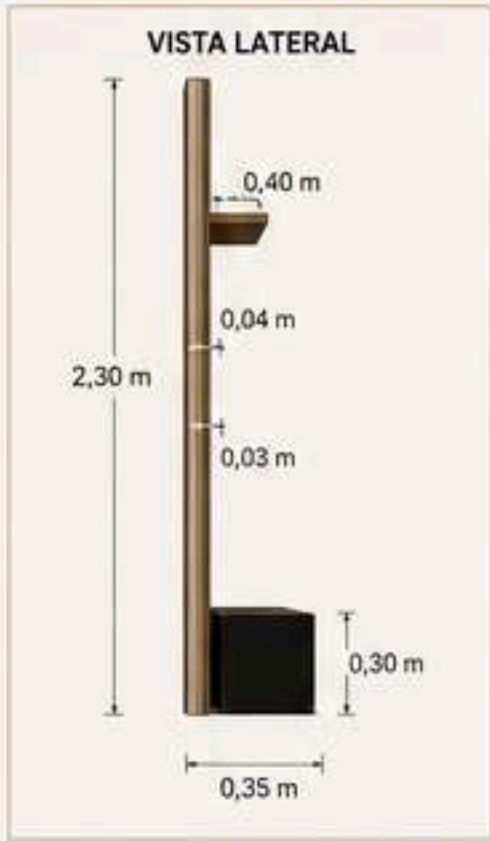

DETALHES CONSTRUTIVOS			
DET. 01 - PAINEL GEOMÉTRICO 3D	DET. 02 - RIPADO	DET. 03 - LED EMBUTIDO	DET. 04 - VITRINE
Espessura do porcelanato 0,9 cm a 1,2 cm			
Peças com cortes geométricos e desníveis	Ripado MDF ou Madeira Fixado sobre o painel	Perfil de LED embutido Iluminação indireta 3000K	Prateleiras de vidro 6mm com suporte invisível

SUGESTÃO DE PORCELANATO
Calacatta Gold 120x120 cm ou 120x250 cm Retificado Polido

SUGESTÃO DE METAIS E ACESSÓRIOS				
Perfil de LED Embutido	Suporte Invisível para Prateleira	Puxador Perfil Preto Fosco	Dobradiça Slow Motion	Fita de LED 3000K

PASSO A PASSO EXECUTIVO	
01	PLANEJAMENTO E MARCAÇÃO Meça o ambiente e marque os pontos de fixação na parede (respeitando as medidas do projeto).
02	INSTALAÇÃO DO RACK SUSPENSO Fixe o rack na parede com buchas e parafusos adequados, garantindo nivelamento perfeito.
02	FIXAÇÃO DO PAINEL GEOMÉTRICO Aplique cola PU no verso das peças de porcelanato e fixe no painel de base com cortes precisos.
04	INSTALAÇÃO DO RIPADO Fixe o ripado MDF ou madeira na lateral com cola PU e parafusos finos (se necessário).
05	INSTALAÇÃO DA VITRINE Instale a estrutura da vitrine e as prateleiras de vidro com suportes invisíveis.
06	INSTALAÇÃO DA ILUMINAÇÃO LED Instale os perfis de LED embutidos atrás do painel, ripado e no forro de gesso.
07	PASSAGEM DE FIAÇÃO Passe toda a fiação elétrica de forma segura e discreta, ligando aos pontos de energia.
08	ACABAMENTOS E LIMPEZA Faça o acabamento das junções com silicone neutro, limpe resíduos e confira alinhamentos.
09	TESTE FINAL Teste toda a iluminação e verifique a fixação de todos os elementos.

- DICAS IMPORTANTES**
- Use porcelanato de grandes formatos com argamassa ACIII ou cola PU para melhor fixação.
 - Reforce a parede para suportar o peso do painel, rack e vitrine.
 - Planeje a passagem da fiação antes da fixação dos painéis.
 - Contrate mão de obra especializada para cortes geométricos e montagem do painel.

ILUMINAÇÃO RECOMENDADA			
	LED Fita 3000K		LED Perfil Embutido
			LED Spot Direcionável




PROJETO 15

PAINEL DE TV EM PORCELANATO CALACATTA 'BOLD' COM DETALHE RIPADO E PISO MARMORIZADO CINZA



ESPECIFICAÇÕES TÉCNICAS DO PROJETO	
Estilo do Projeto	Contemporâneo Minimalista e Monolítico
Tipo de Porcelanato	Marmorizado de Aparência Calacatta 'Bold' (Preto/Branco) e Marmorizado Cinza (Piso)
Técnica de Corte	Execução de Grandes Formatos, Cortes em 45° e Acabamento Retificado
Aplicação	Painel de TV (Parede Central), Piso Marmorizado e Nichos de Teto Mobiliário.

MATERIAIS E ACABAMENTOS	
• Porcelanato Calacatta 'Bold' (Painel)	160 x 120 cm (peça única)
• Porcelanato Marmorizado Cinza (Piso)	120x120 cm
• MDF Ultra ou Duratex (cor Branco Fosco)	
• Ripado MDF Cinza (Frisos 2,7 cm)	
• Fita de LED 3000K (Luz Quente)	
• Perfis de LED Embutido (Alumínio)	
• Suportes Invisíveis para Prateleiras	
• Parafusos, buchas e cola PU	

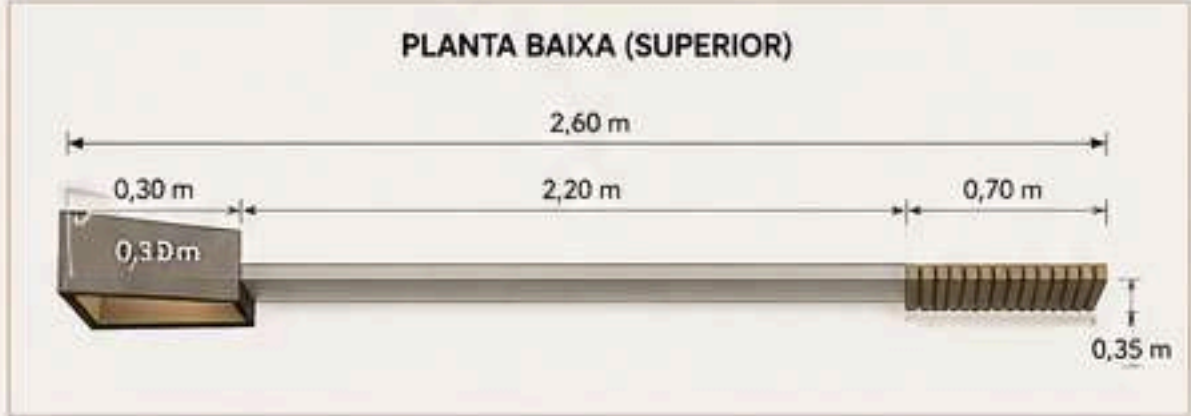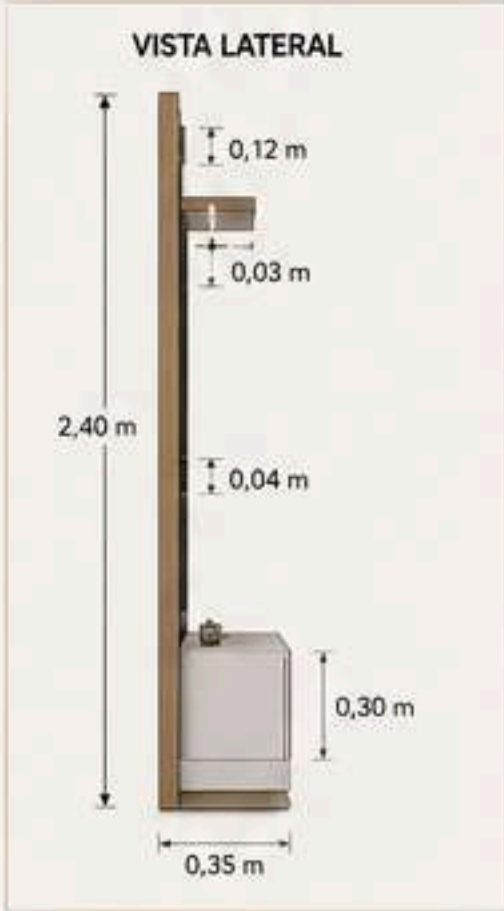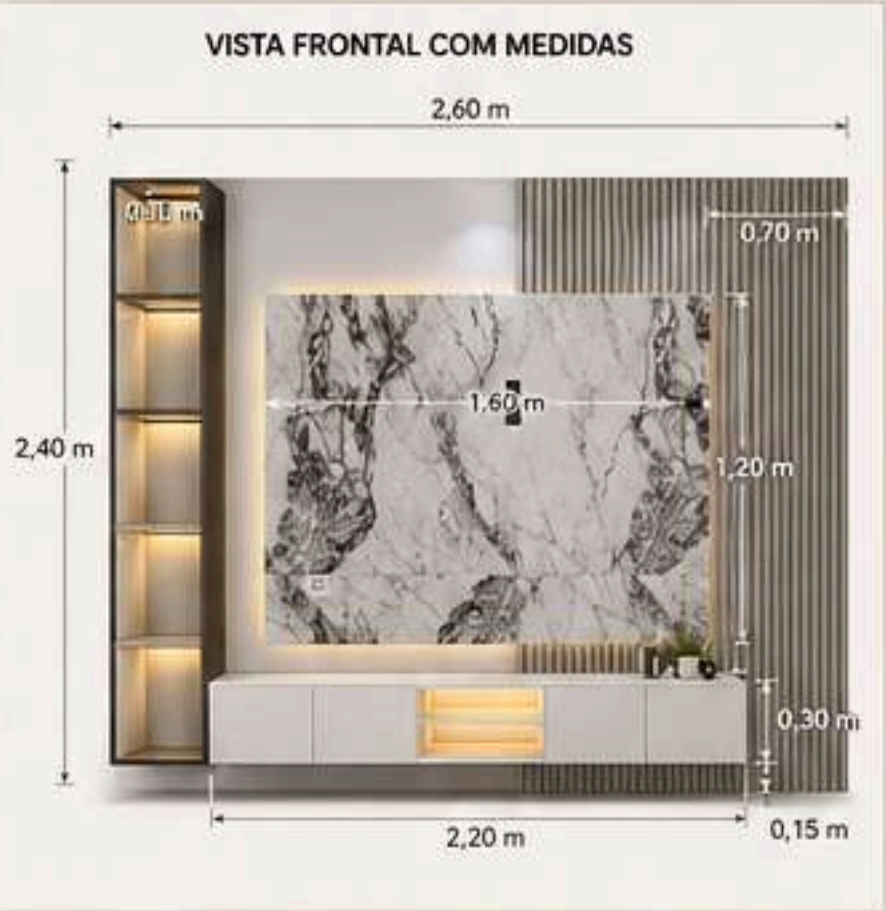

DETALHES CONSTRUTIVOS E MATERIAIS				
DET. 01 - PAINEL CALACATTA 'BOLD'	DET. 02 - RIPADO MDF CINZA	DET. 03 - NICHOS VERTICAIS	DET. 04 - NICHOS CENTRAIS	DET. 05 - PISO MARMORIZADO
160 x 120 cm Espessura 0,9 cm Acabamento Retificado	Frisos MDF Cinza Espaçamento 1 cm	Iluminação LED embutida em todos os níveis	Fita de LED embutida Luz Quente 3000K	Porcelanato Cinza 120x120 cm Acabamento Polido

SUGESTÃO DE METAIS E ACESSÓRIOS					
Perfil de LED Embutido	Suporte Invisível para Nichos	Puxador Cava Branco Fosco	Dobradiça Slow Motion	Fita de LED 3000K	Parafusos e Buchas

DICAS IMPORTANTES	
• Utilize porcelanato de grandes formatos com argamassa ACIII ou cola PU para melhor fixação.	• Alinhe o ripado com linha a laser para um acabamento perfeito.
• Planeje a passagem da fiação antes da instalação do painel.	• Contrate mão de obra especializada para cortes em 45° e instalação do porcelanato.
• Utilize niveladores de porcelanato para um resultado impecável.	

PASSO A PASSO EXECUTIVO	
01	PLANEJAMENTO E MARCAÇÃO Meça o ambiente e marque os pontos de fixação na parede (respeitando as medidas do projeto).
02	INSTALAÇÃO DOS RACK SUSPENSO E NICHOS Fixe o rack suspenso na parede com buchas e parafusos adequados e instale os nichos verticais com suporte oculto.
03	INSTALAÇÃO DO PAINEL DE PORCELANATO Aplique cola PU no verso da peça Calacatta 'Bold' e fixe no centro da parede. Utilize espaçadores e nivelamento.
04	INSTALAÇÃO DO RIPADO Cole os frisos ripados de MDF cinza com cola PU, alinhando com as medidas do projeto.
05	INSTALAÇÃO DA ILUMINAÇÃO LED Instale as fitas de LED 3000K nos nichos, no painel e no nicho central do rack. Ligue aos perfis embutidos.
06	LIMPEZA E ACABAMENTOS FINAIS Faça rejuntas, limpezas e ajuste de todos os acabamentos visíveis.
07	PASSAGEM DE FIAÇÃO Passe toda a fiação de forma discreta por trás do painel e nos nichos.
08	TESTE FINAL Teste toda a iluminação e verifique a fixação dos elementos.
09	ENTREGA E MANUTENÇÃO Oriente o cliente sobre limpeza e cuidados com o porcelanato e iluminação.

ILUMINAÇÃO RECOMENDADA			
	LED Fita 3000K		LED Perfil Embutido
			LED Spot Direcional





PROJETO 16

SOLUÇÃO DE TV MONOLÍTICA COM PAINEL CALACATTA E MARCENARIA ILUMINADA



ESPECIFICAÇÕES TÉCNICAS DO PROJETO	
Estilo do Projeto	Contemporâneo Minimalista e Luxuoso.
Tipo de Porcelanato	Revestimento Marmorizado de Aparência Calacatta (Branco/Cinza). Grandes Formatos.
Técnica de Corte	Execução de Grandes Formatos, Cortes em 45° e Acabamento Retificado
Aplicação	Painel de TV (Parede Central).

MATERIAIS E ACABAMENTOS	
- Porcelanato Calacatta (Painel) 160 x 120 cm (peça única) - MDF Ultra ou Duratex (cor Branco Fosco) - Fita de LED 3000K (Luz Quente) - Perfis de LED Embutido (Alumínio) - Ripado MDF (frisos 2,7 cm) na cor Cinza Claro - Suportes Invisíveis para Prateleiras - Parafusos, buchas e cola PU	

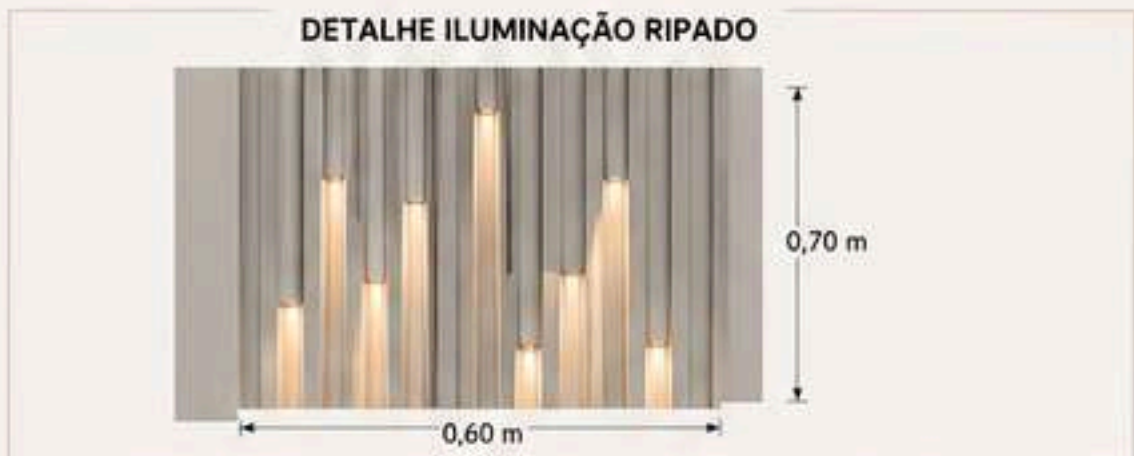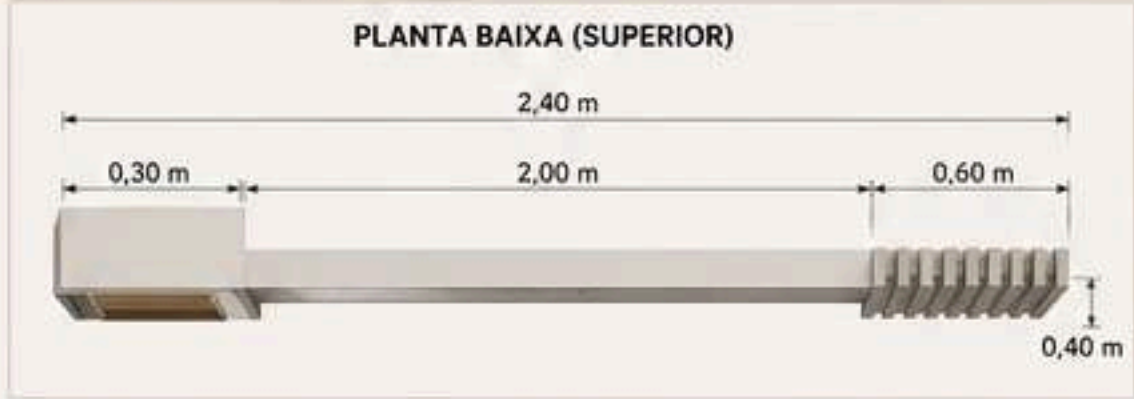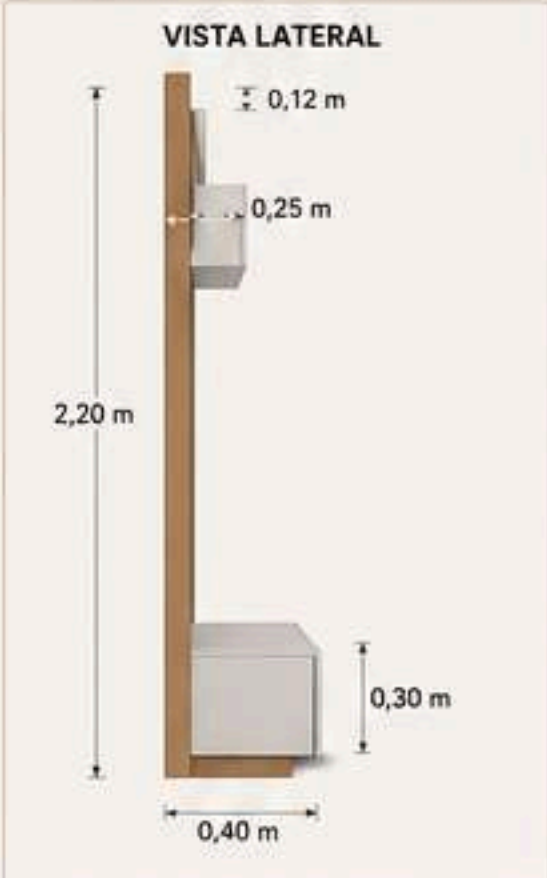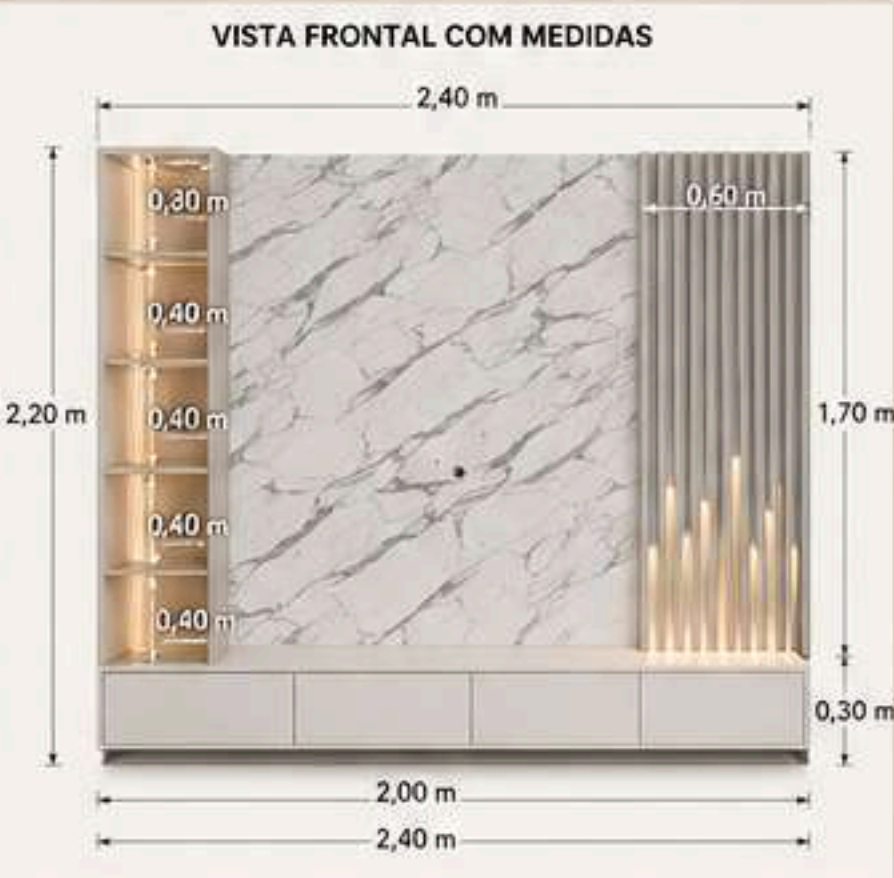

DETALHES CONSTRUTIVOS E MATERIAIS				
DET. 01 - PAINEL CALACATTA	DET. 02 - NICHOS ILUMINADOS	DET. 03 - RIPADO VERTICAL	DET. 04 - ILUMINAÇÃO RIPADO	DET. 05 - MARCENARIA
160 x 120 cm Peça única Acabamento Retificado	Prateleiras em MDF com LED embutido	MDF Ripado Cinza Claro Espaçamento 1 cm	Perfis de LED Embutidos Luz Quente 3000K	MDF Branco Fosco Sistema de abertura Push to Open

SUGESTÃO DE METAIS E ACESSÓRIOS				
Perfil de LED Embutido	Suporte Invisível para Prateleira	Parafusos e Buchas	Fita de LED 3000K	Fonte 12V Slim

DICAS IMPORTANTES	
- Utilize porcelanato de grandes formatos com argamassa ACIII ou cola PU para melhor fixação. - Alinhe o ripado com linha a laser para um acabamento perfeito. - Planeje a passagem da fiação antes da fixação do painel. - Contrate mão de obra especializada para cortes em 45° e instalação do porcelanato. - Use espaçadores e sistema de nivelamento para um resultado impecável.	

PASSO A PASSO EXECUTIVO	
01	PLANEJAMENTO E MARCAÇÃO Meça o ambiente e marque os pontos de fixação na parede (respeitando as medidas do projeto).
02	INSTALAÇÃO DO PAINEL DE PORCELANATO Aplique cola PU no verso da peça Calacatta e fixe no centro da parede. Utilize espaçadores e nivelamento.
03	INSTALAÇÃO DOS NICHOS LATERAIS Fixe os nichos laterais na parede com parafusos adequados e confira o nivelamento.
04	INSTALAÇÃO DO RIPADO Cole os frisos ripados de MDF cinza claro com cola PU, alinhando sempre as medidas do projeto.
05	INSTALAÇÃO DA ILUMINAÇÃO LED Instale os perfis de LED nos nichos e no ripado vertical e conecte à fonte 12V.
06	INSTALAÇÃO DA MARCENARIA Fixe o móvel suspenso com suportes invisíveis nivelados na parede.
07	LIGAÇÃO ELÉTRICA Conecte a fita de LED à fonte 12V e realize os testes de funcionamento.
08	ACABAMENTOS E LIMPEZA Faça os ajustes finais, vedações com silicone neutro e limpeza dos acabamentos.
09	TESTE FINAL Teste toda a iluminação e verifique a fixação de todos os elementos.

ILUMINAÇÃO RECOMENDADA			
	LED Fita 3000K		LED Perfil Embutido
	LED Spot Direcionável		




PROJETO 15

PAINEL DE TV EM PORCELANATO CALACATTA 'BOLD' COM DETALHE RIPADO E PISO MARMORIZADO CINZA



ESPECIFICAÇÕES TÉCNICAS DO PROJETO	
Estilo do Projeto	Contemporâneo Minimalista e Monolítico
Tipo de Porcelanato	Marmorizado de Aparência Calacatta 'Bold' (Preto/Branco) e Marmorizado Cinza (Piso)
Técnica de Corte	Execução de Grandes Formatos, Cortes em 45° e Acabamento Retificado
Aplicação	Painel de TV (Parede Central), Piso Marmorizado e Nichos de Teto Mobiliário.

MATERIAIS E ACABAMENTOS	
• Porcelanato Calacatta 'Bold' (Painel)	160 x 120 cm (peça única)
• Porcelanato Marmorizado Cinza (Piso)	120x120 cm
• MDF Ultra ou Duratex (cor Branco Fosco)	
• Ripado MDF Cinza (Frisos 2,7 cm)	
• Fita de LED 3000K (Luz Quente)	
• Perfis de LED Embutido (Alumínio)	
• Suportes Invisíveis para Prateleiras	
• Parafusos, buchas e cola PU	

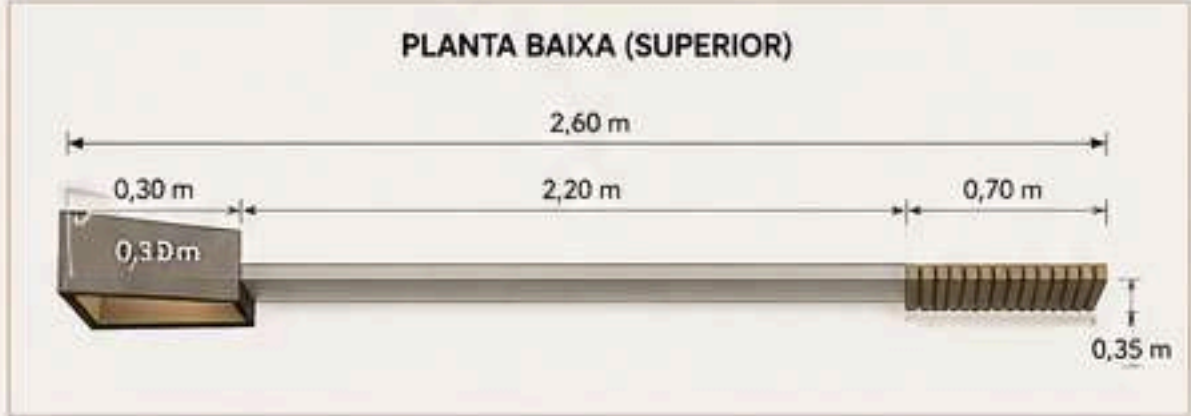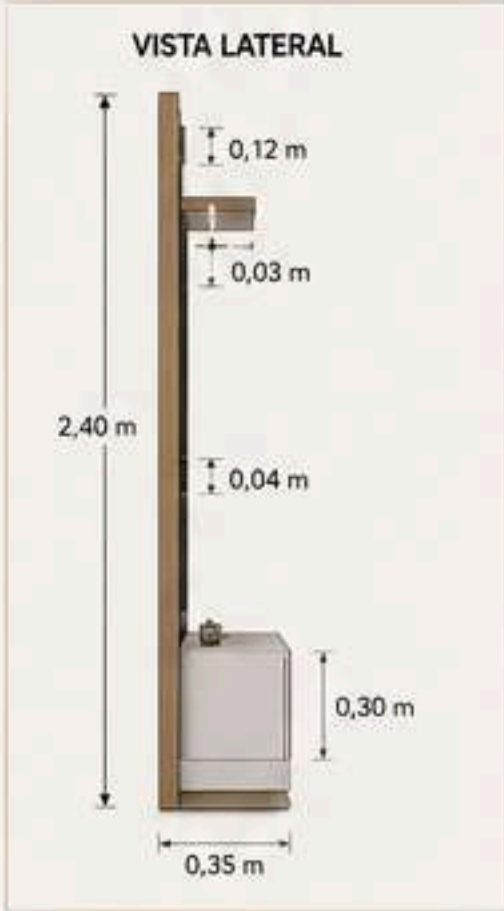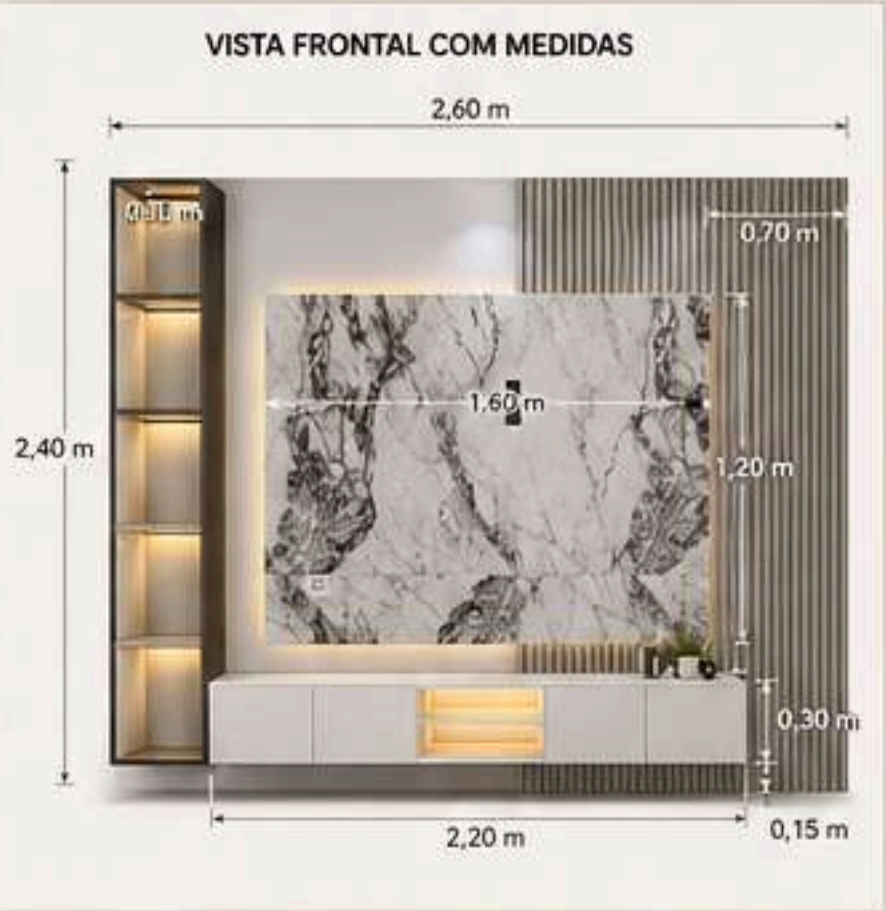

DETALHES CONSTRUTIVOS E MATERIAIS				
DET. 01 - PAINEL CALACATTA 'BOLD'	DET. 02 - RIPADO MDF CINZA	DET. 03 - NICHOS VERTICAIS	DET. 04 - NICHOS CENTRAIS	DET. 05 - PISO MARMORIZADO
160 x 120 cm Espessura 0,9 cm Acabamento Retificado	Frisos MDF Cinza Espaçamento 1 cm	Iluminação LED embutida em todos os níveis	Fita de LED embutida Luz Quente 3000K	Porcelanato Cinza 120x120 cm Acabamento Polido

SUGESTÃO DE METAIS E ACESSÓRIOS					
Perfil de LED Embutido	Suporte Invisível para Nichos	Puxador Cava Branco Fosco	Dobradiça Slow Motion	Fita de LED 3000K	Parafusos e Buchas

DICAS IMPORTANTES	
• Utilize porcelanato de grandes formatos com argamassa ACIII ou cola PU para melhor fixação.	• Alinhe o ripado com linha a laser para um acabamento perfeito.
• Planeje a passagem da fiação antes da instalação do painel.	• Contrate mão de obra especializada para cortes em 45° e instalação do porcelanato.
• Utilize niveladores de porcelanato para um resultado impecável.	

PASSO A PASSO EXECUTIVO	
01	PLANEJAMENTO E MARCAÇÃO Meça o ambiente e marque os pontos de fixação na parede (respeitando as medidas do projeto).
02	INSTALAÇÃO DOS RACK SUSPENSO E NICHOS Fixe o rack suspenso na parede com buchas e parafusos adequados e instale os nichos verticais com suporte oculto.
03	INSTALAÇÃO DO PAINEL DE PORCELANATO Aplique cola PU no verso da peça Calacatta 'Bold' e fixe no centro da parede. Utilize espaçadores e nivelamento.
04	INSTALAÇÃO DO RIPADO Cole os frisos ripados de MDF cinza com cola PU, alinhando com as medidas do projeto.
05	INSTALAÇÃO DA ILUMINAÇÃO LED Instale as fitas de LED 3000K nos nichos, no painel e no nicho central do rack. Ligue aos perfis embutidos.
06	LIMPEZA E ACABAMENTOS FINAIS Faça rejuntas, limpezas e ajuste de todos os acabamentos visíveis.
07	PASSAGEM DE FIAÇÃO Passe toda a fiação de forma discreta por trás do painel e nos nichos.
08	TESTE FINAL Teste toda a iluminação e verifique a fixação dos elementos.
09	ENTREGA E MANUTENÇÃO Oriente o cliente sobre limpeza e cuidados com o porcelanato e iluminação.

ILUMINAÇÃO RECOMENDADA			
	LED Fita 3000K		LED Perfil Embutido
			LED Spot Direcional